

Flight of a Legless Bird

REVISED: 3/6/24





PLATE SCHEDULE:


- 1.0 Section 10' Borders
- 1.1 Section 15' Borders
- 2.0 Electrics
- 2.1 Ground Units
- 2.2 Catwalks
- 3.0 Booms

Flight of a
Legless Bird

DATE:
3/6/24

DRAWN BY:
Kerstin Fagerstrom
kerstinf@princeton.edu

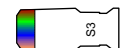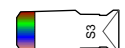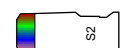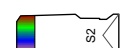- LIGHTING UNITS:
-  ETC LED Series 3 Fresnel
 -  ETC LED Series 3 Leko 19'
 -  ETC LED Series 3 Leko 26'
 -  ETC LED Series 3 Leko 36'
 -  ETC LED Series 3 Leko 50'
 -  ETC LED Series 2 Leko 36'
 -  ETC LED Series 2 Leko 50'
 -  ETC D60 Vivid
 -  MAC Encore

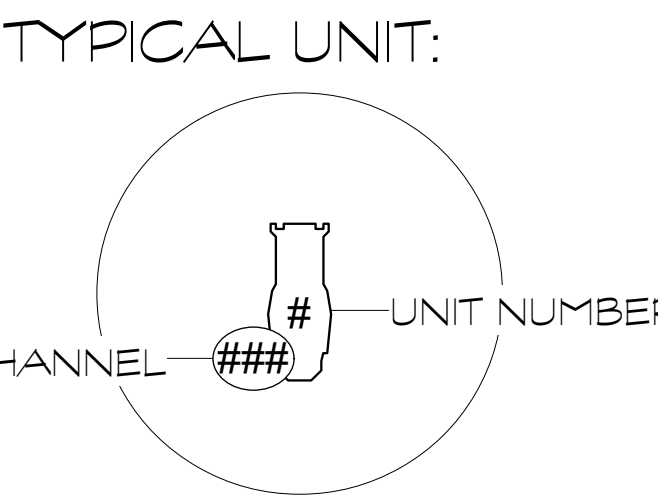

- All units hung on 18" centers unless otherwise specified.
- Written dimensions take precedence over scale measurements.
- Trims are from stage floor to sidearm/pipe.

DRAWING TITLE
Cover

PLATE NUMBER:
0.0

SCALE:
N/A


BERLIND THEATRE
Princeton University
Princeton, NJ

DATE:
3/6/24

DRAWN BY:
Kerstin Fagerstrom
kerstinf@princeton.edu

- LIGHTING UNITS:
- ETC LED Series 3 Fresnel
 - ETC LED Series 3 Leko 19"
 - ETC LED Series 3 Leko 26"
 - ETC LED Series 3 Leko 36"
 - ETC LED Series 3 Leko 50"
 - ETC LED Series 2 Leko 36"
 - ETC LED Series 2 Leko 50"
 - ETC D60 Vivid
 - MAC Encore

TYPICAL UNIT:

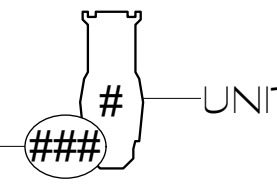CHANNEL  UNIT NUMBER


- All units hung on 18" centers unless otherwise specified.
- Written dimensions take precedence over scale measurements.
- Trims are from stage floor to sidearm/pipe.

DRAWING TITLE
Section - 10' Border

PLATE NUMBER:
1.0

SCALE:
1/4" = 1'0"

BERLIND THEATRE
Princeton University
Princeton, NJ

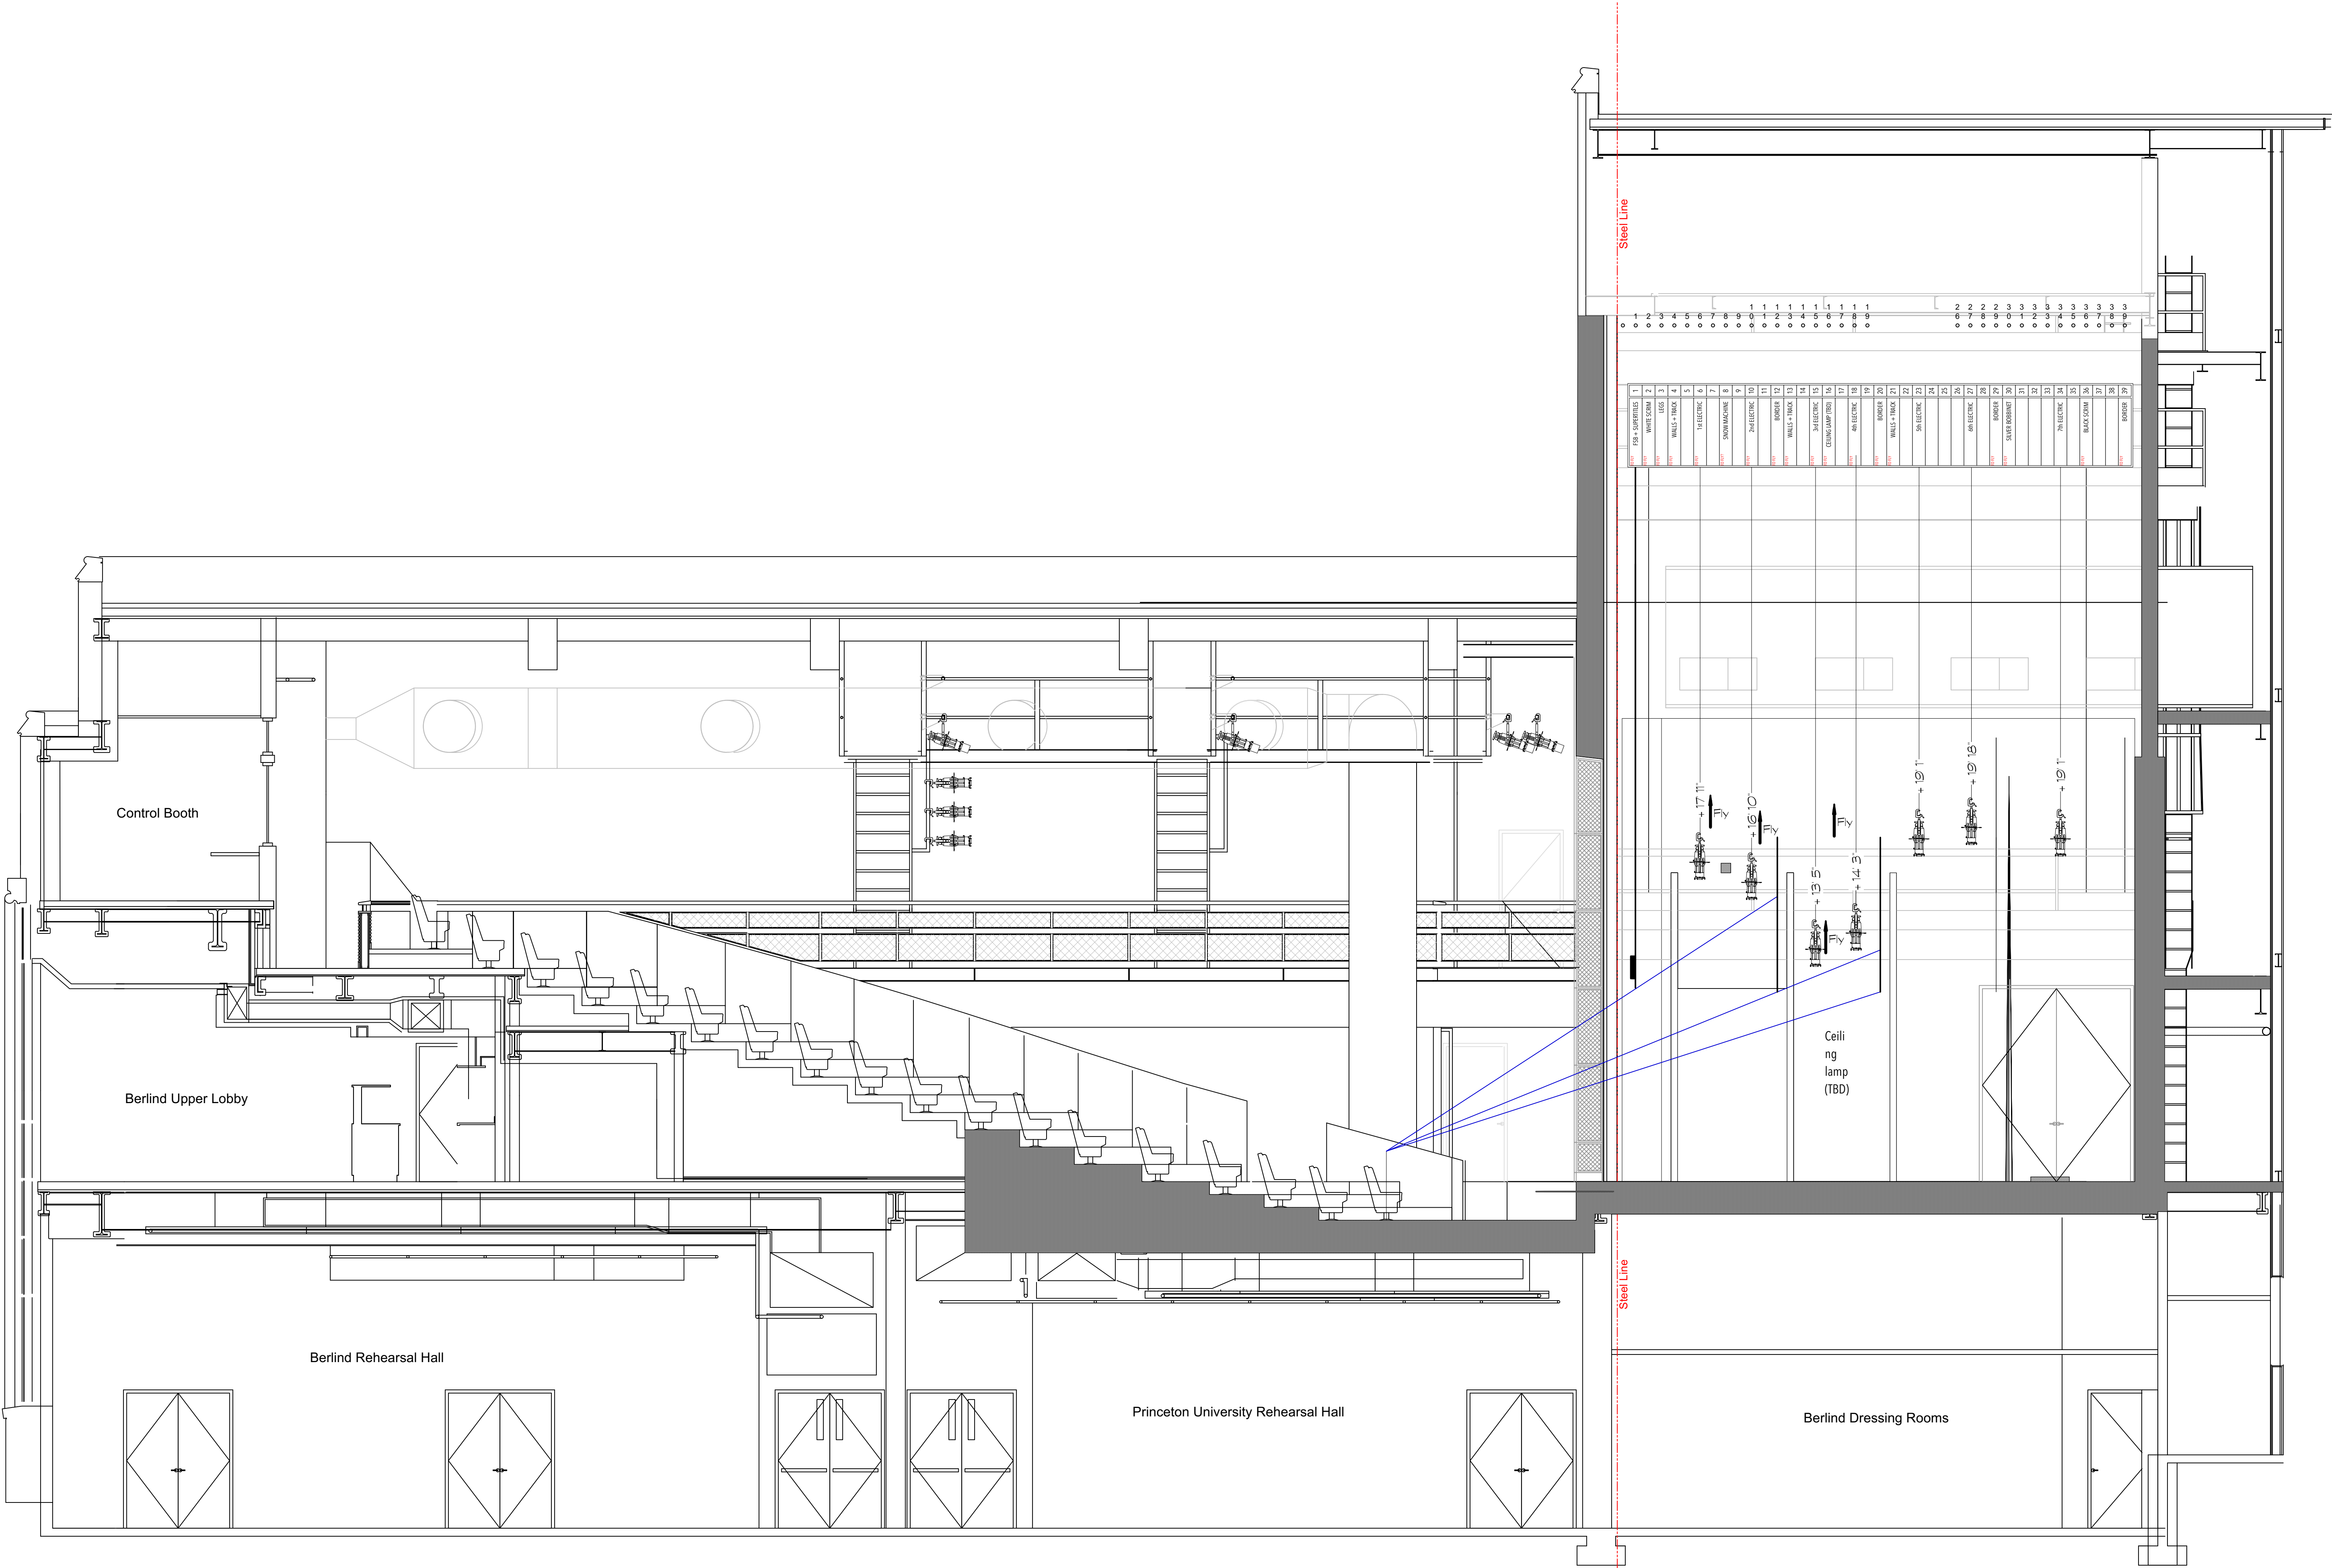


DATE:
3/6/24

DRAWN BY:
Kerstin Fagerstrom
kerstinf@princeton.edu

LIGHTING UNITS:

- ETC LED Series 3 Fresnel
- ETC LED Series 3 Leko 19"
- ETC LED Series 3 Leko 26"
- ETC LED Series 3 Leko 36"
- ETC LED Series 3 Leko 50"
- ETC LED Series 2 Leko 36"
- ETC LED Series 2 Leko 50"
- ETC D60 Vivid
- MAC Encore

TYPICAL UNIT:

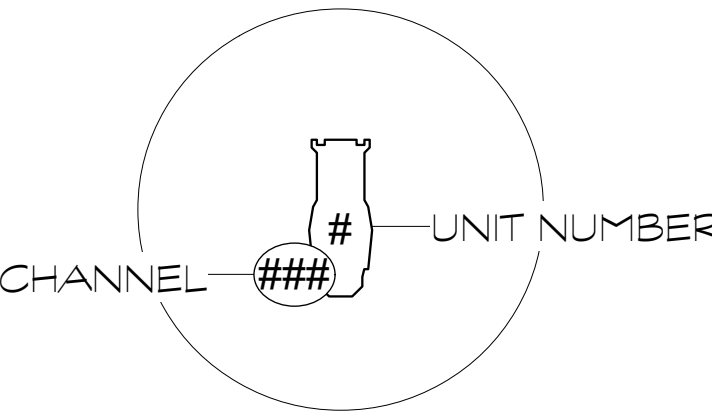

- All units hung on 18" centers unless otherwise specified.
- Written dimensions take precedence over scale measurements.
- Trims are from stage floor to sidearm/pipe.

DRAWING TITLE

Section - 15' Border


PLATE NUMBER:

1.1

SCALE:

1/4" = 1'0"

BERLIND THEATRE
Princeton University
Princeton, NJ

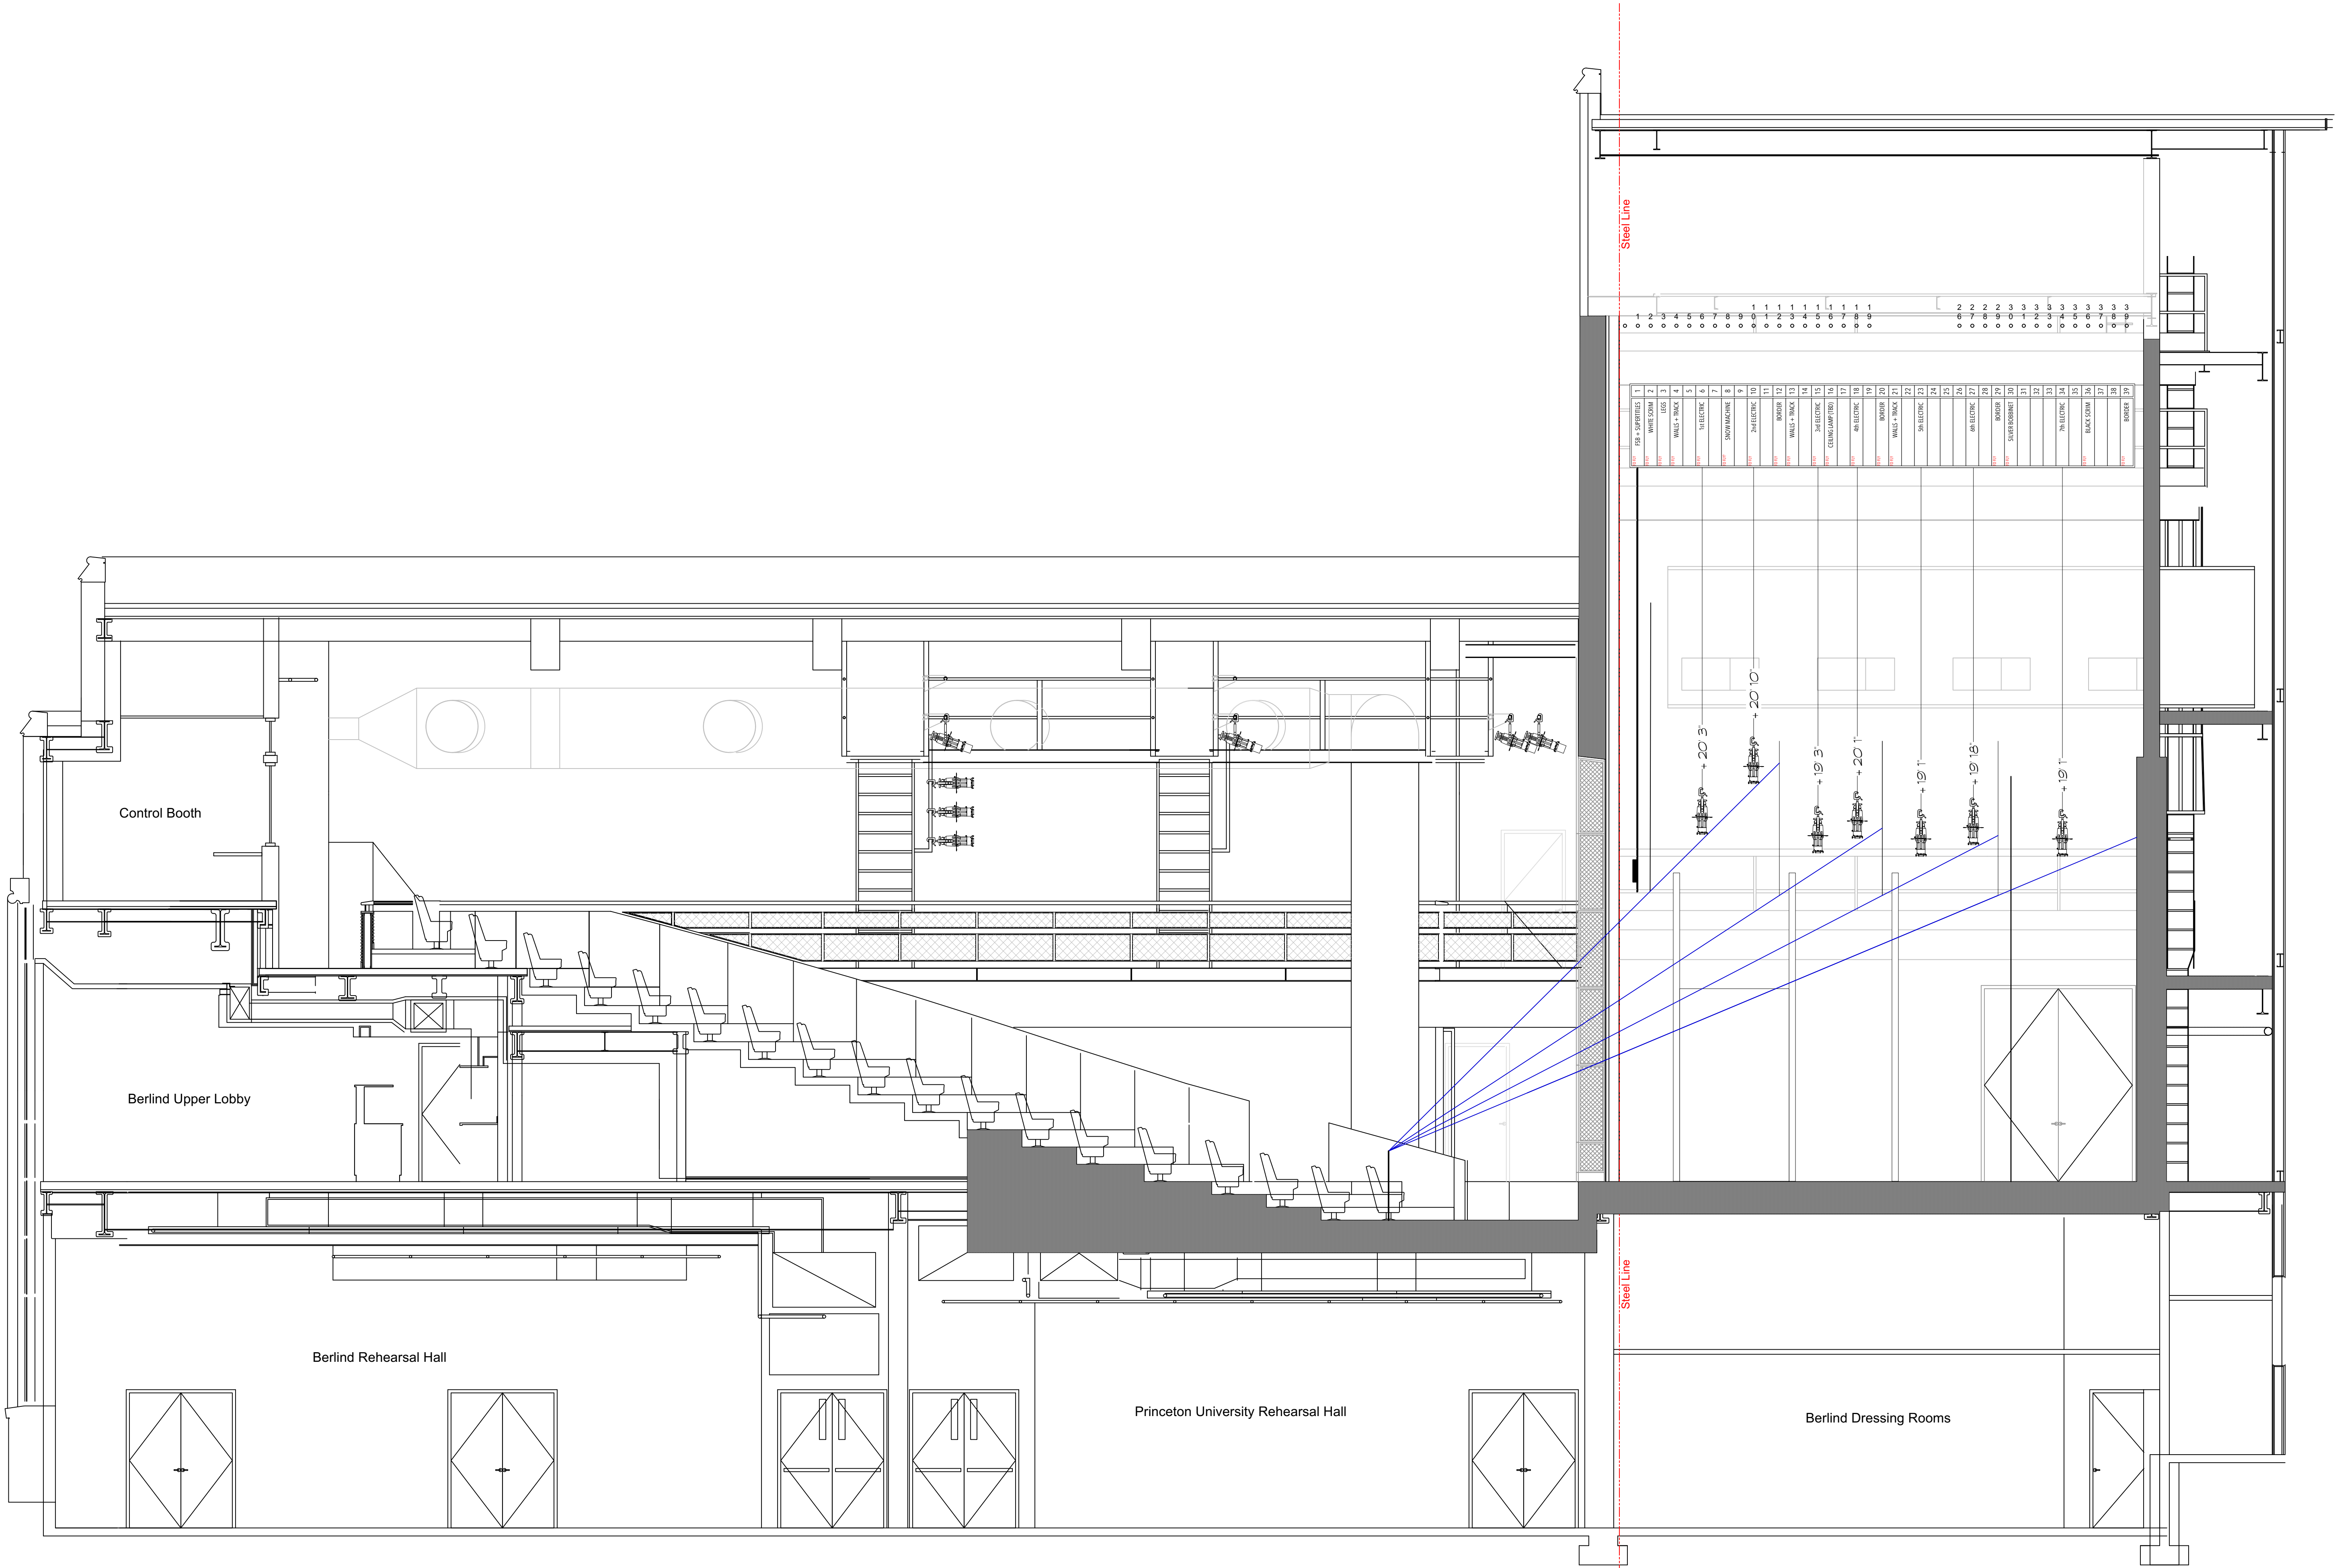

Flight of a Legless Bird


DATE:
3/6/24

DRAWN BY:
Kerstin Fagerstrom
kerstinf@princeton.edu

LIGHTING UNITS:

- ETC LED Series 3 Fresnel
- ETC LED Series 3 Leko 19"
- ETC LED Series 3 Leko 26"
- ETC LED Series 3 Leko 36"
- ETC LED Series 3 Leko 50"
- ETC LED Series 2 Leko 36"
- ETC LED Series 2 Leko 50"
- ETC D60 Vivid
- MAC Encore

TYPICAL UNIT:

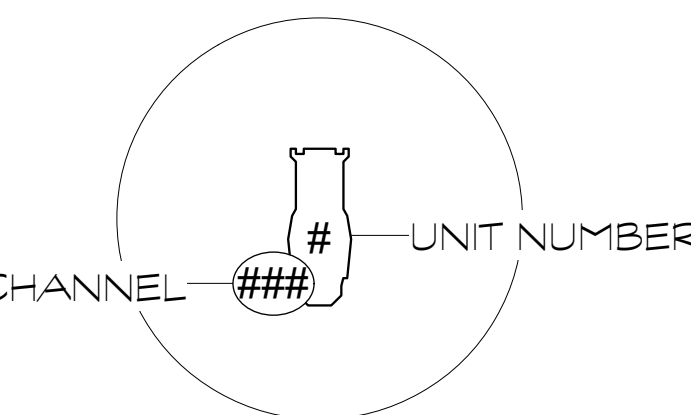

- All units hung on 18" centers unless otherwise specified.
- Written dimensions take precedence over scale measurements.
- Trims are from stage floor to sidearm/pipe.



DRAWING TITLE
Electrics

PLATE NUMBER:
2.0

SCALE:
1/2" = 1'0"

BERLIND THEATRE
Princeton University
Princeton, NJ

39	BORDER	TO FLY
38		
37		
36	BLACK SCRIM	TO FLY
35		
34	7th ELECTRIC	
33		
32		
31		
30	SILVER BOBBINET	TO FLY
29	BORDER	TO FLY
28		
27	6th ELECTRIC	
26		
25		
24		
23	5th ELECTRIC	
22		
21	WALLS + TRACK	TO FLY
20	BORDER	TO FLY
19		
18	4th ELECTRIC	TO FLY
17		
16	CEILING LAMP (TBD)	TO FLY
15	3rd ELECTRIC	TO FLY
14		
13	WALLS + TRACK	TO FLY
12	BORDER	TO FLY
11		
10	2nd ELECTRIC	TO FLY
9		
8	SNOW MACHINE	TO FLY
7		
6	1st ELECTRIC	TO FLY
5		
4	WALLS + TRACK	TO FLY
3	LEGS	TO FLY
2	WHITE SCRIM	TO FLY
1	FSB + SUPERTITLES	TO FLY

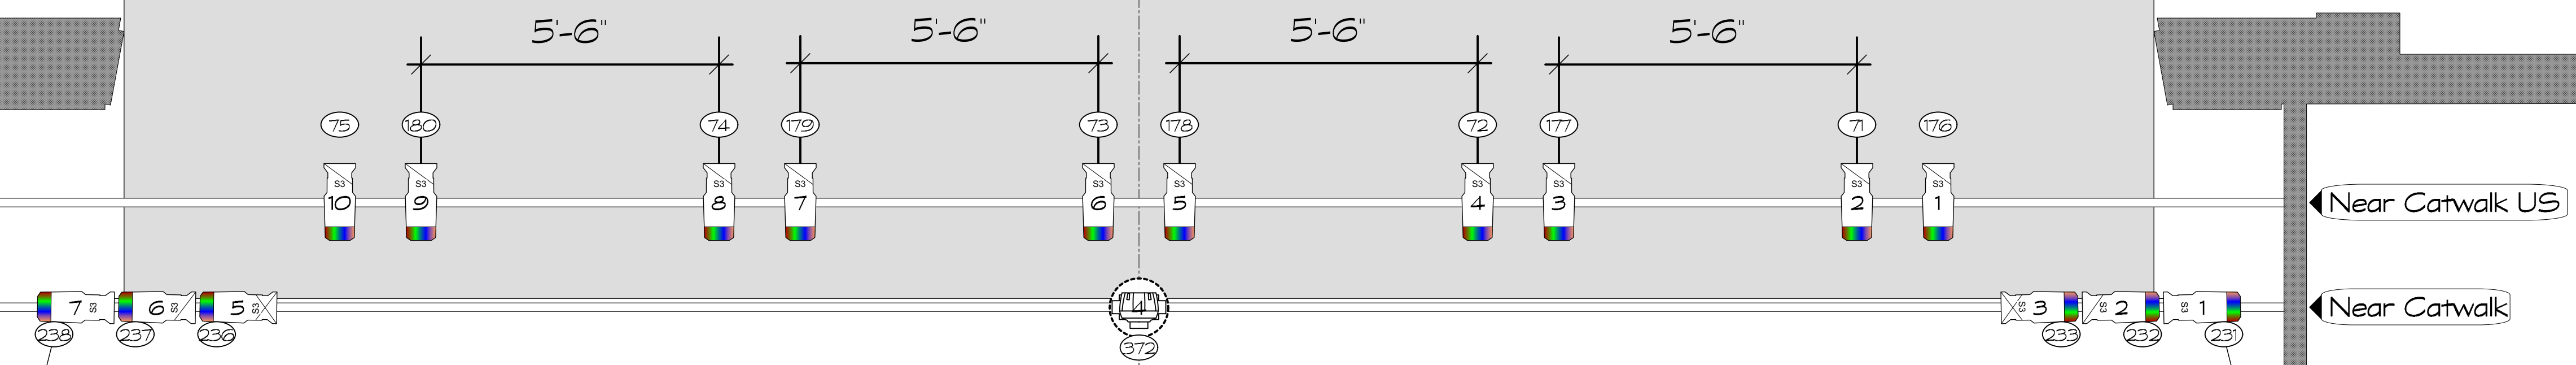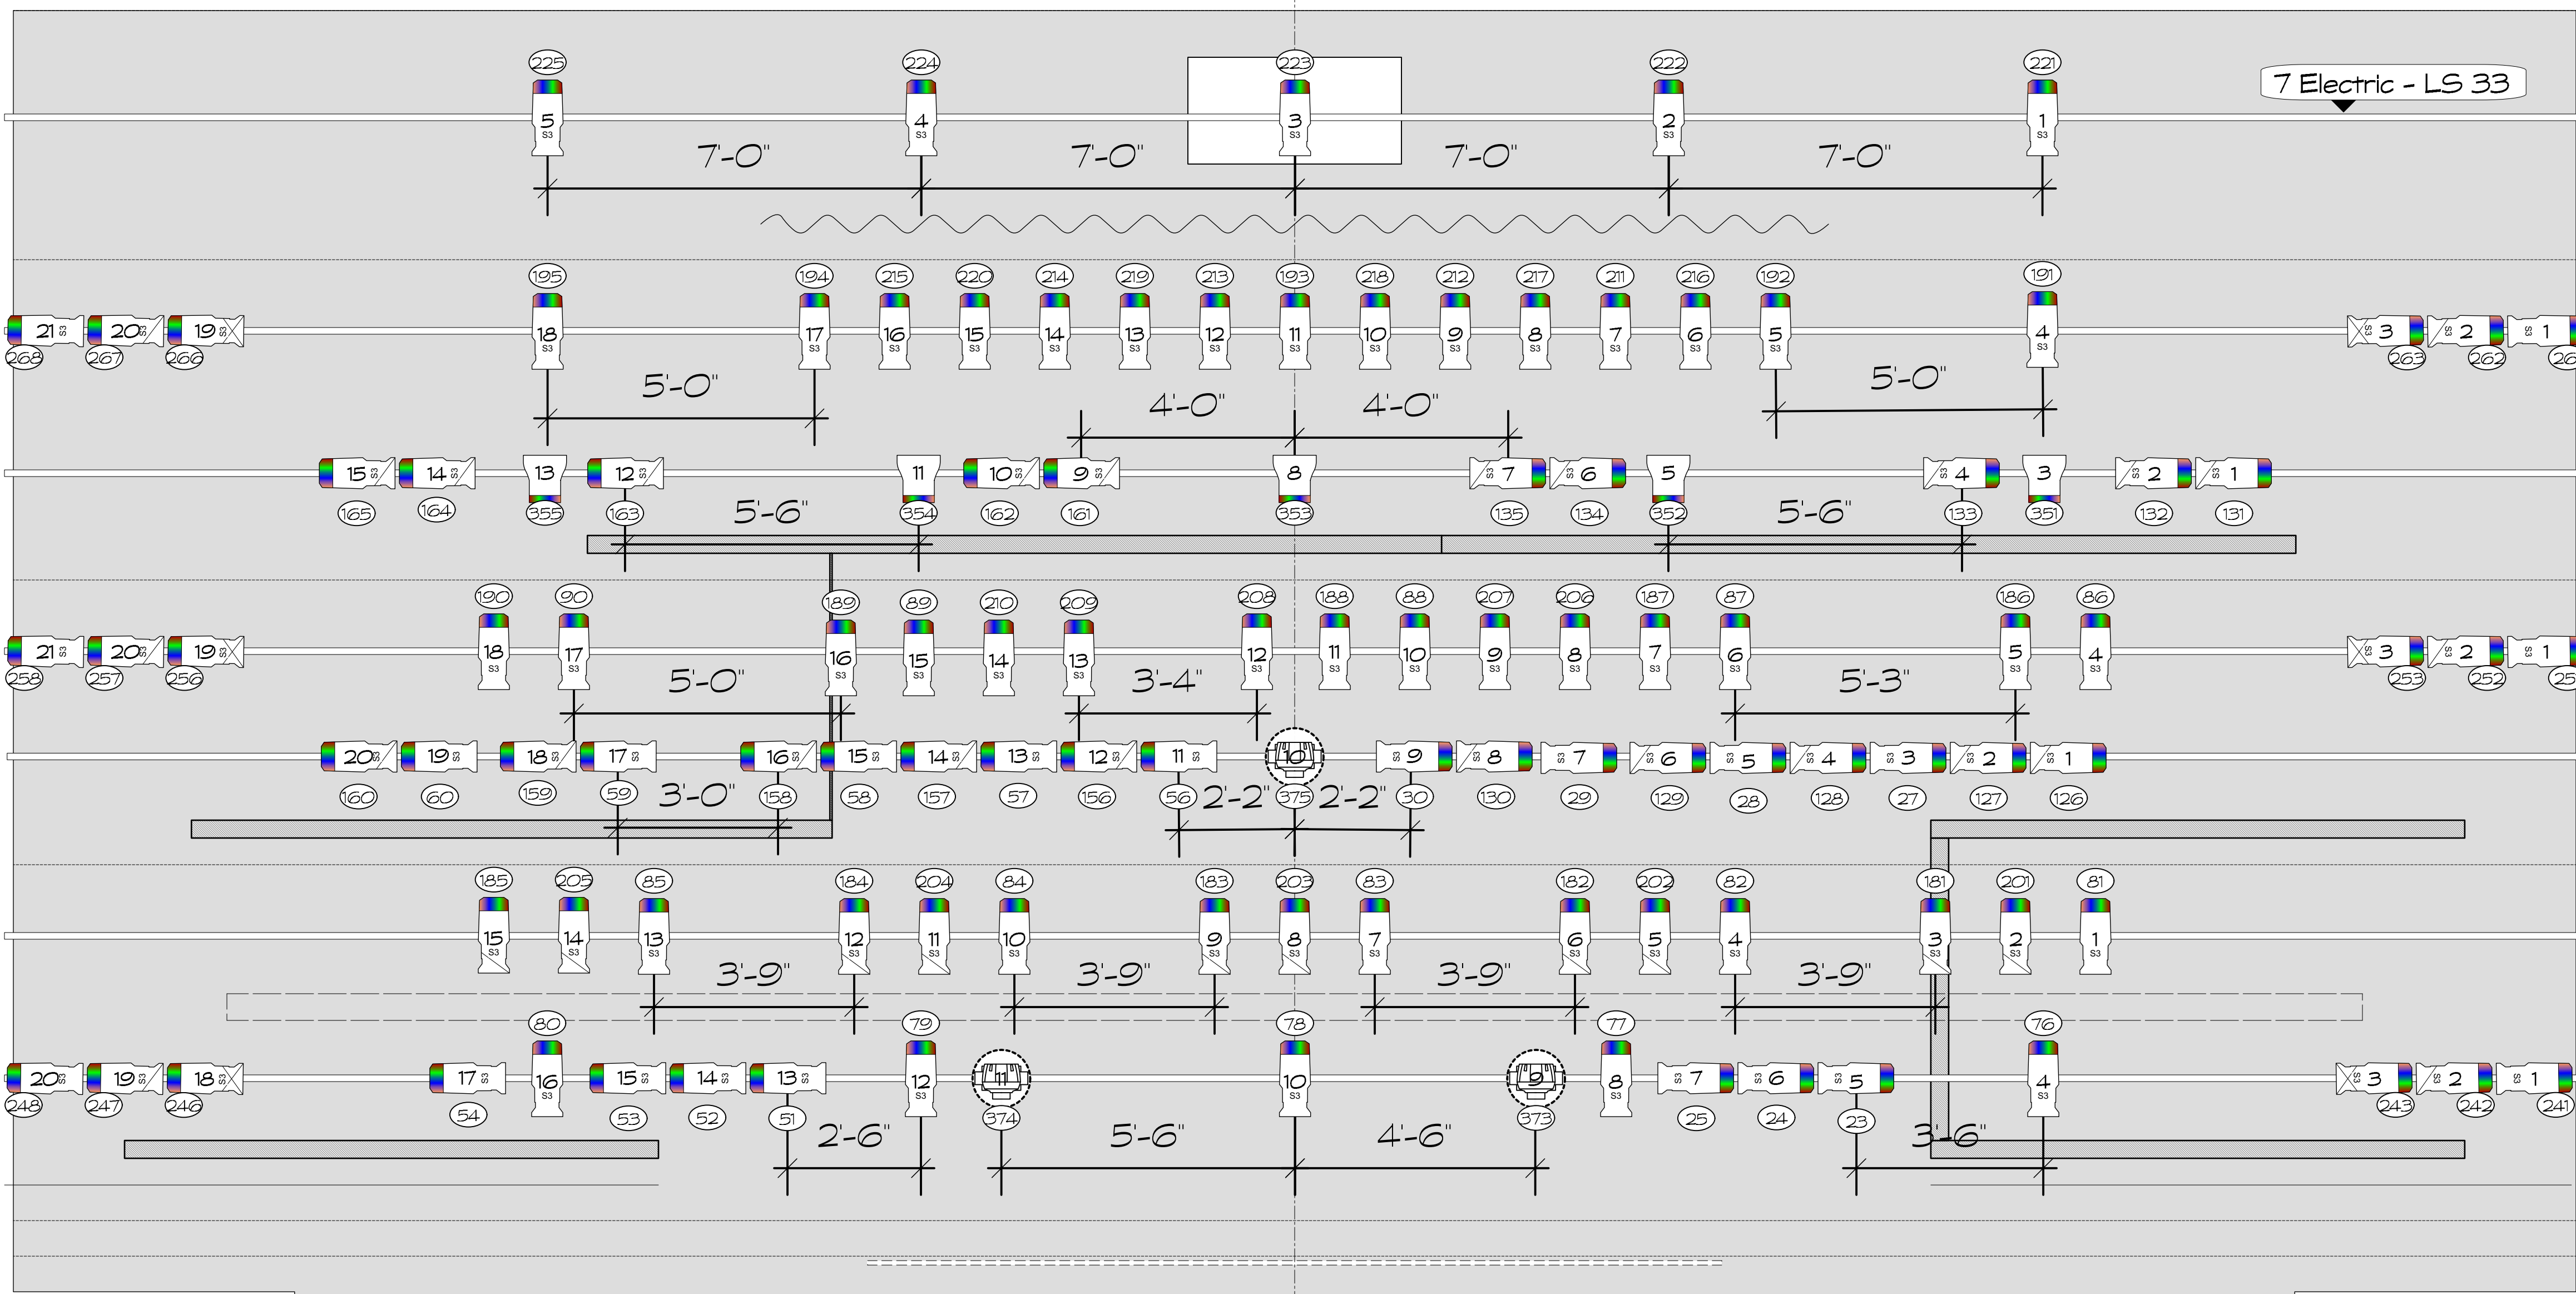


Flight of a
Legless Bird

DATE:
3/6/24

DRAWN BY:
Kerstin Fagerstrom
kerstinf@princeton.edu

- LIGHTING UNITS:
- ETC LED Series 3 Fresnel
 - ETC LED Series 3 Leko 19"
 - ETC LED Series 3 Leko 26"
 - ETC LED Series 3 Leko 36"
 - ETC LED Series 3 Leko 50"
 - ETC LED Series 2 Leko 36"
 - ETC LED Series 2 Leko 50"
 - ETC D60 Vivid
 - MAC Encore

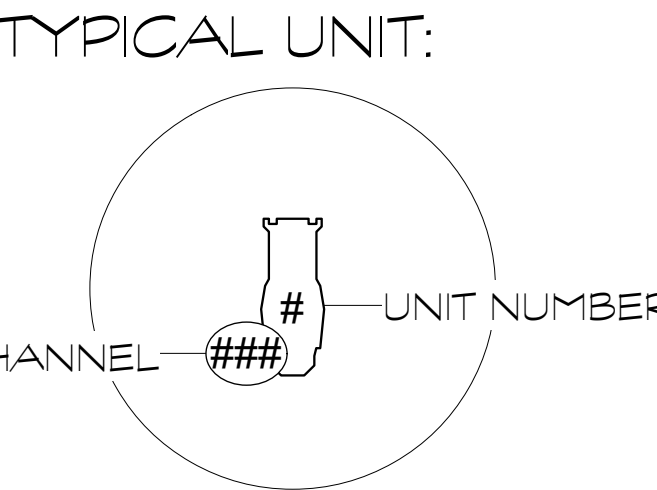

- All units hung on 18" centers unless otherwise specified.
- Written dimensions take precedence over scale measurements.
- Trims are from stage floor to sidearm/pipe.


DRAWING TITLE
Ground Units

PLATE NUMBER:
2.1

SCALE:
1/2" = 1'0"

BERLIND THEATRE
Princeton University
Princeton, NJ





39	BORDER	TO FLY
38		
37		
36	BLACK SCRIM	TO FLY
35		
34	7th ELECTRIC	
33		
32		
31		
30	SILVER BOBBINET	TO FLY
29	BORDER	TO FLY
28		
27	6th ELECTRIC	
26		
25		
24		
23	5th ELECTRIC	
22		
21	WALLS + TRACK	TO FLY
20	BORDER	TO FLY
19		
18	4th ELECTRIC	TO FLY
17		
16	CEILING LAMP (TBD)	TO FLY
15	3rd ELECTRIC	TO FLY
14		
13	WALLS + TRACK	TO FLY
12	BORDER	TO FLY
11		
10	2nd ELECTRIC	TO FLY
9		
8	SNOW MACHINE	TO FLY?
7		
6	1st ELECTRIC	TO FLY
5		
4	WALLS + TRACK	TO FLY
3	LEGS	TO FLY
2	WHITE SCRIM	TO FLY
1	FSB + SUPERTITLES	TO FLY

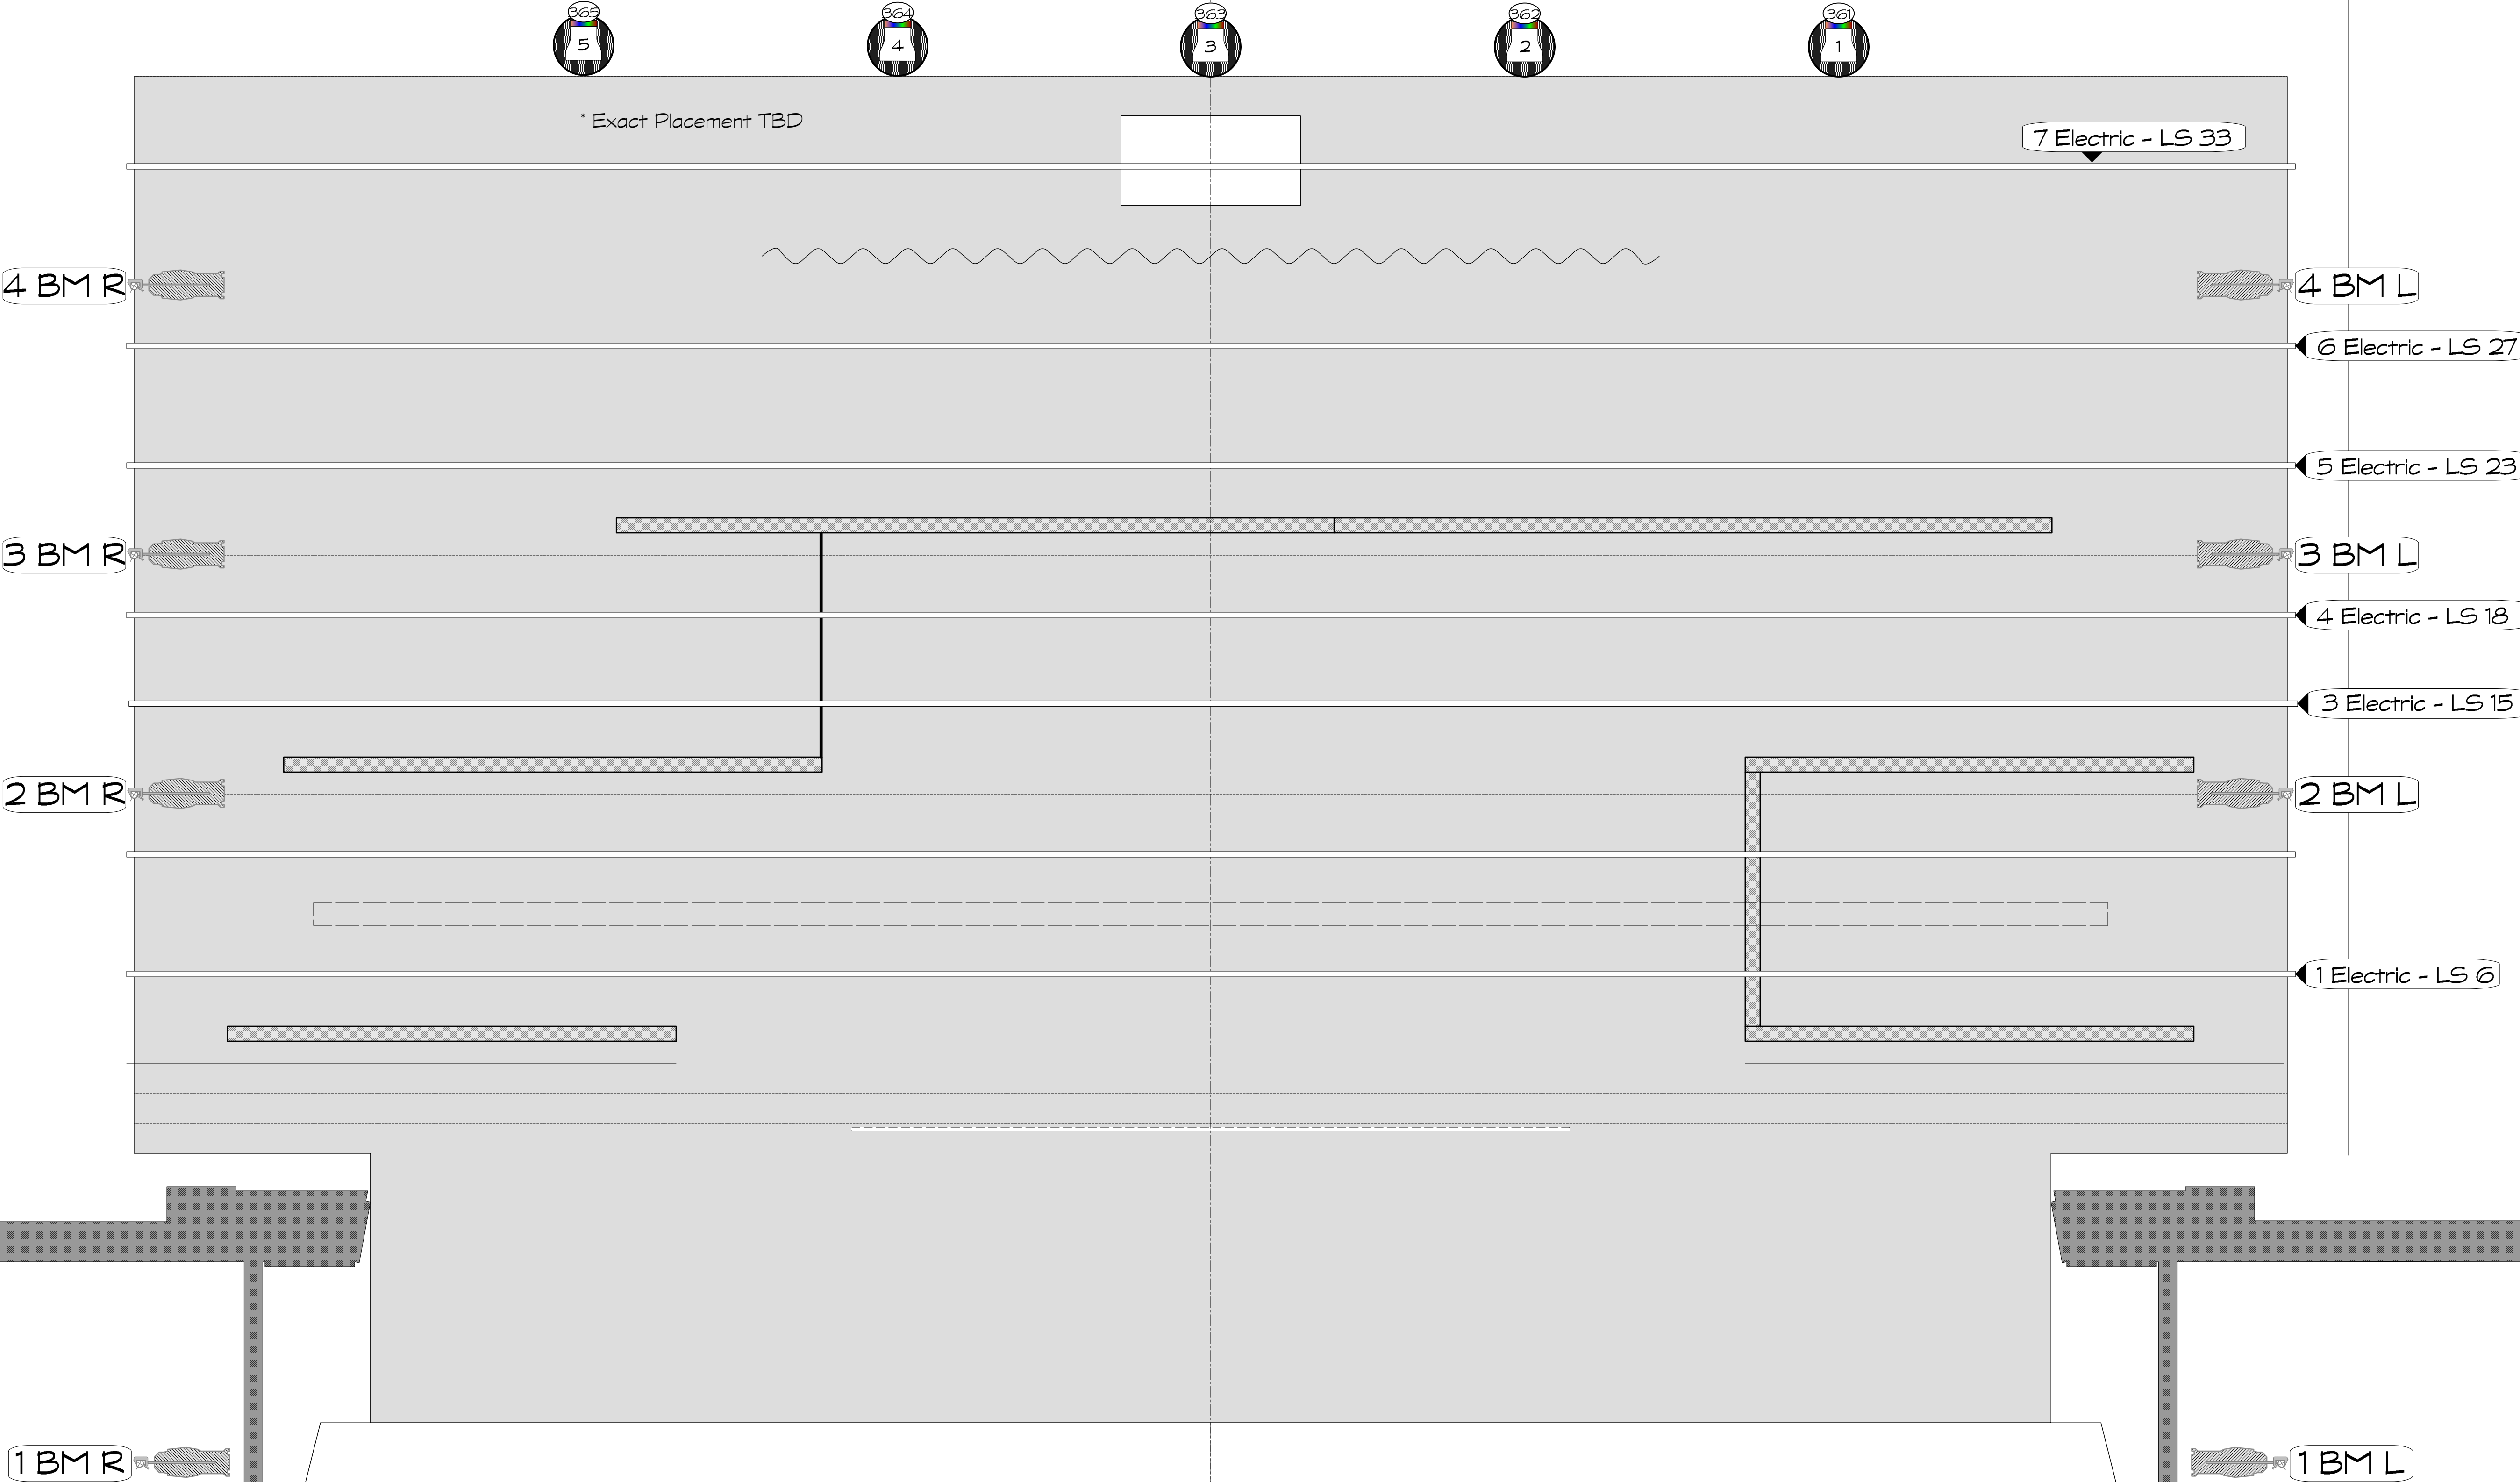


DATE:
3/6/24

DRAWN BY:
Kerstin Fagerstrom
kerstinf@princeton.edu

LIGHTING UNITS:

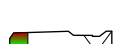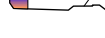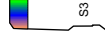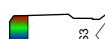- | | |
|---|---------------------------|
|  | ETC LED Series 3 Fresnel |
|  | ETC LED Series 3 Leko 19' |
|  | ETC LED Series 3 Leko 26' |
|  | ETC LED Series 3 Leko 36' |
|  | ETC LED Series 3 Leko 50' |
|  | ETC LED Series 2 Leko 36' |
|  | ETC LED Series 2 Leko 50' |
|  | ETC D60 Vivid |
|  | MAC Encore |

TYPICAL UNIT:

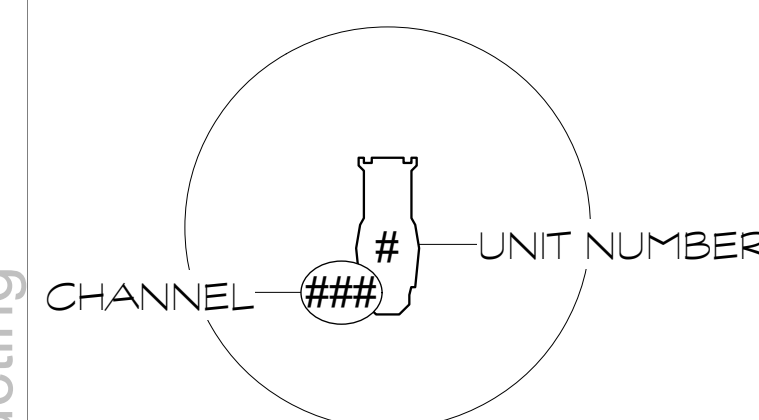

- All units hung on 18" centers unless otherwise specified.
- Written dimensions take precedence over scale measurements.
- Trims are from stage floor to sidearm/pipe.

DRAWING TITLE


Catwalks

PLATE NUMBER:

2.2

SCALE:
1/2" = 1'0"

BERLIND THEATRE
Princeton University
Princeton, NJ

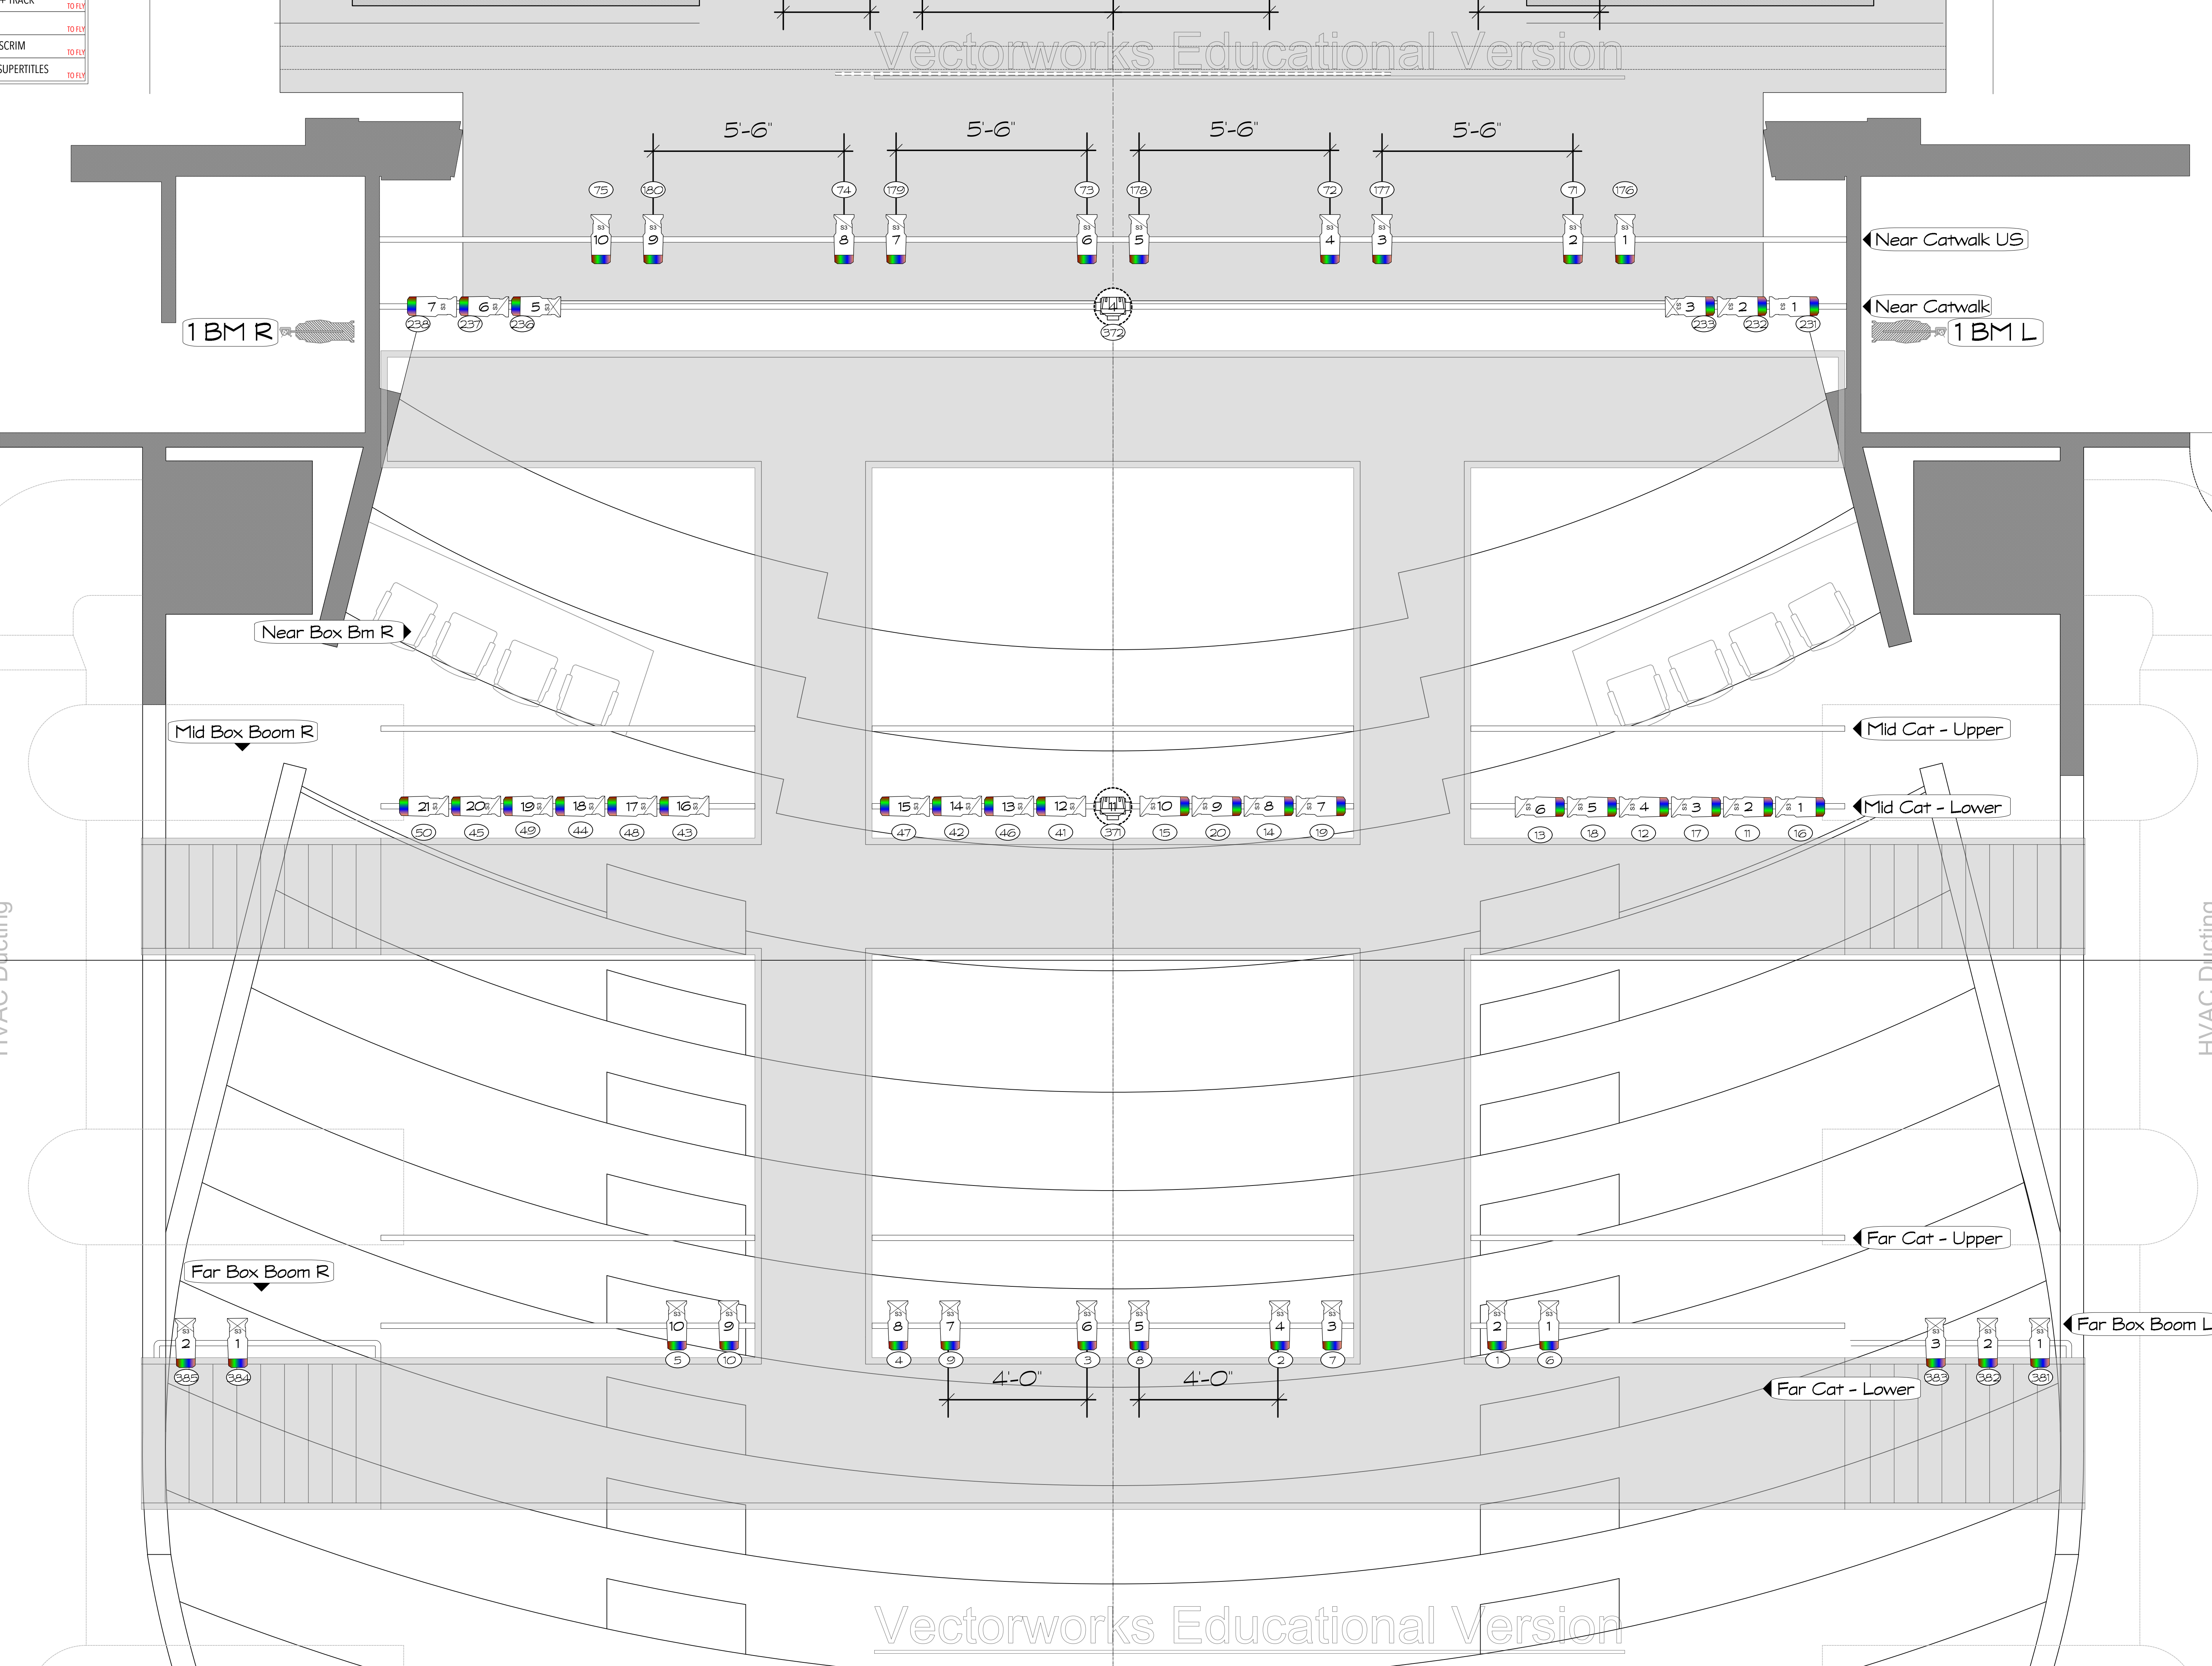

Flight of a
Legless Bird


DATE:
3/6/24

DRAWN BY:
Kerstin Fagerstrom
kerstinf@princeton.edu

LIGHTING UNITS:

- ETC LED Series 3 Fresnel
- ETC LED Series 3 Leko 19'
- ETC LED Series 3 Leko 26'
- ETC LED Series 3 Leko 36'
- ETC LED Series 3 Leko 50'
- ETC LED Series 2 Leko 36'
- ETC LED Series 2 Leko 50'
- ETC D60 Vivid
- MAC Encore

TYPICAL UNIT:

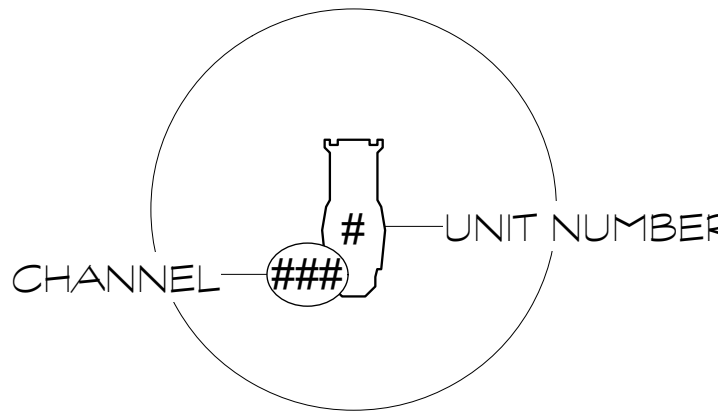

- All units hung on 18" centers unless otherwise specified.
- Written dimensions take precedence over scale measurements.
- Trims are from stage floor to sidearm/pipe.

DRAWING TITLE
Booms

PLATE NUMBER:
3.0

SCALE:
1/2" = 1'0"

BERLIND THEATRE
Princeton University
Princeton, NJ

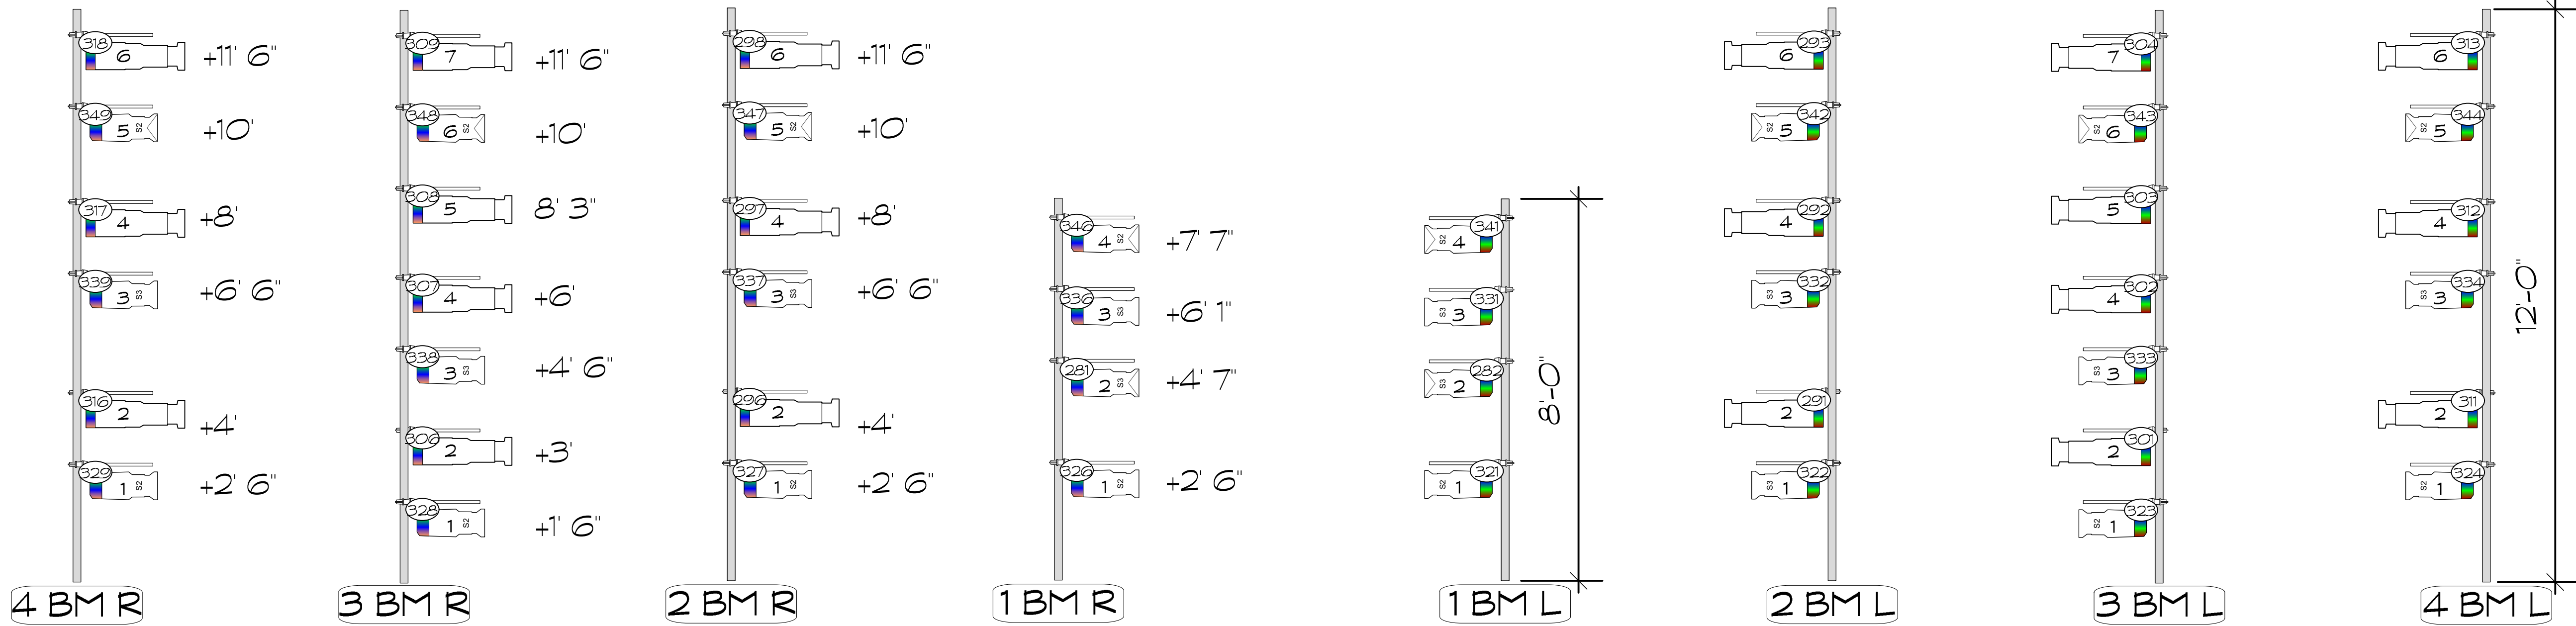


TABLE OF CONTENTS

Boom SR 4	1	Mid Cat	7
Near Cat	1	Boom SR 3	8
2nd E	2	Ground US	8
Boom SL 1	2	5th E	9
Boom SL 4	3	Boom SR 2	9
Boom SL 3	3	Far Cat	10
Boom SL 2	3	7th E	10
3rd E	4	4th E	11
Near Cat US	5	1st E	12
Boom SR 1	5	Far Box Boom R	12
6th E	6	Far Box Boom L	13

Boom SR 4

U#	Purpose	Instrument Type & Accessory	Load	Color & Gobo	Chan	Ad	Dm
1	SR Shin	S4 Lustr2 36°	171w	NC	(329)		
2	SR Curtain	S4 Lustr3Fresnel	171w	NC	(316)		
3	SR Mid	S4 Lustr3 36°	171w	NC	(339)		
4	SR Curtain	S4 Lustr3Fresnel	171w	NC	(317)		
5	SR Heads	S4 Lustr2 50°	171w	NC	(349)		
6	SR Curtain	S4 Lustr3Fresnel	171w	NC	(318)		

Near Cat

U#	Purpose	Instrument Type & Accessory	Load	Color & Gobo	Chan	Ad	Dm
1	Pipe Sides SL A	S4 Lustr3 36°	171w	NC	(231)		
2	Pipe Sides SL B	S4 Lustr3 26°	171w	NC	(232)		
3	Pipe Sides SL C	S4 Lustr3 19°	171w	NC	(233)		
4	ML	Martin Mac Aura	260w	NC	(372)		
5	Pipe Sides SR C	S4 Lustr3 19°	171w	NC	(236)		
6	Pipe Sides SR D	S4 Lustr3 26°	171w	NC	(237)		
7	Pipe Sides SR E	S4 Lustr3 36°	171w	NC	(238)		

2nd E

U#	Purpose	Instrument Type & Accessory	Load	Color & Gobo	Chan	Ad	Dm
1	Down 10' K	S4 Lustr3 36°	171w	NC	(81)		
2	Back 15' A	S4 Lustr3 26°	171w	NC	(201)		
3	Down 15' K	S4 Lustr3 26°	171w	NC	(181)		
4	Down 10' L	S4 Lustr3 36°	171w	NC	(82)		
5	Back 15' B	S4 Lustr3 26°	171w	NC	(202)		
6	Down 15' L	S4 Lustr3 26°	171w	NC	(182)		
7	Down 10' M	S4 Lustr3 36°	171w	NC	(83)		
8	Back 15' C	S4 Lustr3 26°	171w	NC	(203)		
9	Down 15' M	S4 Lustr3 26°	171w	NC	(183)		
10	Down 10' N	S4 Lustr3 36°	171w	NC	(84)		
11	Back 15' D	S4 Lustr3 26°	171w	NC	(204)		
12	Down 15' N	S4 Lustr3 26°	171w	NC	(184)		
13	Down 10' O	S4 Lustr3 36°	171w	NC	(85)		
14	Back 15' E	S4 Lustr3 26°	171w	NC	(205)		
15	Down 15' O	S4 Lustr3 26°	171w	NC	(185)		

Boom SL 1

U#	Purpose	Instrument Type & Accessory	Load	Color & Gobo	Chan	Ad	Dm
1	SL Shins	S4 Lustr2 36°	171w	NC	(321)		
2	SL Walls - Wall A	S4 Lustr3Fresnel	171w	NC	(282)		
3	SL Mids	S4 Lustr3 36°	171w	NC	(331)		
4	SL Heads	S4 Lustr2 50°	171w	NC	(341)		

Boom SL 4

U#	Purpose	Instrument Type & Accessory	Load	Color & Gobo	Chan	Ad	Dm
1	SL Shins	S4 Lustr2 36°	171w	NC	(324)		
2	SL Curtain	S4 Lustr3Fresnel	171w	NC	(311)		
3	SL Mids	S4 Lustr3 36°	171w	NC	(334)		
4	SL Curtain	S4 Lustr3Fresnel	171w	NC	(312)		
5	SL Heads	S4 Lustr2 50°	171w	NC	(344)		
6	SL Curtain	S4 Lustr3Fresnel	171w	NC	(313)		

Boom SL 3

U#	Purpose	Instrument Type & Accessory	Load	Color & Gobo	Chan	Ad	Dm
1	SL Shins	S4 Lustr2 36°	171w	NC	(323)		
2	SL Walls CD	S4 Lustr3Fresnel	171w	NC	(301)		
3	SL Mids	S4 Lustr3 36°	171w	NC	(333)		
4	SL Walls CD	S4 Lustr3Fresnel	171w	NC	(302)		
5	SL Walls CD	S4 Lustr3Fresnel	171w	NC	(303)		
6	SL Heads	S4 Lustr2 50°	171w	NC	(343)		
7	SL Walls CD	S4 Lustr3Fresnel	171w	NC	(304)		

Boom SL 2

U#	Purpose	Instrument Type & Accessory	Load	Color & Gobo	Chan	Ad	Dm
1	SL Shins	S4 Lustr3 36°	171w	NC	(322)		
2	SL Walls B	S4 Lustr3Fresnel	171w	NC	(291)		
3	SL Mids	S4 Lustr3 36°	171w	NC	(332)		
4	SL Walls B	S4 Lustr3Fresnel	171w	NC	(292)		
5	SL Heads	S4 Lustr2 50°	171w	NC	(342)		
6	SL Walls B	S4 Lustr3Fresnel	171w	NC	(293)		

3rd E

U#	Purpose	Instrument Type & Accessory	Load	Color & Gobo	Chan	Ad	Dm
1	F/S 15' SL P	S4 Lustr3 26°	171w	NC	(126)		
2	F/S 15' SL Q	S4 Lustr3 26°	171w	NC	(127)		
3	F/S 10' SL Q	S4 Lustr3 50°	171w	NC	(27)		
4	F/S 15' SL R	S4 Lustr3 26°	171w	NC	(128)		
5	F/S 10' SL R	S4 Lustr3 50°	171w	NC	(28)		
6	F/S 15' SL S	S4 Lustr3 26°	171w	NC	(129)		
7	F/S 10' SL S	S4 Lustr3 50°	171w	NC	(29)		
8	F/S 15' SL T	S4 Lustr3 26°	171w	NC	(130)		
9	F/S 10' SL T	S4 Lustr3 50°	171w	NC	(30)		
10	ML	Martin Mac Aura	260w	NC	(375)		
11	F/S 10' SR P	S4 Lustr3 50°	171w	NC	(56)		
12	F/S 15' SR P	S4 Lustr3 26°	171w	NC	(156)		
13	F/S 10' SR Q	S4 Lustr3 50°	171w	NC	(57)		
14	F/S 15' SR Q	S4 Lustr3 26°	171w	NC	(157)		
15	F/S 10' SR R	S4 Lustr3 50°	171w	NC	(58)		
16	F/S 15' SR R	S4 Lustr3 26°	171w	NC	(158)		
17	F/S 10' SR S	S4 Lustr3 50°	171w	NC	(59)		
18	F/S 15' SR S	S4 Lustr3 26°	171w	NC	(159)		
19	F/S 10' SR T	S4 Lustr3 50°	171w	NC	(60)		
20	F/S 15' SR T	S4 Lustr3 26°	171w	NC	(160)		

Near Cat US

U#	Purpose	Instrument Type & Accessory	Load	Color & Gobo	Chan	Ad	Dm
1	Down 15' F	S4 Lustr3 26°	171w	NC	(176)		
2	Down A	S4 Lustr3 26°	171w	NC	(71)		
3	Down 15' G	S4 Lustr3 26°	171w	NC	(177)		
4	Down B	S4 Lustr3 26°	171w	NC	(72)		
5	Down 15' H	S4 Lustr3 26°	171w	NC	(178)		
6	Down C	S4 Lustr3 26°	171w	NC	(73)		
7	Down 15' I	S4 Lustr3 26°	171w	NC	(179)		
8	Down D	S4 Lustr3 26°	171w	NC	(74)		
9	Down 15' J	S4 Lustr3 26°	171w	NC	(180)		
10	Down E	S4 Lustr3 26°	171w	NC	(75)		

Boom SR 1

U#	Purpose	Instrument Type & Accessory	Load	Color & Gobo	Chan	Ad	Dm
1	SR Shin	S4 Lustr2 36°	171w	NC	(326)		
2	SR Walls - Wall G	S4 Lustr3 50°	171w	NC	(281)		
3	SR Mid	S4 Lustr3 36°	171w	NC	(336)		
4	SR Heads	S4 Lustr2 50°	171w	NC	(346)		

6th E

U#	Purpose	Instrument Type & Accessory	Load	Color & Gobo	Chan	Ad	Dm
1	Pipe Sides SL U	S4 Lustr3 36°	171w	NC	(261)		
2	Pipe Sides SL V	S4 Lustr3 26°	171w	NC	(262)		
3	Pipe Sides SL W	S4 Lustr3 19°	171w	NC	(263)		
4	Back 15' U	S4 Lustr3 36°	171w	NC	(191)		
5	Back 15' V	S4 Lustr3 36°	171w	NC	(192)		
6	Back 15' P	S4 Lustr3 36°	171w	NC	(216)		
7	Back 15' K	S4 Lustr3 36°	171w	NC	(211)		
8	Back 15' Q	S4 Lustr3 36°	171w	NC	(217)		
9	Back 15' L	S4 Lustr3 36°	171w	NC	(212)		
10	Back 15' R	S4 Lustr3 36°	171w	NC	(218)		
11	Back 15' W	S4 Lustr3 36°	171w	NC	(193)		
12	Back 15' M	S4 Lustr3 36°	171w	NC	(213)		
13	Back 15' S	S4 Lustr3 36°	171w	NC	(219)		
14	Back 15' N	S4 Lustr3 36°	171w	NC	(214)		
15	Back 15' T	S4 Lustr3 36°	171w	NC	(220)		
16	Back 15' O	S4 Lustr3 36°	171w	NC	(215)		
17	Back 15' X	S4 Lustr3 36°	171w	NC	(194)		
18	Back 15' Y	S4 Lustr3 36°	171w	NC	(195)		
19	Pipe Sides SR U	S4 Lustr3 19°	171w	NC	(266)		
20	Pipe Sides SR X	S4 Lustr3 26°	171w	NC	(267)		
21	Pipe Sides SR Y	S4 Lustr3 36°	171w	NC	(268)		

Mid Cat

U#	Purpose	Instrument Type & Accessory	Load	Color & Gobo	Chan	Ad	Dm
1	F/S SL F	S4 Lustr3 26°	171w	NC	(16)		
2	F/S SL A	S4 Lustr3 26°	171w	NC	(11)		
3	F/S SL G	S4 Lustr3 26°	171w	NC	(17)		
4	F/S SL B	S4 Lustr3 26°	171w	NC	(12)		
5	F/S SL H	S4 Lustr3 26°	171w	NC	(18)		
6	F/S SL C	S4 Lustr3 26°	171w	NC	(13)		
7	F/S SL I	S4 Lustr3 26°	171w	NC	(19)		
8	F/S SL D	S4 Lustr3 26°	171w	NC	(14)		
9	F/S SL J	S4 Lustr3 26°	171w	NC	(20)		
10	F/S SL E	S4 Lustr3 26°	171w	NC	(15)		
11	ML	Martin Mac Aura	260w	NC	(371)		
12	F/S SR A	S4 Lustr3 26°	171w	NC	(41)		
13	F/S SR F	S4 Lustr3 26°	171w	NC	(46)		
14	F/S SR B	S4 Lustr3 26°	171w	NC	(42)		
15	F/S SR G	S4 Lustr3 26°	171w	NC	(47)		
16	F/S SR C	S4 Lustr3 26°	171w	NC	(43)		
17	F/S SR H	S4 Lustr3 26°	171w	NC	(48)		
18	F/S SR D	S4 Lustr3 26°	171w	NC	(44)		
19	F/S SR I	S4 Lustr3 26°	171w	NC	(49)		
20	F/S SR E	S4 Lustr3 26°	171w	NC	(45)		
21	F/S SR J	S4 Lustr3 26°	171w	NC	(50)		

Boom SR 3

U#	Purpose	Instrument Type & Accessory	Load	Color & Gobo	Chan	Ad	Dm
1	SR Shin	S4 Lustr2 36°	171w	NC	(328)		
2	SR Walls CD	S4 Lustr3Fresnel	171w	NC	(306)		
3	SR Mid	S4 Lustr3 36°	171w	NC	(338)		
4	SR Walls CD	S4 Lustr3Fresnel	171w	NC	(307)		
5	SR Walls CD	S4 Lustr3Fresnel	171w	NC	(308)		
6	SR Heads	S4 Lustr2 50°	171w	NC	(348)		
7	SR Walls CD	S4 Lustr3Fresnel	171w	NC	(309)		

Ground US

U#	Purpose	Instrument Type & Accessory	Load	Color & Gobo	Chan	Ad	Dm
1	Ground Light	ETC D60 Lustr SELO3070	161w	NC	(361)		
2	Ground Light	ETC D60 Lustr SELO3070	161w	NC	(362)		
3	Ground Light	ETC D60 Lustr SELO3070	161w	NC	(363)		
4	Ground Light	ETC D60 Lustr SELO3070	161w	NC	(364)		
5	Ground Light	ETC D60 Lustr SELO3070	161w	NC	(365)		

5th E

U#	Purpose	Instrument Type & Accessory	Load	Color & Gobo	Chan	Ad	Dm
1	F/S 15' SL U	S4 Lustr3 26°	171w	NC	(131)		
2	F/S 15' SL V	S4 Lustr3 26°	171w	NC	(132)		
3	Curtain Light	ETC D60 Lustr SELO3070	161w	NC	(351)		
4	F/S 15' SL W	S4 Lustr3 26°	171w	NC	(133)		
5	Curtain Light	ETC D60 Lustr SELO3070	161w	NC	(352)		
6	F/S 15' SL X	S4 Lustr3 26°	171w	NC	(134)		
7	F/S 15' SL Y	S4 Lustr3 26°	171w	NC	(135)		
8	Curtain Light	ETC D60 Lustr SELO3070	161w	NC	(353)		
9	F/S 15' SR U	S4 Lustr3 26°	171w	NC	(161)		
10	F/S 15' SR V	S4 Lustr3 26°	171w	NC	(162)		
11	Curtain Light	ETC D60 Lustr SELO3070	161w	NC	(354)		
12	F/S 15' SR W	S4 Lustr3 26°	171w	NC	(163)		
13	Curtain Light	ETC D60 Lustr SELO3070	161w	NC	(355)		
14	F/S 15' SR X	S4 Lustr3 26°	171w	NC	(164)		
15	F/S 15' SR Y	S4 Lustr3 26°	171w	NC	(165)		

Boom SR 2

U#	Purpose	Instrument Type & Accessory	Load	Color & Gobo	Chan	Ad	Dm
1	SR Shin	S4 Lustr2 36°	171w	NC	(327)		
2	SR Walls E	S4 Lustr3Fresnel	171w	NC	(296)		
3	SR Mid	S4 Lustr3 36°	171w	NC	(337)		
4	SR Walls E	S4 Lustr3Fresnel	171w	NC	(297)		
5	SR Heads	S4 Lustr2 50°	171w	NC	(347)		
6	SR Walls E	S4 Lustr3Fresnel	171w	NC	(298)		

Far Cat

U#	Purpose	Instrument Type & Accessory	Load	Color & Gobo	Chan	Ad	Dm
1	Front Lights F	S4 Lustr3 19°	171w	NC	(6)		
2	Front Lights A	S4 Lustr3 19°	171w	NC	(1)		
3	Front Lights G	S4 Lustr3 19°	171w	NC	(7)		
4	Front Lights B	S4 Lustr3 19°	171w	NC	(2)		
5	Front Lights H	S4 Lustr3 19°	171w	NC	(8)		
6	Front Lights C	S4 Lustr3 19°	171w	NC	(3)		
7	Front Lights I	S4 Lustr3 19°	171w	NC	(9)		
8	Front Lights D	S4 Lustr3 19°	171w	NC	(4)		
9	Front Lights J	S4 Lustr3 19°	171w	NC	(10)		
10	Front Lights E	S4 Lustr3 19°	171w	NC	(5)		

7th E

U#	Purpose	Instrument Type & Accessory	Load	Color & Gobo	Chan	Ad	Dm
1	Down 15' U	S4 Lustr3 36°	171w	NC	(221)		
2	Down 15' V	S4 Lustr3 36°	171w	NC	(222)		
3	Down 15' W	S4 Lustr3 36°	171w	NC	(223)		
4	Down 15' X	S4 Lustr3 36°	171w	NC	(224)		
5	Down 15' Y	S4 Lustr3 36°	171w	NC	(225)		

4th E

U#	Purpose	Instrument Type & Accessory	Load	Color & Gobo	Chan	Ad	Dm
1	Pipe Sides SL P	S4 Lustr3 36°	171w	NC	(251)		
2	Pipe Sides SL Q	S4 Lustr3 26°	171w	NC	(252)		
3	Pipe Sides SL R	S4 Lustr3 19°	171w	NC	(253)		
4	Down 10' P	S4 Lustr3 50°	171w	NC	(86)		
5	Down 15' P	S4 Lustr3 36°	171w	NC	(186)		
6	Down 10' Q	S4 Lustr3 50°	171w	NC	(87)		
7	Down 15' Q	S4 Lustr3 36°	171w	NC	(187)		
8	Back 15' F	S4 Lustr3 36°	171w	NC	(206)		
9	Back 15' G	S4 Lustr3 36°	171w	NC	(207)		
10	Down 10' R	S4 Lustr3 50°	171w	NC	(88)		
11	Down 15' R	S4 Lustr3 36°	171w	NC	(188)		
12	Back 15' H	S4 Lustr3 36°	171w	NC	(208)		
13	Back 15' I	S4 Lustr3 36°	171w	NC	(209)		
14	Back 15' J	S4 Lustr3 36°	171w	NC	(210)		
15	Down 10' S	S4 Lustr3 50°	171w	NC	(89)		
16	Down 15' S	S4 Lustr3 36°	171w	NC	(189)		
17	Down 10' T	S4 Lustr3 50°	171w	NC	(90)		
18	Down 15' T	S4 Lustr3 36°	171w	NC	(190)		
19	Pipe Sides SR P	S4 Lustr3 19°	171w	NC	(256)		
20	Pipe Sides SR S	S4 Lustr3 26°	171w	NC	(257)		
21	Pipe Sides SR T	S4 Lustr3 36°	171w	NC	(258)		

1st E

U#	Purpose	Instrument Type & Accessory	Load	Color & Gobo	Chan	Ad	Dm
1	Pipe Sides SL K	S4 Lustr3 36°	171w	NC	(241)		
2	Pipe Sides SL L	S4 Lustr3 26°	171w	NC	(242)		
3	Pipe Sides SL M	S4 Lustr3 19°	171w	NC	(243)		
4	Down 10' F	S4 Lustr3 36°	171w	NC	(76)		
5	F/S SL M	S4 Lustr3 36°	171w	NC	(23)		
6	F/S SL N	S4 Lustr3 36°	171w	NC	(24)		
7	F/S SL O	S4 Lustr3 36°	171w	NC	(25)		
8	Down 10' G	S4 Lustr3 36°	171w	NC	(77)		
9	ML	Martin Mac Aura	260w	NC	(373)		
10	Down 10' H	S4 Lustr3 36°	171w	NC	(78)		
11	ML	Martin Mac Aura	260w	NC	(374)		
12	Down 10' I	S4 Lustr3 36°	171w	NC	(79)		
13	F/S SR K	S4 Lustr3 36°	171w	NC	(51)		
14	F/S SR L	S4 Lustr3 36°	171w	NC	(52)		
15	F/S SR M	S4 Lustr3 36°	171w	NC	(53)		
16	Down 10' J	S4 Lustr3 36°	171w	NC	(80)		
17	F/S SR N	S4 Lustr3 36°	171w	NC	(54)		
18	Pipe Sides SR M	S4 Lustr3 19°	171w	NC	(246)		
19	Pipe Sides SR N	S4 Lustr3 26°	171w	NC	(247)		
20	Pipe Sides SR O	S4 Lustr3 36°	171w	NC	(248)		

Far Box Boom R

U#	Purpose	Instrument Type & Accessory	Load	Color & Gobo	Chan	Ad	Dm
1	Far Side	S4 Lustr3 19°	171w	NC	(384)		
2	Far Side	S4 Lustr3 19°	171w	NC	(385)		

Far Box Boom L

U#	Purpose	Instrument Type & Accessory	Load	Color & Gobo	Chan	Ad	Dm
1	Far Side	S4 Lustr3 19°	171w	NC	(381)		
2	Far Side	S4 Lustr3 19°	171w	NC	(382)		
3	Far Side	S4 Lustr3 19°	171w	NC	(383)		

Channel	Position	U#	Inst Type & Access & Load	Purpose	Clr & Gbo	Dm	Ad
(1)	Far Cat	2	S4 Lustr3 19° 171w	Front Lights A	NC		
(2)	Far Cat	4	S4 Lustr3 19° 171w	Front Lights B	NC		
(3)	Far Cat	6	S4 Lustr3 19° 171w	Front Lights C	NC		
(4)	Far Cat	8	S4 Lustr3 19° 171w	Front Lights D	NC		
(5)	Far Cat	10	S4 Lustr3 19° 171w	Front Lights E	NC		
(6)	Far Cat	1	S4 Lustr3 19° 171w	Front Lights F	NC		
(7)	Far Cat	3	S4 Lustr3 19° 171w	Front Lights G	NC		
(8)	Far Cat	5	S4 Lustr3 19° 171w	Front Lights H	NC		
(9)	Far Cat	7	S4 Lustr3 19° 171w	Front Lights I	NC		
(10)	Far Cat	9	S4 Lustr3 19° 171w	Front Lights J	NC		
(11)	Mid Cat	2	S4 Lustr3 26° 171w	F/S SL A	NC		
(12)	Mid Cat	4	S4 Lustr3 26° 171w	F/S SL B	NC		
(13)	Mid Cat	6	S4 Lustr3 26° 171w	F/S SL C	NC		
(14)	Mid Cat	8	S4 Lustr3 26° 171w	F/S SL D	NC		
(15)	Mid Cat	10	S4 Lustr3 26° 171w	F/S SL E	NC		
(16)	Mid Cat	1	S4 Lustr3 26° 171w	F/S SL F	NC		
(17)	Mid Cat	3	S4 Lustr3 26° 171w	F/S SL G	NC		
(18)	Mid Cat	5	S4 Lustr3 26° 171w	F/S SL H	NC		
(19)	Mid Cat	7	S4 Lustr3 26° 171w	F/S SL I	NC		
(20)	Mid Cat	9	S4 Lustr3 26° 171w	F/S SL J	NC		
(23)	1st E	5	S4 Lustr3 36° 171w	F/S SL M	NC		
(24)	1st E	6	S4 Lustr3 36° 171w	F/S SL N	NC		
(25)	1st E	7	S4 Lustr3 36° 171w	F/S SL O	NC		
(27)	3rd E	3	S4 Lustr3 50° 171w	F/S 10' SL Q	NC		
(28)	3rd E	5	S4 Lustr3 50° 171w	F/S 10' SL R	NC		
(29)	3rd E	7	S4 Lustr3 50° 171w	F/S 10' SL S	NC		

Channel	Position	U#	Inst Type & Access & Load	Purpose	Clr & Gbo	Dm	Ad
(30)	3rd E	9	S4 Lustr3 50° 171w	F/S 10' SL T	NC		
(41)	Mid Cat	12	S4 Lustr3 26° 171w	F/S SR A	NC		
(42)	Mid Cat	14	S4 Lustr3 26° 171w	F/S SR B	NC		
(43)	Mid Cat	16	S4 Lustr3 26° 171w	F/S SR C	NC		
(44)	Mid Cat	18	S4 Lustr3 26° 171w	F/S SR D	NC		
(45)	Mid Cat	20	S4 Lustr3 26° 171w	F/S SR E	NC		
(46)	Mid Cat	13	S4 Lustr3 26° 171w	F/S SR F	NC		
(47)	Mid Cat	15	S4 Lustr3 26° 171w	F/S SR G	NC		
(48)	Mid Cat	17	S4 Lustr3 26° 171w	F/S SR H	NC		
(49)	Mid Cat	19	S4 Lustr3 26° 171w	F/S SR I	NC		
(50)	Mid Cat	21	S4 Lustr3 26° 171w	F/S SR J	NC		
(51)	1st E	13	S4 Lustr3 36° 171w	F/S SR K	NC		
(52)	1st E	14	S4 Lustr3 36° 171w	F/S SR L	NC		
(53)	1st E	15	S4 Lustr3 36° 171w	F/S SR M	NC		
(54)	1st E	17	S4 Lustr3 36° 171w	F/S SR N	NC		
(56)	3rd E	11	S4 Lustr3 50° 171w	F/S 10' SR P	NC		
(57)	3rd E	13	S4 Lustr3 50° 171w	F/S 10' SR Q	NC		
(58)	3rd E	15	S4 Lustr3 50° 171w	F/S 10' SR R	NC		
(59)	3rd E	17	S4 Lustr3 50° 171w	F/S 10' SR S	NC		
(60)	3rd E	19	S4 Lustr3 50° 171w	F/S 10' SR T	NC		
(71)	Near Cat US	2	S4 Lustr3 26° 171w	Down A	NC		
(72)	Near Cat US	4	S4 Lustr3 26° 171w	Down B	NC		
(73)	Near Cat US	6	S4 Lustr3 26° 171w	Down C	NC		
(74)	Near Cat US	8	S4 Lustr3 26° 171w	Down D	NC		

Channel	Position	U#	Inst Type & Access & Load	Purpose	Clr & Gbo	Dm	Ad
(75)	Near Cat US	10	S4 Lustr3 26° 171w	Down E	NC		
(76)	1st E	4	S4 Lustr3 36° 171w	Down 10' F	NC		
(77)	1st E	8	S4 Lustr3 36° 171w	Down 10' G	NC		
(78)	1st E	10	S4 Lustr3 36° 171w	Down 10' H	NC		
(79)	1st E	12	S4 Lustr3 36° 171w	Down 10' I	NC		
(80)	1st E	16	S4 Lustr3 36° 171w	Down 10' J	NC		
(81)	2nd E	1	S4 Lustr3 36° 171w	Down 10' K	NC		
(82)	2nd E	4	S4 Lustr3 36° 171w	Down 10' L	NC		
(83)	2nd E	7	S4 Lustr3 36° 171w	Down 10' M	NC		
(84)	2nd E	10	S4 Lustr3 36° 171w	Down 10' N	NC		
(85)	2nd E	13	S4 Lustr3 36° 171w	Down 10' O	NC		
(86)	4th E	4	S4 Lustr3 50° 171w	Down 10' P	NC		
(87)	4th E	6	S4 Lustr3 50° 171w	Down 10' Q	NC		
(88)	4th E	10	S4 Lustr3 50° 171w	Down 10' R	NC		
(89)	4th E	15	S4 Lustr3 50° 171w	Down 10' S	NC		
(90)	4th E	17	S4 Lustr3 50° 171w	Down 10' T	NC		
(126)	3rd E	1	S4 Lustr3 26° 171w	F/S 15' SL P	NC		
(127)	3rd E	2	S4 Lustr3 26° 171w	F/S 15' SL Q	NC		
(128)	3rd E	4	S4 Lustr3 26° 171w	F/S 15' SL R	NC		
(129)	3rd E	6	S4 Lustr3 26° 171w	F/S 15' SL S	NC		
(130)	3rd E	8	S4 Lustr3 26° 171w	F/S 15' SL T	NC		
(131)	5th E	1	S4 Lustr3 26° 171w	F/S 15' SL U	NC		
(132)	5th E	2	S4 Lustr3 26° 171w	F/S 15' SL V	NC		
(133)	5th E	4	S4 Lustr3 26° 171w	F/S 15' SL W	NC		
(134)	5th E	6	S4 Lustr3 26° 171w	F/S 15' SL X	NC		

Channel	Position	U#	Inst Type & Access & Load	Purpose	Clr & Gbo	Dm	Ad
(135)	5th E	7	S4 Lustr3 26° 171w	F/S 15' SL Y	NC		
(156)	3rd E	12	S4 Lustr3 26° 171w	F/S 15' SR P	NC		
(157)	3rd E	14	S4 Lustr3 26° 171w	F/S 15' SR Q	NC		
(158)	3rd E	16	S4 Lustr3 26° 171w	F/S 15' SR R	NC		
(159)	3rd E	18	S4 Lustr3 26° 171w	F/S 15' SR S	NC		
(160)	3rd E	20	S4 Lustr3 26° 171w	F/S 15' SR T	NC		
(161)	5th E	9	S4 Lustr3 26° 171w	F/S 15' SR U	NC		
(162)	5th E	10	S4 Lustr3 26° 171w	F/S 15' SR V	NC		
(163)	5th E	12	S4 Lustr3 26° 171w	F/S 15' SR W	NC		
(164)	5th E	14	S4 Lustr3 26° 171w	F/S 15' SR X	NC		
(165)	5th E	15	S4 Lustr3 26° 171w	F/S 15' SR Y	NC		
(176)	Near Cat US	1	S4 Lustr3 26° 171w	Down 15' F	NC		
(177)	Near Cat US	3	S4 Lustr3 26° 171w	Down 15' G	NC		
(178)	Near Cat US	5	S4 Lustr3 26° 171w	Down 15' H	NC		
(179)	Near Cat US	7	S4 Lustr3 26° 171w	Down 15' I	NC		
(180)	Near Cat US	9	S4 Lustr3 26° 171w	Down 15' J	NC		
(181)	2nd E	3	S4 Lustr3 26° 171w	Down 15' K	NC		
(182)	2nd E	6	S4 Lustr3 26° 171w	Down 15' L	NC		
(183)	2nd E	9	S4 Lustr3 26° 171w	Down 15' M	NC		
(184)	2nd E	12	S4 Lustr3 26° 171w	Down 15' N	NC		
(185)	2nd E	15	S4 Lustr3 26° 171w	Down 15' O	NC		
(186)	4th E	5	S4 Lustr3 36° 171w	Down 15' P	NC		
(187)	4th E	7	S4 Lustr3 36° 171w	Down 15' Q	NC		

Channel	Position	U#	Inst Type & Access & Load	Purpose	Clr & Gbo	Dm	Ad
(188)	4th E	11	S4 Lustr3 36° 171w	Down 15' R	NC		
(189)	4th E	16	S4 Lustr3 36° 171w	Down 15' S	NC		
(190)	4th E	18	S4 Lustr3 36° 171w	Down 15' T	NC		
(191)	6th E	4	S4 Lustr3 36° 171w	Back 15' U	NC		
(192)	6th E	5	S4 Lustr3 36° 171w	Back 15' V	NC		
(193)	6th E	11	S4 Lustr3 36° 171w	Back 15' W	NC		
(194)	6th E	17	S4 Lustr3 36° 171w	Back 15' X	NC		
(195)	6th E	18	S4 Lustr3 36° 171w	Back 15' Y	NC		
(201)	2nd E	2	S4 Lustr3 26° 171w	Back 15' A	NC		
(202)	2nd E	5	S4 Lustr3 26° 171w	Back 15' B	NC		
(203)	2nd E	8	S4 Lustr3 26° 171w	Back 15' C	NC		
(204)	2nd E	11	S4 Lustr3 26° 171w	Back 15' D	NC		
(205)	2nd E	14	S4 Lustr3 26° 171w	Back 15' E	NC		
(206)	4th E	8	S4 Lustr3 36° 171w	Back 15' F	NC		
(207)	4th E	9	S4 Lustr3 36° 171w	Back 15' G	NC		
(208)	4th E	12	S4 Lustr3 36° 171w	Back 15' H	NC		
(209)	4th E	13	S4 Lustr3 36° 171w	Back 15' I	NC		
(210)	4th E	14	S4 Lustr3 36° 171w	Back 15' J	NC		
(211)	6th E	7	S4 Lustr3 36° 171w	Back 15' K	NC		
(212)	6th E	9	S4 Lustr3 36° 171w	Back 15' L	NC		
(213)	6th E	12	S4 Lustr3 36° 171w	Back 15' M	NC		
(214)	6th E	14	S4 Lustr3 36° 171w	Back 15' N	NC		
(215)	6th E	16	S4 Lustr3 36° 171w	Back 15' O	NC		
(216)	6th E	6	S4 Lustr3 36° 171w	Back 15' P	NC		
(217)	6th E	8	S4 Lustr3 36° 171w	Back 15' Q	NC		
(218)	6th E	10	S4 Lustr3 36° 171w	Back 15' R	NC		

Channel	Position	U#	Inst Type & Access & Load	Purpose	Clr & Gbo	Dm	Ad
(219)	6th E	13	S4 Lustr3 36° 171w	Back 15' S	NC		
(220)	6th E	15	S4 Lustr3 36° 171w	Back 15' T	NC		
(221)	7th E	1	S4 Lustr3 36° 171w	Down 15' U	NC		
(222)	7th E	2	S4 Lustr3 36° 171w	Down 15' V	NC		
(223)	7th E	3	S4 Lustr3 36° 171w	Down 15' W	NC		
(224)	7th E	4	S4 Lustr3 36° 171w	Down 15' X	NC		
(225)	7th E	5	S4 Lustr3 36° 171w	Down 15' Y	NC		
(231)	Near Cat	1	S4 Lustr3 36° 171w	Pipe Sides SL A	NC		
(232)	Near Cat	2	S4 Lustr3 26° 171w	Pipe Sides SL B	NC		
(233)	Near Cat	3	S4 Lustr3 19° 171w	Pipe Sides SL C	NC		
(236)	Near Cat	5	S4 Lustr3 19° 171w	Pipe Sides SR C	NC		
(237)	Near Cat	6	S4 Lustr3 26° 171w	Pipe Sides SR D	NC		
(238)	Near Cat	7	S4 Lustr3 36° 171w	Pipe Sides SR E	NC		
(241)	1st E	1	S4 Lustr3 36° 171w	Pipe Sides SL K	NC		
(242)	1st E	2	S4 Lustr3 26° 171w	Pipe Sides SL L	NC		
(243)	1st E	3	S4 Lustr3 19° 171w	Pipe Sides SL M	NC		
(246)	1st E	18	S4 Lustr3 19° 171w	Pipe Sides SR M	NC		
(247)	1st E	19	S4 Lustr3 26° 171w	Pipe Sides SR N	NC		
(248)	1st E	20	S4 Lustr3 36° 171w	Pipe Sides SR O	NC		
(251)	4th E	1	S4 Lustr3 36° 171w	Pipe Sides SL P	NC		
(252)	4th E	2	S4 Lustr3 26° 171w	Pipe Sides SL Q	NC		
(253)	4th E	3	S4 Lustr3 19° 171w	Pipe Sides SL R	NC		
(256)	4th E	19	S4 Lustr3 19° 171w	Pipe Sides SR P	NC		
(257)	4th E	20	S4 Lustr3 26° 171w	Pipe Sides SR S	NC		
(258)	4th E	21	S4 Lustr3 36° 171w	Pipe Sides SR T	NC		

Channel	Position	U#	Inst Type & Access & Load	Purpose	Clr & Gbo	Dm	Ad
(261)	6th E	1	S4 Lustr3 36° 171w	Pipe Sides SL U	NC		
(262)	6th E	2	S4 Lustr3 26° 171w	Pipe Sides SL V	NC		
(263)	6th E	3	S4 Lustr3 19° 171w	Pipe Sides SL W	NC		
(266)	6th E	19	S4 Lustr3 19° 171w	Pipe Sides SR U	NC		
(267)	6th E	20	S4 Lustr3 26° 171w	Pipe Sides SR X	NC		
(268)	6th E	21	S4 Lustr3 36° 171w	Pipe Sides SR Y	NC		
(281)	Boom SR 1	2	S4 Lustr3 50° 171w	SR Walls - Wall G	NC		
(282)	Boom SL 1	2	S4 Lustr3Fresnel 171w	SL Walls - Wall A	NC		
(291)	Boom SL 2	2	S4 Lustr3Fresnel 171w	SL Walls B	NC		
(292)	Boom SL 2	4	S4 Lustr3Fresnel 171w	SL Walls B	NC		
(293)	Boom SL 2	6	S4 Lustr3Fresnel 171w	SL Walls B	NC		
(296)	Boom SR 2	2	S4 Lustr3Fresnel 171w	SR Walls E	NC		
(297)	Boom SR 2	4	S4 Lustr3Fresnel 171w	SR Walls E	NC		
(298)	Boom SR 2	6	S4 Lustr3Fresnel 171w	SR Walls E	NC		
(301)	Boom SL 3	2	S4 Lustr3Fresnel 171w	SL Walls CD	NC		
(302)	Boom SL 3	4	S4 Lustr3Fresnel 171w	SL Walls CD	NC		
(303)	Boom SL 3	5	S4 Lustr3Fresnel 171w	SL Walls CD	NC		
(304)	Boom SL 3	7	S4 Lustr3Fresnel 171w	SL Walls CD	NC		
(306)	Boom SR 3	2	S4 Lustr3Fresnel 171w	SR Walls CD	NC		
(307)	Boom SR 3	4	S4 Lustr3Fresnel 171w	SR Walls CD	NC		
(308)	Boom SR 3	5	S4 Lustr3Fresnel 171w	SR Walls CD	NC		




Channel	Position	U#	Inst Type & Access & Load	Purpose	Clr & Gbo	Dm	Ad
(309)	Boom SR 3	7	S4 Lustr3Fresnel 171w	SR Walls CD	NC		
(311)	Boom SL 4	2	S4 Lustr3Fresnel 171w	SL Curtain	NC		
(312)	Boom SL 4	4	S4 Lustr3Fresnel 171w	SL Curtain	NC		
(313)	Boom SL 4	6	S4 Lustr3Fresnel 171w	SL Curtain	NC		
(316)	Boom SR 4	2	S4 Lustr3Fresnel 171w	SR Curtain	NC		
(317)	Boom SR 4	4	S4 Lustr3Fresnel 171w	SR Curtain	NC		
(318)	Boom SR 4	6	S4 Lustr3Fresnel 171w	SR Curtain	NC		
(321)	Boom SL 1	1	S4 Lustr2 36° 171w	SL Shins	NC		
(322)	Boom SL 2	1	S4 Lustr3 36° 171w	SL Shins	NC		
(323)	Boom SL 3	1	S4 Lustr2 36° 171w	SL Shins	NC		
(324)	Boom SL 4	1	S4 Lustr2 36° 171w	SL Shins	NC		
(326)	Boom SR 1	1	S4 Lustr2 36° 171w	SR Shin	NC		
(327)	Boom SR 2	1	S4 Lustr2 36° 171w	SR Shin	NC		
(328)	Boom SR 3	1	S4 Lustr2 36° 171w	SR Shin	NC		
(329)	Boom SR 4	1	S4 Lustr2 36° 171w	SR Shin	NC		
(331)	Boom SL 1	3	S4 Lustr3 36° 171w	SL Mids	NC		
(332)	Boom SL 2	3	S4 Lustr3 36° 171w	SL Mids	NC		
(333)	Boom SL 3	3	S4 Lustr3 36° 171w	SL Mids	NC		
(334)	Boom SL 4	3	S4 Lustr3 36° 171w	SL Mids	NC		
(336)	Boom SR 1	3	S4 Lustr3 36° 171w	SR Mid	NC		
(337)	Boom SR 2	3	S4 Lustr3 36° 171w	SR Mid	NC		

Channel	Position	U#	Inst Type & Access & Load	Purpose	Clr & Gbo	Dm	Ad
(338)	Boom SR 3	3	S4 Lustr3 36° 171w	SR Mid	NC		
(339)	Boom SR 4	3	S4 Lustr3 36° 171w	SR Mid	NC		
(341)	Boom SL 1	4	S4 Lustr2 50° 171w	SL Heads	NC		
(342)	Boom SL 2	5	S4 Lustr2 50° 171w	SL Heads	NC		
(343)	Boom SL 3	6	S4 Lustr2 50° 171w	SL Heads	NC		
(344)	Boom SL 4	5	S4 Lustr2 50° 171w	SL Heads	NC		
(346)	Boom SR 1	4	S4 Lustr2 50° 171w	SR Heads	NC		
(347)	Boom SR 2	5	S4 Lustr2 50° 171w	SR Heads	NC		
(348)	Boom SR 3	6	S4 Lustr2 50° 171w	SR Heads	NC		
(349)	Boom SR 4	5	S4 Lustr2 50° 171w	SR Heads	NC		
(351)	5th E	3	ETC D60 Lustr SELO3070 161w	Curtain Light	NC		
(352)	5th E	5	ETC D60 Lustr SELO3070 161w	Curtain Light	NC		
(353)	5th E	8	ETC D60 Lustr SELO3070 161w	Curtain Light	NC		
(354)	5th E	11	ETC D60 Lustr SELO3070 161w	Curtain Light	NC		
(355)	5th E	13	ETC D60 Lustr SELO3070 161w	Curtain Light	NC		
(361)	Ground US	1	ETC D60 Lustr SELO3070 161w	Ground Light	NC		
(362)	Ground US	2	ETC D60 Lustr SELO3070 161w	Ground Light	NC		
(363)	Ground US	3	ETC D60 Lustr SELO3070 161w	Ground Light	NC		

Channel	Position	U#	Inst Type & Access & Load	Purpose	Clr & Gbo	Dm	Ad
(364)	Ground US	4	ETC D60 Lustr SELO3070 161w	Ground Light	NC		
(365)	Ground US	5	ETC D60 Lustr SELO3070 161w	Ground Light	NC		
(371)	Mid Cat	11	Martin Mac Aura 260w	ML	NC		
(372)	Near Cat	4	Martin Mac Aura 260w	ML	NC		
(373)	1st E	9	Martin Mac Aura 260w	ML	NC		
(374)	1st E	11	Martin Mac Aura 260w	ML	NC		
(375)	3rd E	10	Martin Mac Aura 260w	ML	NC		
(381)	Far Box Boom L	1	S4 Lustr3 19° 171w	Far Side	NC		
(382)	Far Box Boom L	2	S4 Lustr3 19° 171w	Far Side	NC		
(383)	Far Box Boom L	3	S4 Lustr3 19° 171w	Far Side	NC		
(384)	Far Box Boom R	1	S4 Lustr3 19° 171w	Far Side	NC		
(385)	Far Box Boom R	2	S4 Lustr3 19° 171w	Far Side	NC		

Flight of a Legless Bird: Magic Sheet (2 of 3)





10' Trim Lights

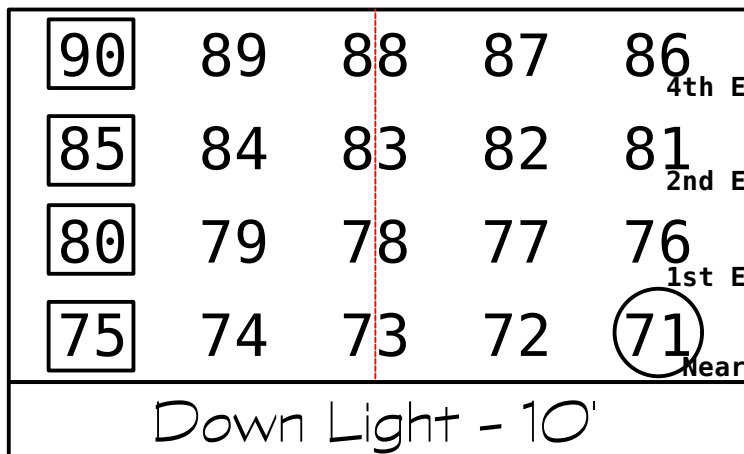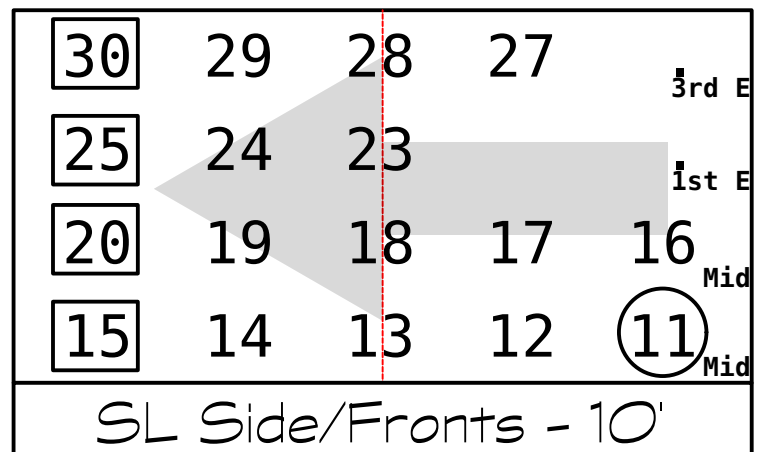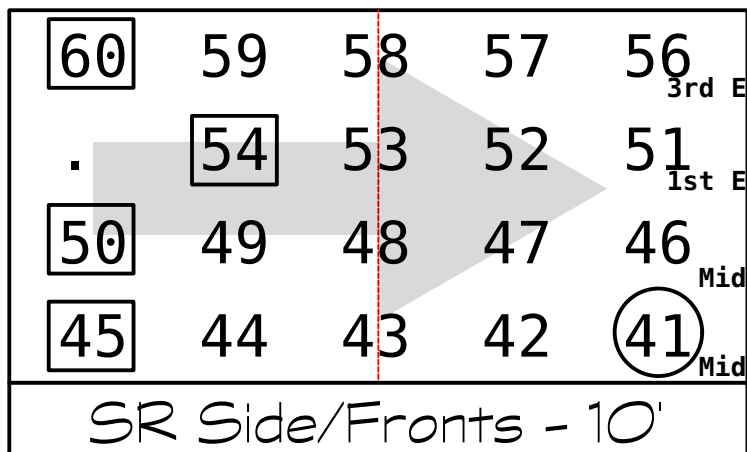

CP	COLOR	
1		R34
2		R325
3		R302
4		R16
5		R321
6		R374
7		R39
8		L733
9		L201
10		L200
11		R83
12		R4
13		R54
14		R80
15		L651
16		L354
17		L790
18		R02
19		L248
-		-
-		-

Flight of a Legless Bird: Magic Sheet (3 of 3)

15' Trim Lights

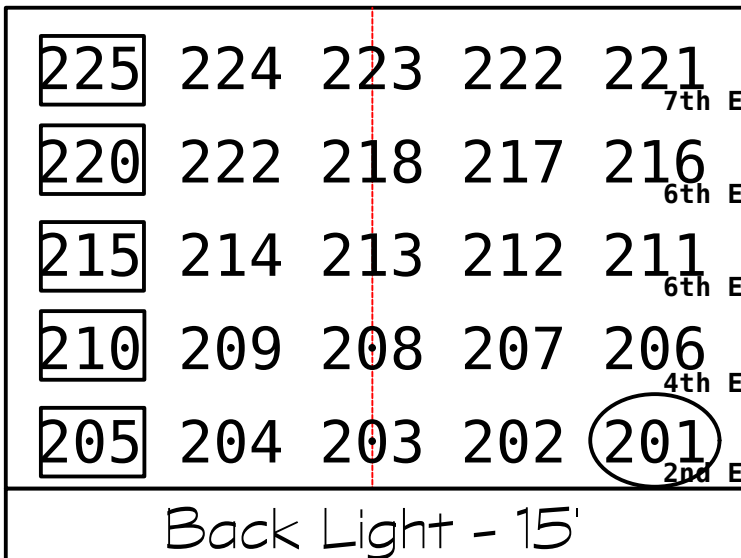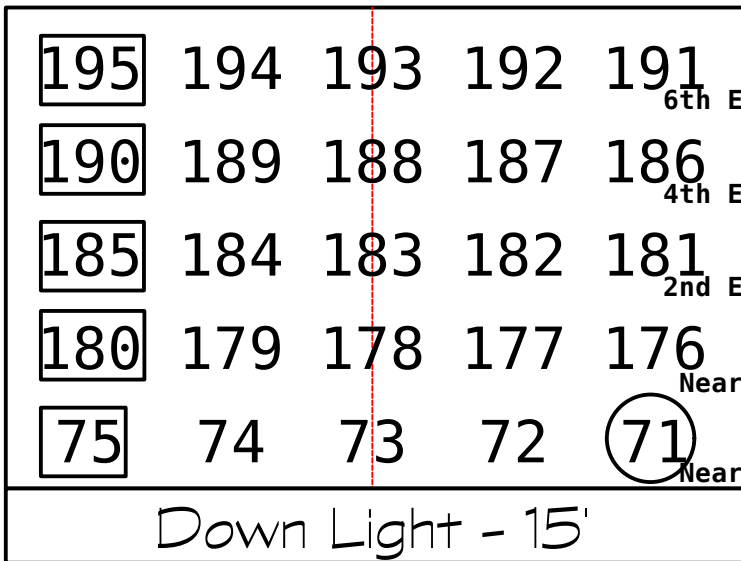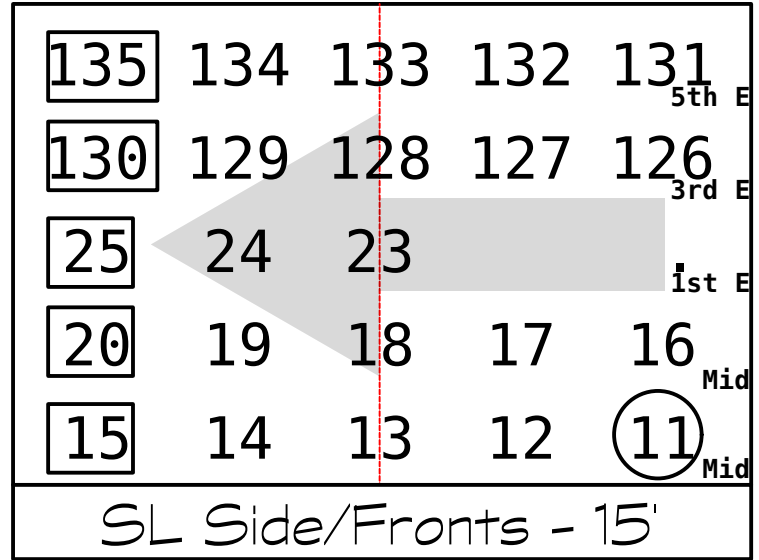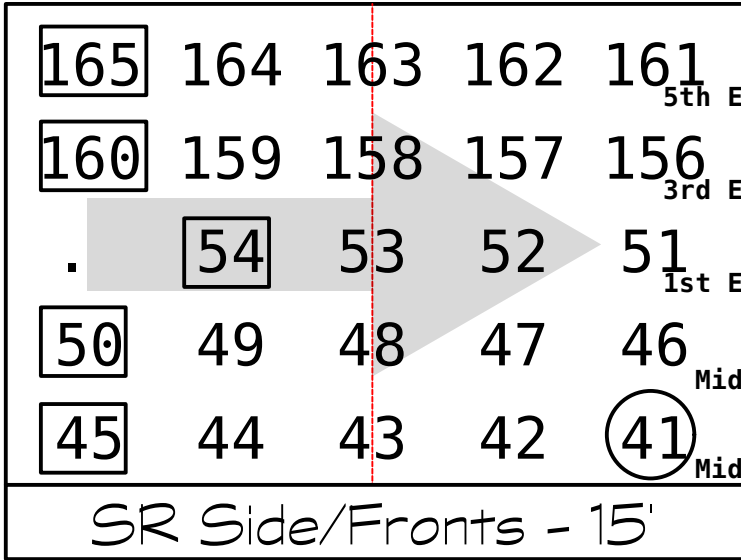

CP	COLOR	
1		R34
2		R325
3		R302
4		R16
5		R321
6		R374
7		R39
8		L733
9		L201
10		L200
11		R83
12		R4
13		R54
14		R80
15		L651
16		L354
17		L790
18		R02
19		L248
-		-
-		-

Flight of a Legless Bird: Magic Sheet (1 of 3)

Vectorworks Educational Version

318	317	316	313	312	311	Boom 4
309	308	307	306	304	303	302 301
298	297	296		293	292	291
	282	383		281		Boom 2
B1, Mid Box SL, B1						
Wall Lights						

	402	Bar
403		Robin's
Lamps		

10	9	8	7	6	Far
5	4	3	2	1	Far
Front Light					

355	354	353	352	351	5th E
365	364	363	362	361	Ground
Curtain Lights					

268	267	266	263	262	261	6th E
258	257	256	253	252	251	4th E
248	247	246	243	242	241	1st E
238	237	236	233	232	231	Near Cat
Beam Ends						

Cats	996	Grid	997
House	998	FOH	999
Work	1000	Booth	1001
Fog	401	Haze	400
Works & Fog/Haze			

329	324
328	323
327	322
326	321
Shins	

339	334
338	333
337	332
336	331
Mids	


349	344
348	343
347	342
346	341
Heads	

	375	3rd E
374	373	1st E
	372	Near Cat
	371	Mid Cat
Moving		

Vectorworks Educational Version

Flight of a Legless Bird
Focus Positions
Scale: 1/4" = 1'

Vectorworks Educational Version

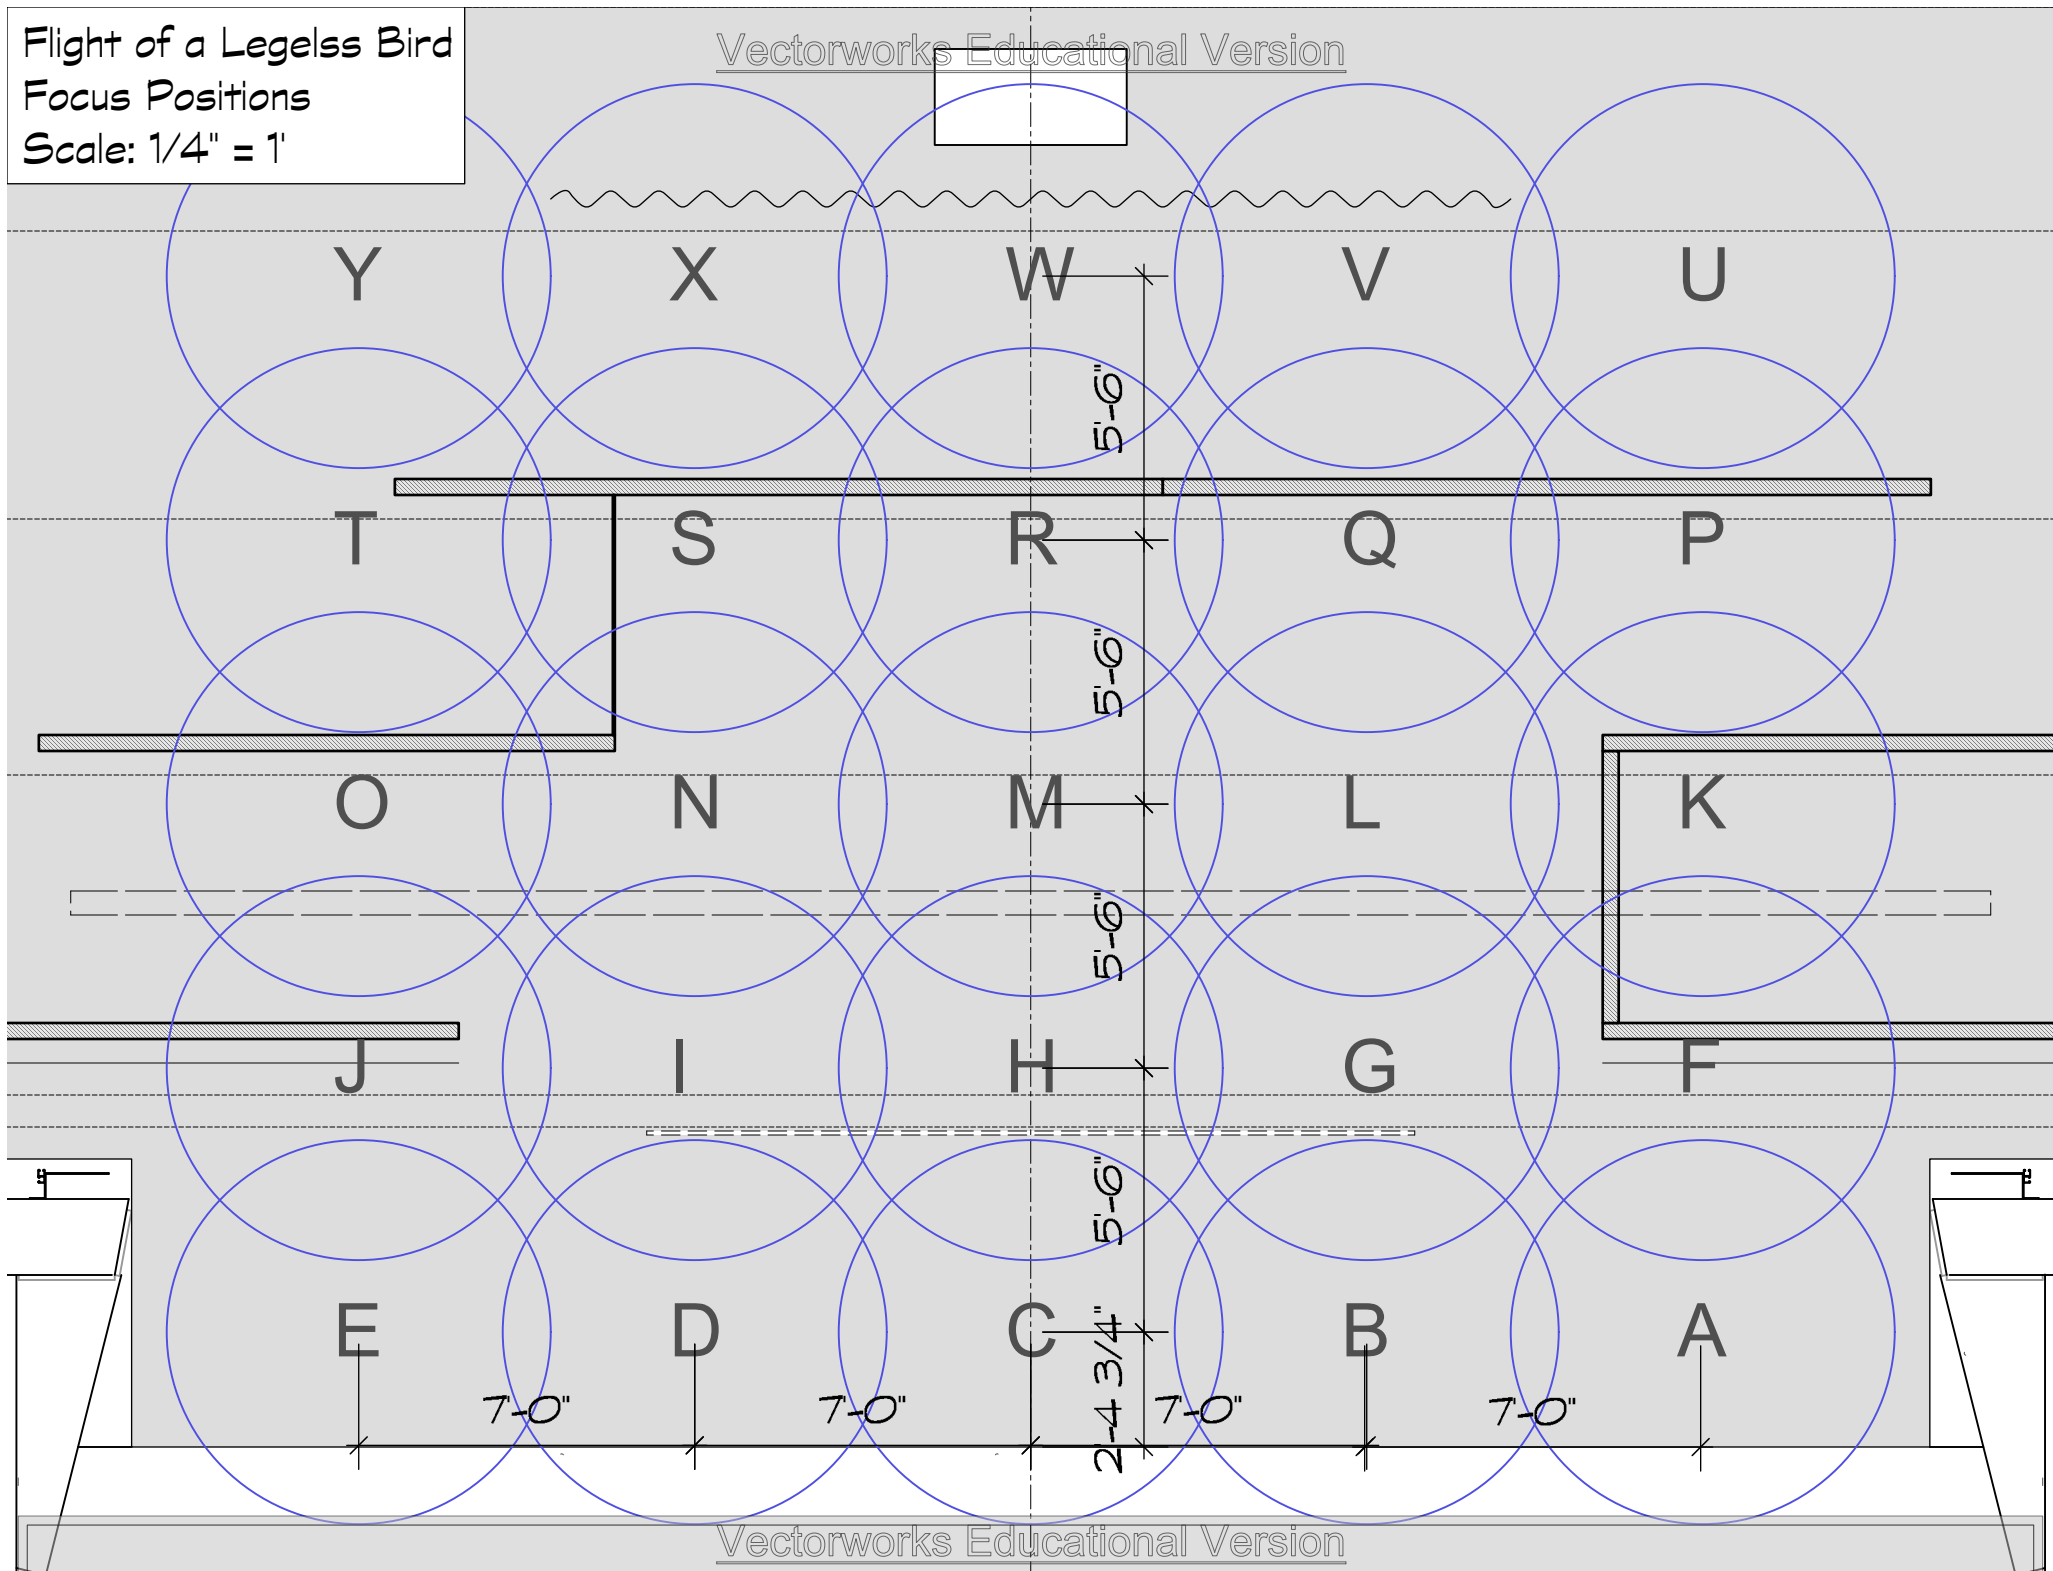

Vectorworks Educational Version