



FUENTE OVEJUNA
Lighting Information v2
JANUARY 15, 2022

Tab Stage Right
Firm Rail Above 9'-6" Clearance Below to SR Wall

Steel Line

Obstructions to 12" deep

Near Box Boom

Near Catwalk

Near Box Boom

House Speaker Positions shown are standard positions and not fixed.

Center Line

Groundrow

-Faces US to Bounce
-Drawn slightly out of place for clarity
-These units can be any available led strip

6th Electric - LS 36

-Faces US to Bounce
-These units can be any LED Strip available

5 Electric - LS 26

4 Electric - LS 19

3 Electric - LS 14

2 Electric - LS 8

1 Electric - LS 3


Hanging Schedule

#39	26'-4"	Bounce
#38	25'-8"	
#37	25'-0"	
#36	24'-4"	6 Electric @ 20'-0"
#35	23'-8"	CYC
#34	23'-0"	
#33	22'-4"	
#32	21'-8"	Black Scrim
#31	21'-0"	#4 Legs
#30	20'-4"	#4 Border @ 18'-0"
#29	19'-8"	
#28	19'-0"	
#27	18'-4"	
#26	17'-8"	5 Electric @ 20'-9"
#25	17'-0"	
#24	16'-4"	
#23	15'-8"	#3 Legs
#22	15'-0"	#3 Border @ 18'-0"
#21	14'-4"	
#20	13'-8"	
#19	13'-0"	4 Electric @ 23'-9"
#18	12'-4"	Fairy Lights
#17	11'-8"	King/Queen Frames
#16	11'-0"	
#15	10'-4"	
#14	9'-8"	3 Electric @ 20'-6"
#13	9'-0"	#2 Legs
#12	8'-4"	#2 Border @ 18'-0"
#11	7'-8"	
#10	7'-0"	
#9	6'-4"	
#8	5'-8"	2 Electric @ 25'-0"
#7	5'-0"	
#6	4'-4"	
#5	3'-8"	
#4	3'-0"	
#3	2'-4"	1 Electric @ 20'-0"
#2	1'-8"	#1 Legs
#1	1'-0"	#1 Border @ 18'-0"
#0	0'-4"	Main Drape

INSTRUMENTATION

- ETC SOURCE 4 50° @575W
- ETC SOURCE 4 36° @575W
- ETC SOURCE 4 26° @575W
- ETC SOURCE 4 19° @575W
- ETC SOURCE 4 LUSTRE 50° @171W
- ETC SOURCE 4 LUSTRE 36° @171W
- ETC SOURCE 4 LUSTRE 19° @171W
- ETC SOURCE 4 TUNG 19° @171W
- ETC SOURCE 4 LUSTRE FRESNEL @171W
- ETC D60 DESIRE @171W
- SOURCE 4 PAR WFL @575W
- MARTIN MAC AURA @260W
- S4 MULTIPAR MFL@3000W
- LED STRIPLIGHTS@1200W

TYPICAL UNIT

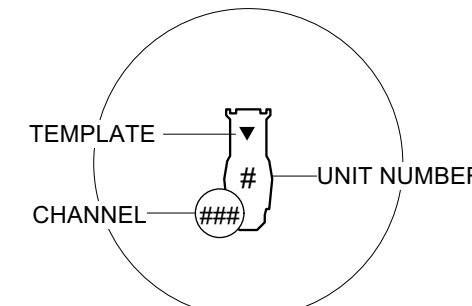

NOTES

- ALL EQUIPMENT SUBSTITUTIONS SHOULD BE DISCUSSED WITH THE COMPANY LIGHTING DIRECTOR IN ADVANCE
- ALL DIMENSIONS ARE FROM CENTER LINE & PLASTER LINE UNLESS OTHERWISE NOTED
- ALL TRIMS ARE FROM STAGE FLOOR TO SIDEARM/PIPE UNLESS NOTED
- OVERSTAGE ELECTRIC TRIM HEIGHTS ARE FROM SYSTEM PIPE. BORDER TRIME HEIGHTS ARE FROM BOTTOM OF GOODS.
- ALL UNITS HUNG ON 18" CENTERS UNLESS OTHERWISE DIMENSIONED
- WRITTEN DIMENSIONS TAKE PRECEDENCE OVER SCALE MEASUREMENTS
- PLEASE SEE HOOKUP FOR COLOR AND ACCESSORY INFORMATION - TOPHAT & BARNDOORS ARE NOT DRAWN ON PLOT
- PLEASE DROP ALL ACCESSORIES & COLOR PRIOR TO START OF FOCUS. COMPANY TRAVELS WITH FRAMED TEMPLATES AND WILL PROVIDE UPON ARRIVAL.

DISCLAIMER

THIS DRAWING REPRESENTS VISUAL CONCEPTS AND CONSTRUCTION SUGGESTIONS ONLY.




LEWIS CENTER PRINCETON arts McCarter THEATRE CENTER

FUENTEOVEJUNA

SCALE: 1/4"=1'-0"

DRAFTED BY: LCA THEATRE DEPARTMENT

PLATE

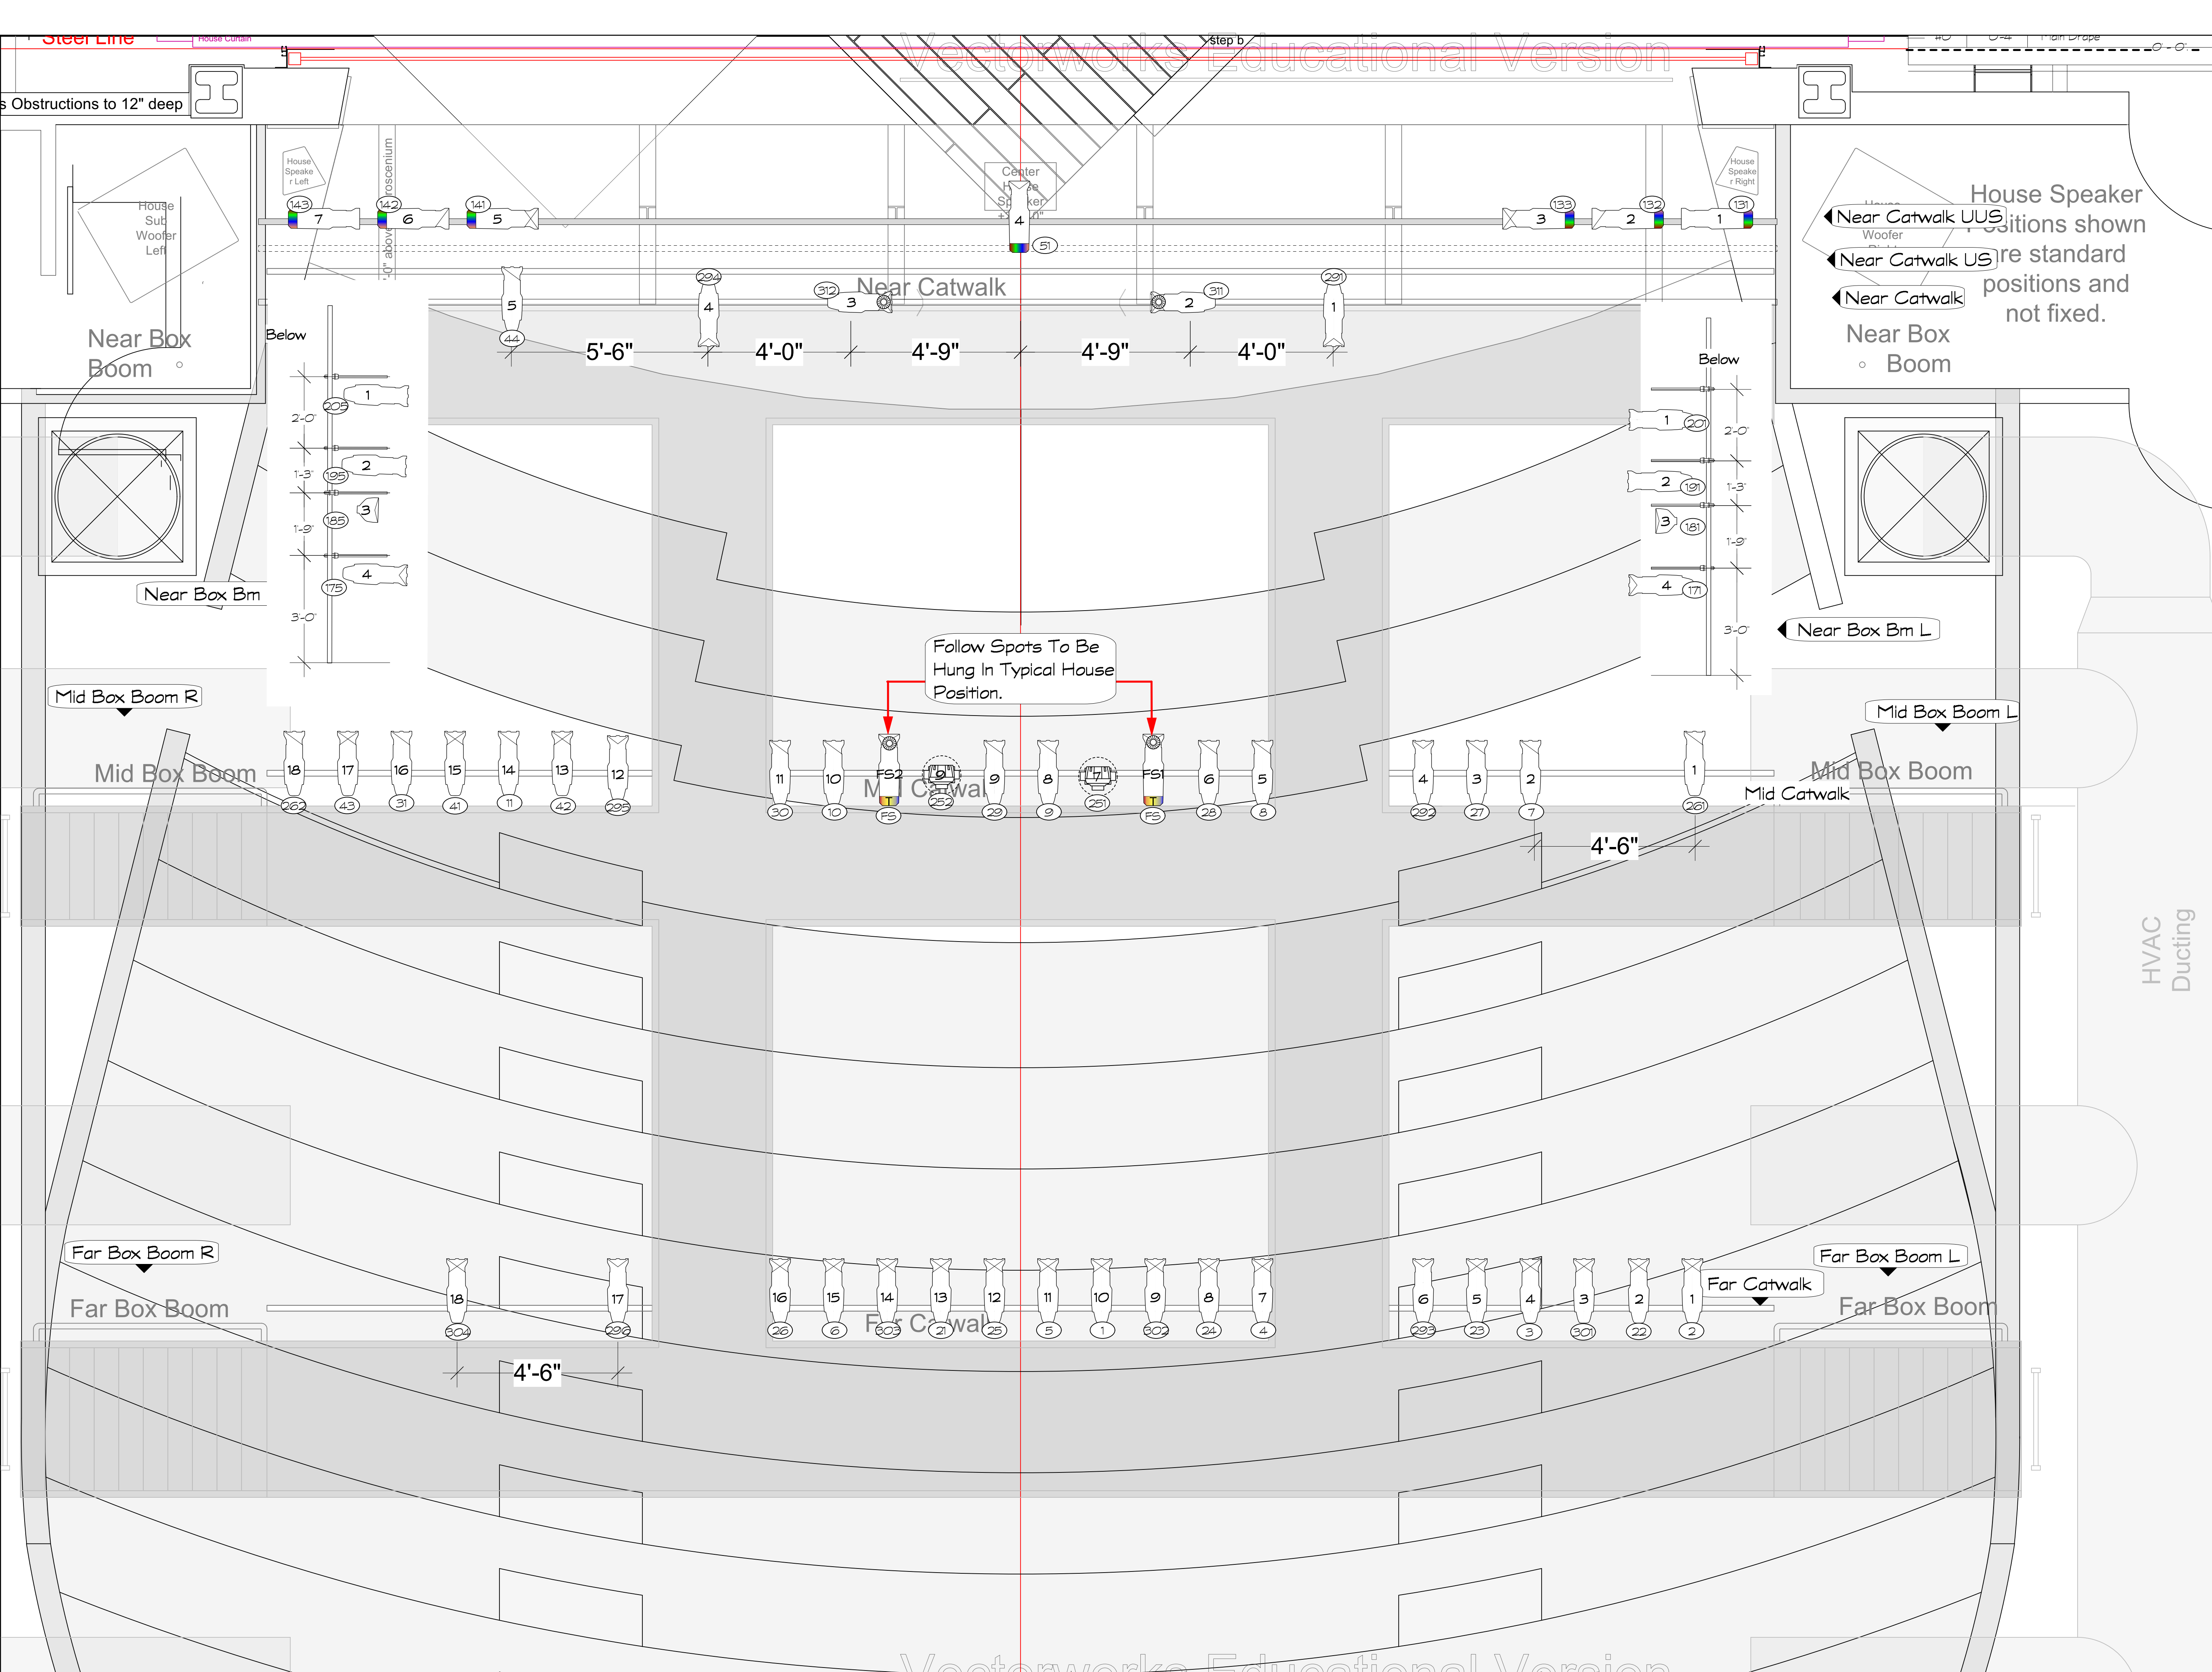

INSTRUMENTATION

ETC SOURCE 4 50° @575W
ETC SOURCE 4 36° @575W
ETC SOURCE 4 26° @575W
ETC SOURCE 4 19° @575W
ETC SOURCE 4 LUSTRE 50° @171W
ETC SOURCE 4 LUSTRE 36° @171W
ETC SOURCE 4 LUSTRE 19° @171W
ETC SOURCE 4 TUNG 19° @171W
ETC SOURCE 4 LUSTRE FRESNEL @171W
ETC D60 DESIRE @171W
SOURCE 4 PAR WFL @575W
MARTIN MAC AURA @260W

S4 MULTIPAR MFL@3000W
COLOR FORCE 72
LED STRIPLIGHTS@1200W

TYPICAL UNIT

TEMPLATE
CHANNEL
UNIT NUMBER

NOTES

- ALL EQUIPMENT SUBSTITUTIONS SHOULD BE DISCUSSED WITH THE COMPANY LIGHTING DIRECTOR IN ADVANCE
- ALL DIMENSIONS ARE FROM CENTER LINE & PLASTER LINE UNLESS OTHERWISE NOTED
- ALL TRIMS ARE FROM STAGE FLOOR TO SIDEARM/PIPE UNLESS NOTED
- OVERSTAGE ELECTRIC TRIM HEIGHTS ARE FROM SYSTEM PIPE. BORDER TRIME HEIGHTS ARE FROM BOTTOM OF GOODS.
- ALL UNITS HUNG ON 18" CENTERS UNLESS OTHERWISE DIMENSIONED
- WRITTEN DIMENSIONS TAKE PRECEDENCE OVER SCALE MEASUREMENTS
- PLEASE SEE HOOKUP FOR COLOR AND ACCESSORY INFORMATION - TOPHAT & BARNDOORS ARE NOT DRAWN ON PLOT
- PLEASE DROP ALL ACCESSORIES & COLOR PRIOR TO START OF FOCUS. COMPANY TRAVELS WITH FRAMED TEMPLATES AND WILL PROVIDE UPON ARRIVAL.

DISCLAIMER

THIS DRAWING REPRESENTS VISUAL CONCEPTS AND CONSTRUCTION SUGGESTIONS ONLY.

THE IMPLEMENTATION OF THIS LIGHTING DESIGN BY THE COMPANY MUST COMPLY WITH THE MOST STRINGENT APPLICABLE FEDERAL AND LOCAL SAFETY AND FIRE CODES. ALL DRAWINGS, EQUIPMENT LISTS, AND ACCESSORY INFORMATION ARE FOR CONCEPTUAL PURPOSES ONLY. THE COMPANY DOES NOT ASSUME RESPONSIBILITY FOR THE PROPER INSTALLATION, OPERATION, MAINTENANCE, OR USE OF THE LIGHTING EQUIPMENT WHICH IMPLEMENTS THIS DESIGN.


LEWIS CENTER arts
PRINCETON
McCarter THEATRE CENTER

FUENTE OVEJUNA

SCALE: 1/4"=1'-0"


DRAFTED BY: LCA THEATRE DEPARTMENT

PLATE

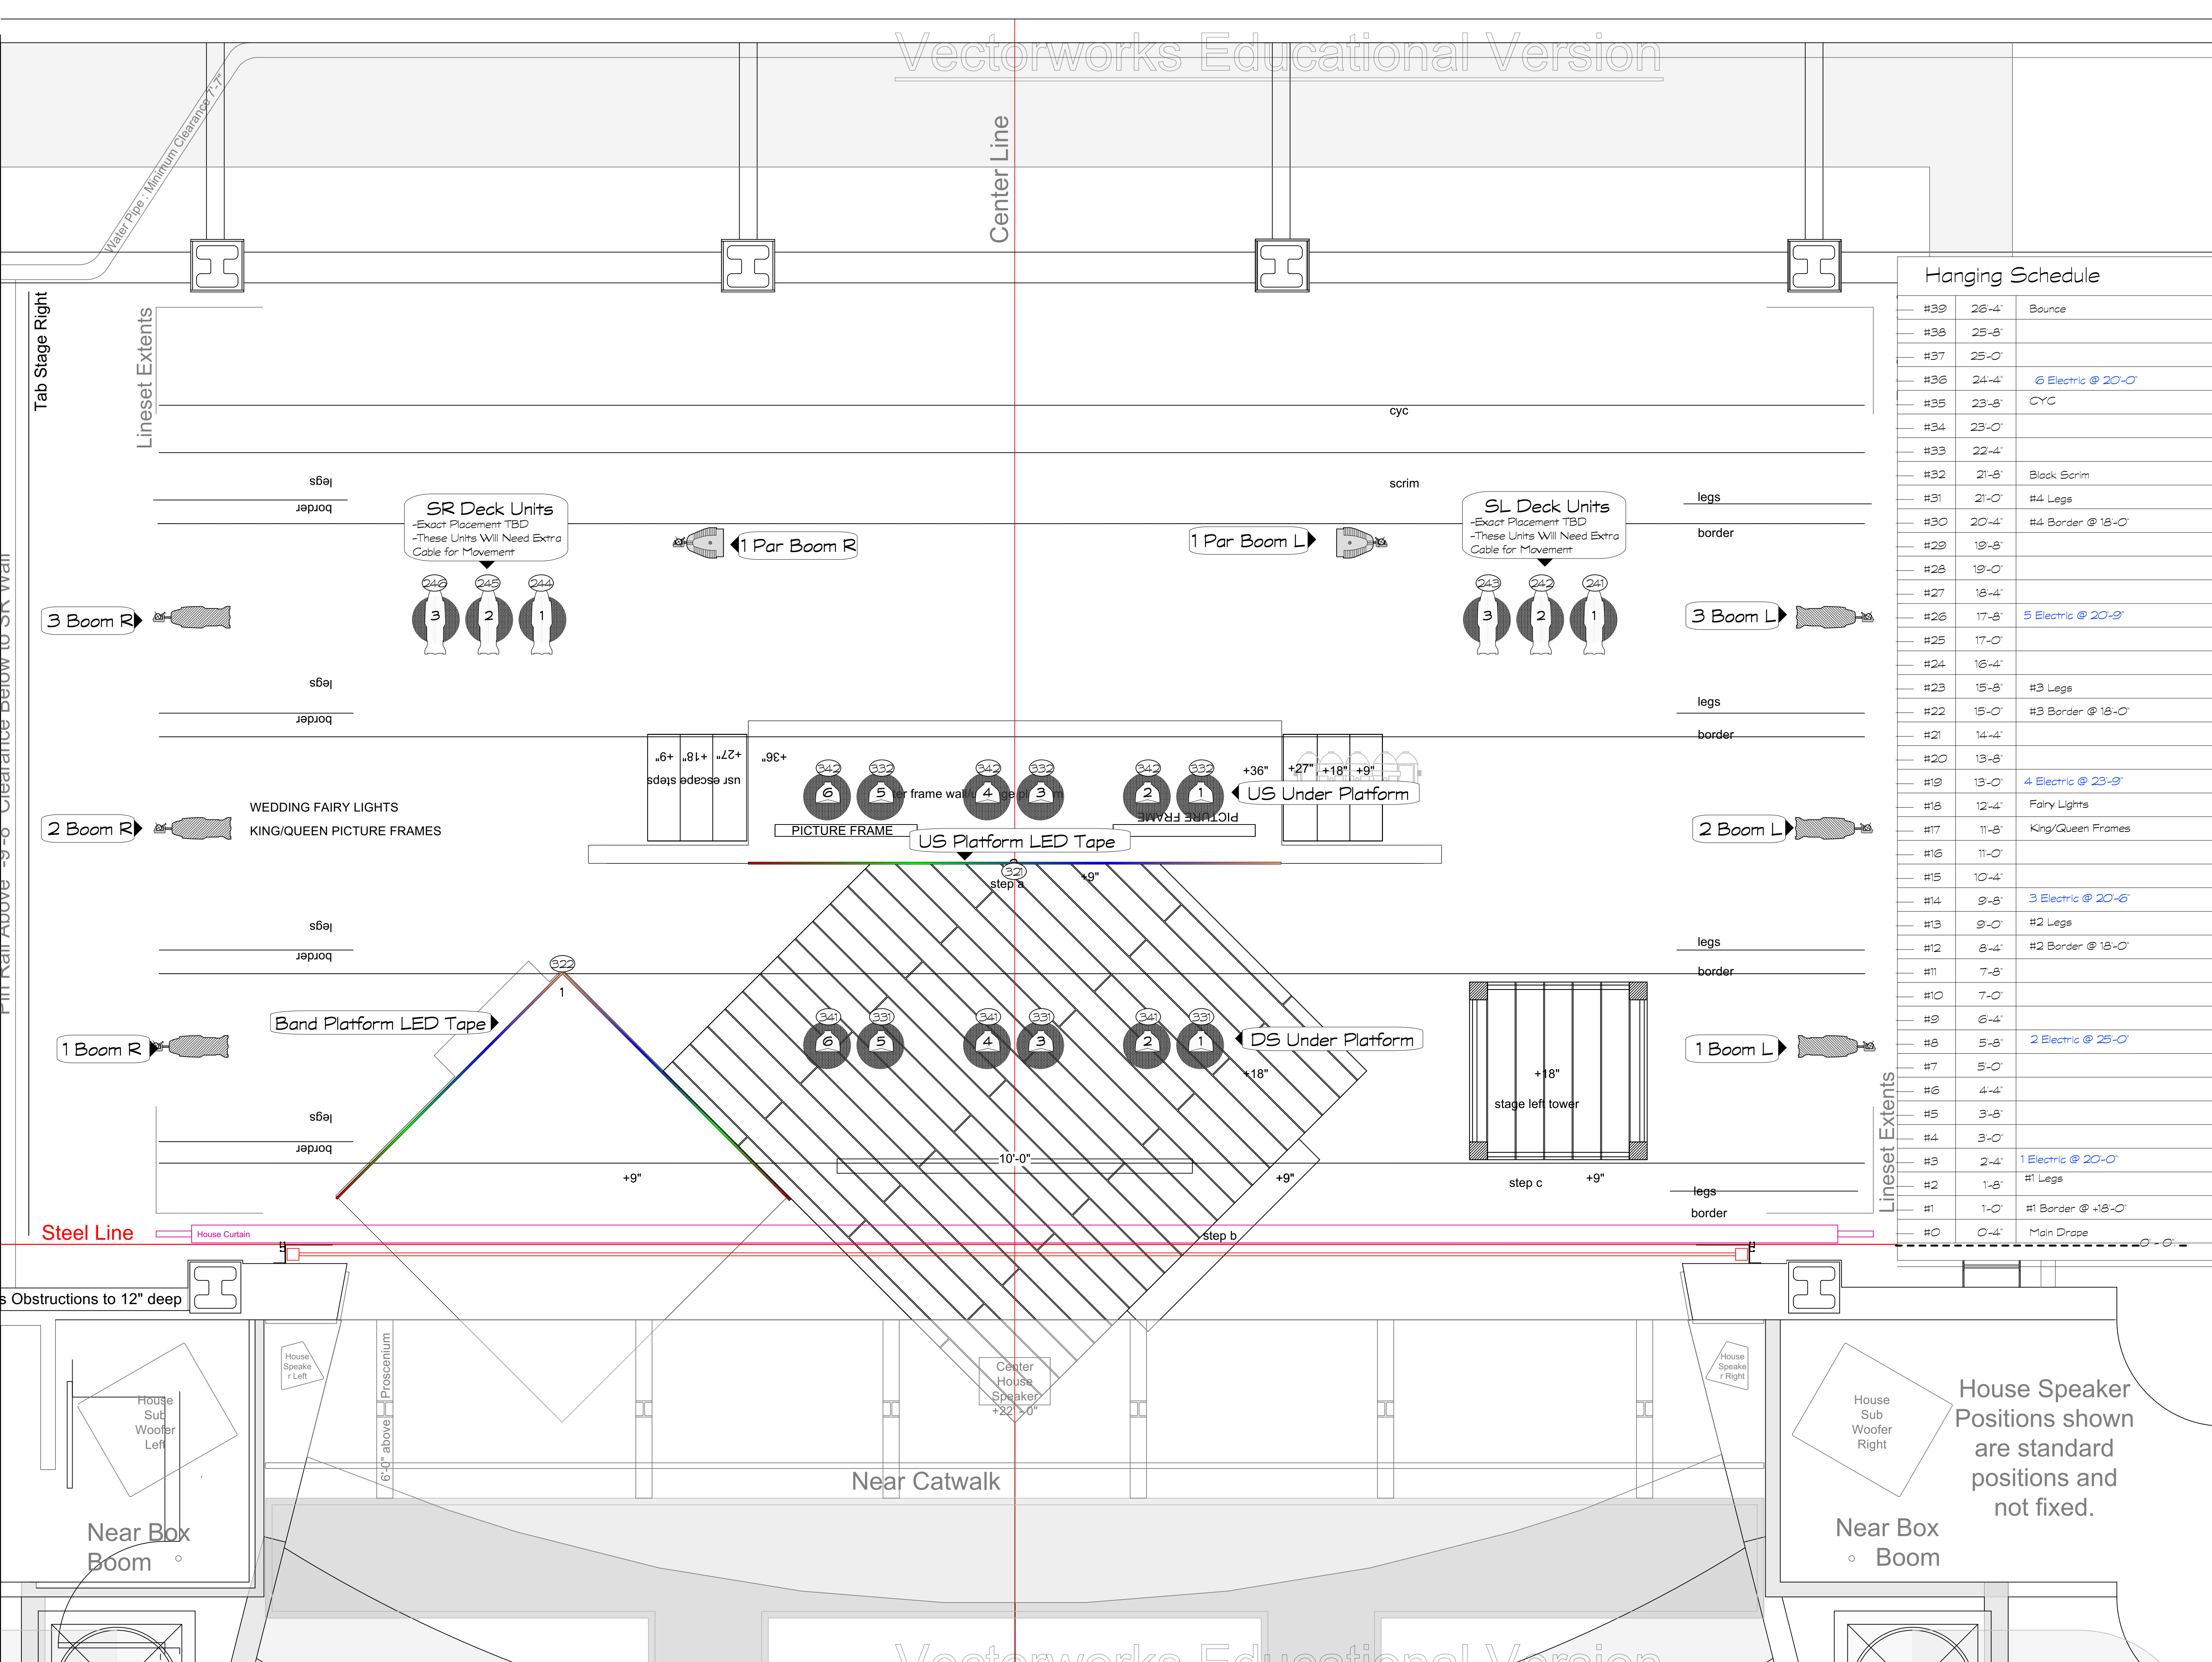

Hanging Schedule		
#39	26'-4"	Bounce
#38	25'-8"	
#37	25'-0"	
#36	24'-4"	6 Electric @ 20'-0"
#35	23'-8"	CYC
#34	23'-0"	
#33	22'-4"	
#32	21'-8"	Black Scrim
#31	21'-0"	#4 Legs
#30	20'-4"	#4 Border @ 18'-0"
#29	19'-8"	
#28	19'-0"	
#27	18'-4"	
#26	17'-8"	5 Electric @ 20'-0"
#25	17'-0"	
#24	16'-4"	
#23	15'-8"	#3 Legs
#22	15'-0"	#3 Border @ 18'-0"
#21	14'-4"	
#20	13'-8"	
#19	13'-0"	4 Electric @ 23'-0"
#18	12'-4"	Fairy Lights
#17	11'-8"	King/Queen Frames
#16	11'-0"	
#15	10'-4"	
#14	9'-8"	3 Electric @ 20'-0"
#13	9'-0"	#2 Legs
#12	8'-4"	#2 Border @ 18'-0"
#11	7'-8"	
#10	7'-0"	
#9	6'-4"	
#8	5'-8"	2 Electric @ 25'-0"
#7	5'-0"	
#6	4'-4"	
#5	3'-8"	
#4	3'-0"	
#3	2'-4"	1 Electric @ 20'-0"
#2	1'-8"	#1 Legs
#1	1'-0"	#1 Border @ 18'-0"
#0	0'-4"	Main Drape


INSTRUMENTATION	
	ETC SOURCE 4 50° @575W
	ETC SOURCE 4 36° @575W
	ETC SOURCE 4 26° @575W
	ETC SOURCE 4 19° @575W
	ETC SOURCE 4 LUSTR 50° @171W
	ETC SOURCE 4 LUSTR 36° @171W
	ETC SOURCE 4 LUSTR 19° @171W
	ETC SOURCE 4 TUNG 19° @171W
	ETC SOURCE 4 LUSTR FRESNEL @171W
	ETC D60 DESIRE @171W
	SOURCE 4 PAR WFL @575W
	MARTIN MAC AURA @260W
	S4 MULTIPAR MFL@3000W
	COLOR FORCE 72
	LED STRIPLIGHTS@1200W

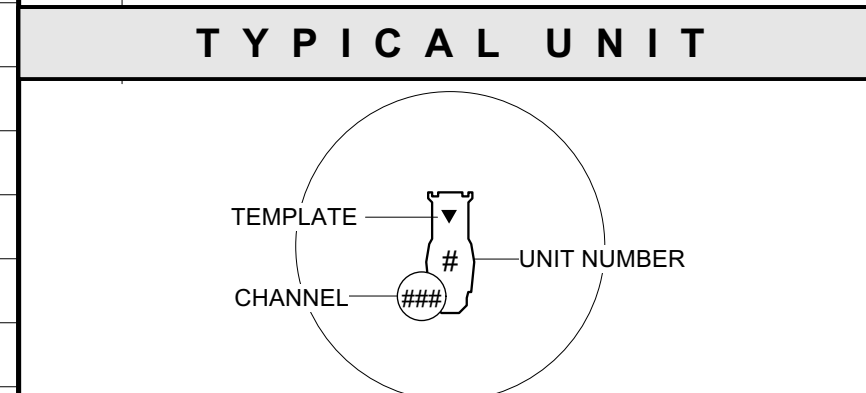


- NOTES**
- ALL EQUIPMENT SUBSTITUTIONS SHOULD BE DISCUSSED WITH THE COMPANY LIGHTING DIRECTOR IN ADVANCE
 - ALL DIMENSIONS ARE FROM CENTER LINE & PLASTER LINE UNLESS OTHERWISE NOTED
 - ALL TRIMS ARE FROM STAGE FLOOR TO SIDEARM/PIPE UNLESS NOTED
 - OVERSTAGE ELECTRIC TRIM HEIGHTS ARE FROM SYSTEM PIPE. BORDER TRIME HEIGHTS ARE FROM BOTTOM OF GOODS.
 - ALL UNITS HUNG ON 18" CENTERS UNLESS OTHERWISE DIMENSIONED
 - WRITTEN DIMENSIONS TAKE PRECEDENCE OVER SCALE MEASUREMENTS
 - PLEASE SEE HOOKUP FOR COLOR AND ACCESSORY INFORMATION - TOPHAT & BARNDOORS ARE NOT DRAWN ON PLOT
 - PLEASE DROP ALL ACCESSORIES & COLOR PRIOR TO START OF FOCUS. COMPANY TRAVELS WITH FRAMED TEMPLATES AND WILL PROVIDE UPON ARRIVAL.


DISCLAIMER

THIS DRAWING REPRESENTS VISUAL CONCEPTS AND CONSTRUCTION SUGGESTIONS ONLY.

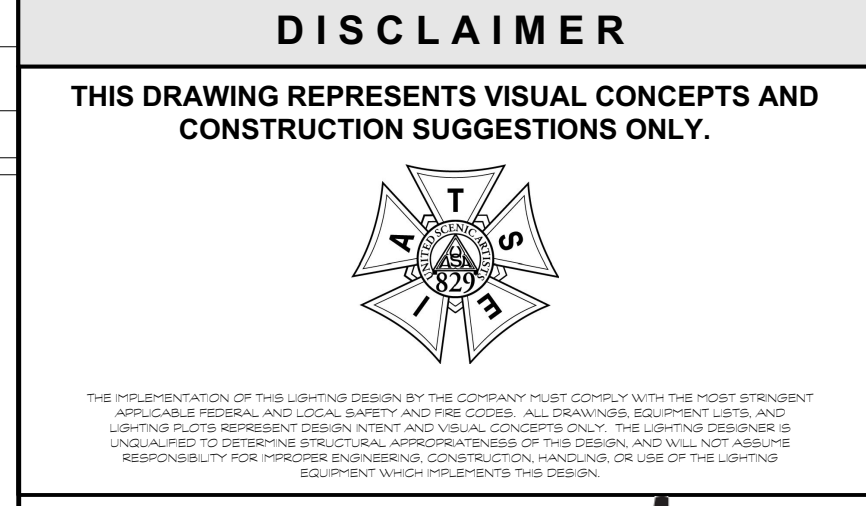


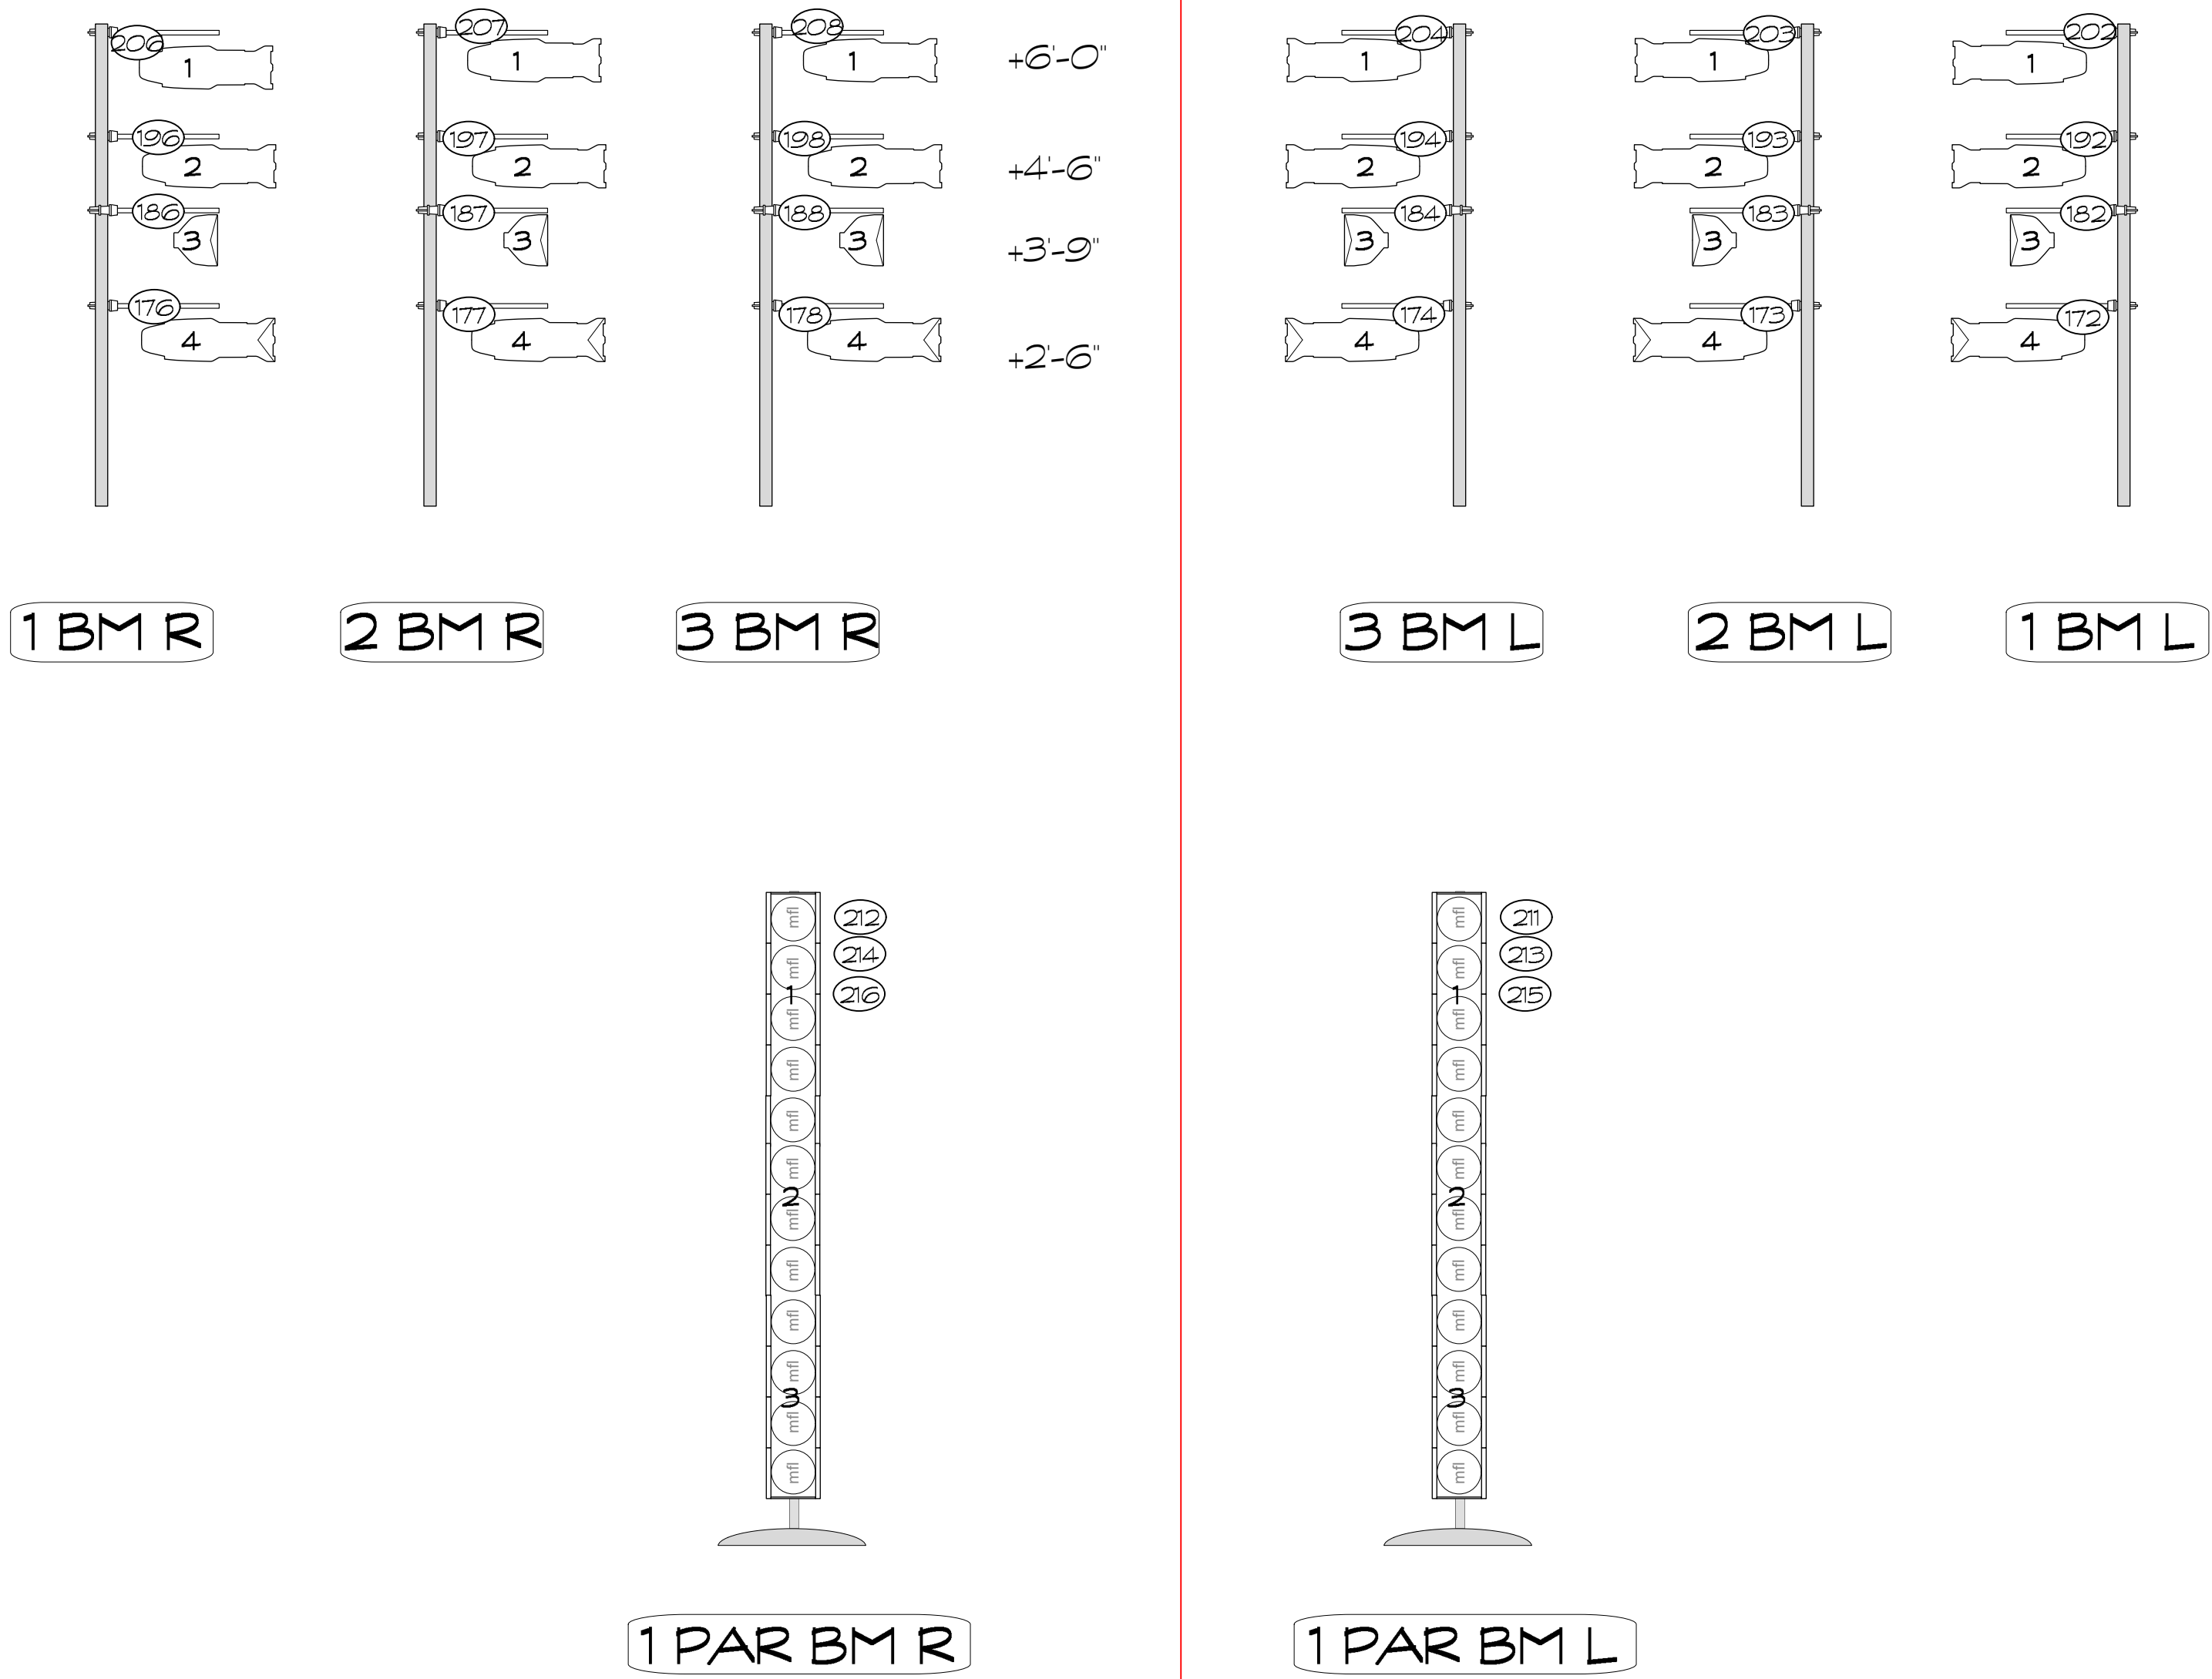


I N S T R U M E N T A T I O N	
	ETC SOURCE 4 50° @575W
	ETC SOURCE 4 36° @575W
	ETC SOURCE 4 26° @575W
	ETC SOURCE 4 19° @575W
	ETC SOURCE 4 LUSTR 50° @171W
	ETC SOURCE 4 LUSTR 36° @171W
	ETC SOURCE 4 LUSTR 19° @171W
	ETC SOURCE 4 TUNG 19° @171W
	ETC SOURCE 4 LUSTR FRESNEL @171W
	ETC D60 DESIRE @171W
	SOURCE 4 PAR WFL @575W
	MARTIN MAC AURA @260W
T Y P I C A L U N I T	
N O T E S	
-ALL EQUIPMENT SUBSTITUTIONS SHOULD BE DISCUSSED WITH THE COMPANY LIGHTING DIRECTOR IN ADVANCE - ALL DIMENSIONS ARE FROM CENTER LINE & PLASTER LINE UNLESS OTHERWISE NOTED - ALL TRIMS ARE FROM STAGE FLOOR TO SIDEARM/PIPE UNLESS NOTED -OVERSTAGE ELECTRIC TRIM HEIGHTS ARE FROM SYSTEM PIPE. BORDER TRIME HEIGHTS ARE FROM BOTTOM OF GOODS. -ALL UNITS HUNG ON 18" CENTERS UNLESS OTHERWISE DIMENSIONED -WRITTEN DIMENSIONS TAKE PRECEDENCE OVER SCALE MEASURMENTS -PLEASE SEE HOOKUP FOR COLOR AND ACCESSORY INFORMATION - TOPHAT & BARNDOORS ARE NOT DRAWN ON PLOT -PLEASE DROP ALL ACCESSORIES & COLOR PRIOR TO START OF FOCUS. COMPANY TRAVELS WITH FRAMED TEMPLATES AND WILL PROVIDE UPON ARRIVAL.	
D I S C L A I M E R	
THIS DRAWING REPRESENTS VISUAL CONCEPTS AND CONSTRUCTION SUGGESTIONS ONLY. THE IMPLEMENTATION OF THIS LIGHTING DESIGN BY THE COMPANY MUST COMPLY WITH THE MOST STRINGENT APPLICABLE FEDERAL AND LOCAL SAFETY AND FIRE CODES. ALL DRAWINGS, EQUIPMENT LISTS AND PARTS LISTS REPRESENT DESIGN INTENT AND VISUAL CONCEPTS ONLY. THE COMPANY DOES NOT UNDERTAKE TO DETERMINE STRUCTURAL APPROPRIATENESS OF THIS DESIGN, AND WILL NOT ASSUME RESPONSIBILITY FOR IMPROPER OR UNUSUAL CONSTRUCTION HANDLING OR USE OF THE LIGHTING EQUIPMENT WHICH PRELUENTS THIS DESIGN.	
FUENTEOVEJUNA	
SCALE: 1/4"=1'-0"	
DRAFTED BY:..... LCA THEATRE DEPARTMENT	
P L A T E	

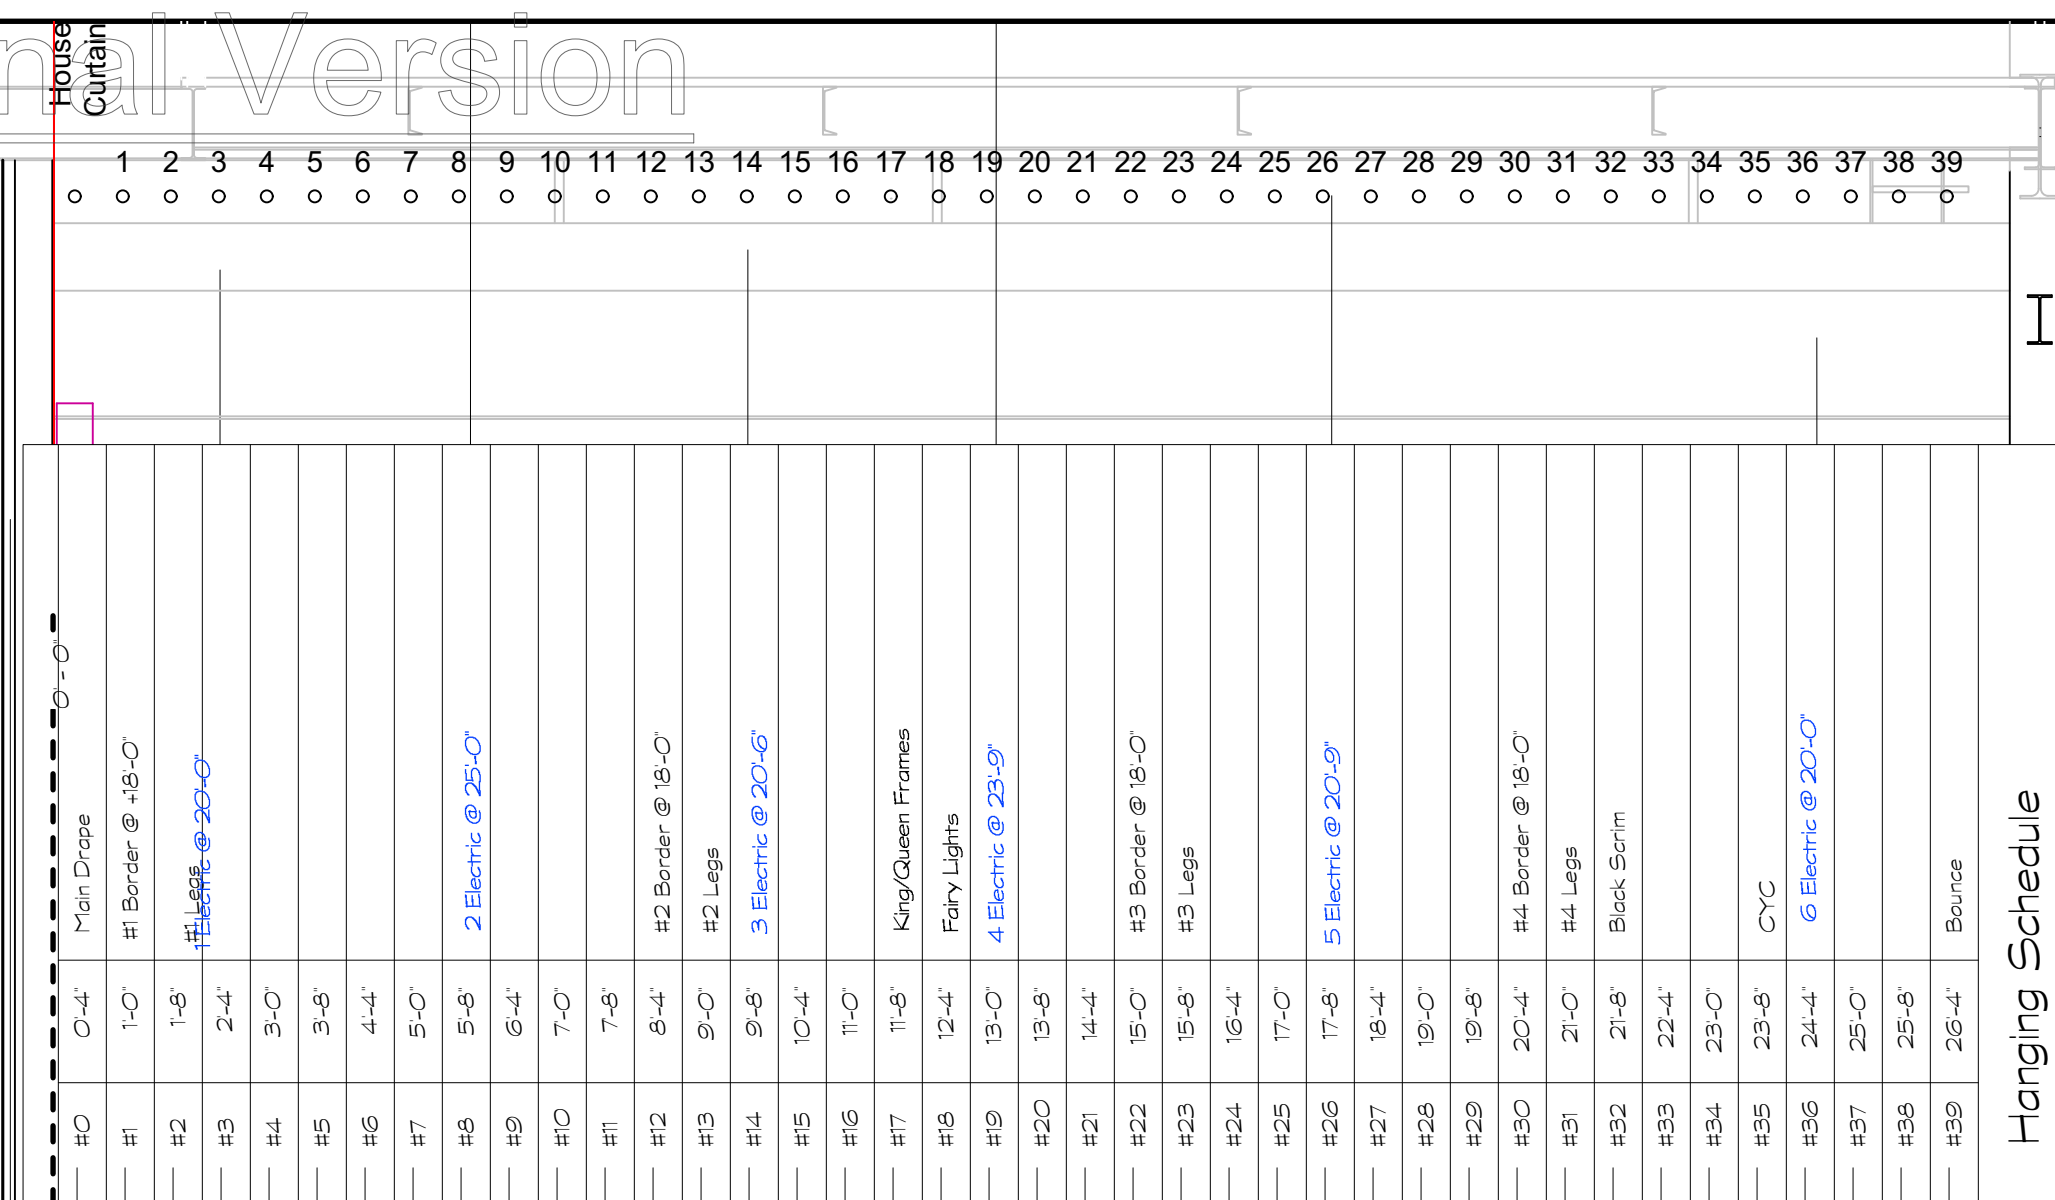

TYPICAL UNIT

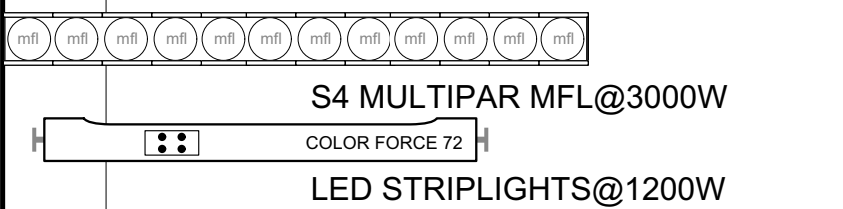

- | | |
|---|--|
| DISCLAIMER | |
| THIS DRAWING REPRESENTS VISUAL CONCEPTS AND
CONSTRUCTION SUGGESTIONS ONLY. | |

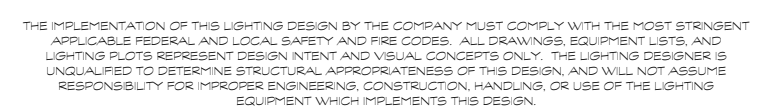

McCarter
THEATRE CENTER

SCALE: 1/4"=1'-0"

DRAFTED BY:..... LCA THEATRE DEPARMENT

PLATE

TABLE OF CONTENTS

Far Cat	1	3 Boom L	9
Mid Cat	2	1 Par Boom L	9
Near Cat	3	1 Boom R	9
Near Cat UUS	3	2 Boom R	9
Near Box Boom L Lo	3	3 Boom R	10
Near Box Boom R Lo	4	1 Par Boom R	10
1st Electric - LS 3	4	Deck Units SL	10
2nd Electric - LS 8	5	Deck Units SR	10
3rd Electric - LS 14	6	Ground Row	11
4th Electric - LS 19	7	Deck LED Tape	11
5th Electric - LS 26	7	Band Standlights	11
6th Electric - LS 36	8	DS Under Deck	12
1 Boom L	8	US Under Platform	12
2 Boom L	8	Fairy Lights	12
		Hazer	12

Berlind Theatre
Lewis Center for the Arts**Far Cat**

U#	Purpose	Inst Type & Access & Load	Color	Chan
1	F/L Wm B	S4 19° 575w	L506+R119	(2)
2	F/L Cool B	S4 19° 575w	L503+R119	(22)
3	Wall Frnt Specials	S4 19° 575w	L248+R132	(301)
4	F/L Wm C	S4 19° 575w	L506+R119	(3)
5	F/L Cool C	S4 19° 575w	L503+R119	(23)
6	SL Aisle	S4 50° 575w	R02+R132	(293)
7	F/L Wm D	S4 19° 575w	L506+R119	(4)
8	F/L Cool D	S4 19° 575w	L503+R119	(24)
9	Wall Frnt Specials	S4 19° 575w	L248+R132	(302)
10	F/L Wm A	S4 19° 575w	L506+R119	(1)
11	F/L Wm E	S4 19° 575w	L506+R119	(5)
12	F/L Cool E	S4 19° 575w	L503+R119	(25)
13	F/L Cool A	S4 19° 575w	L503+RR19	(21)
14	Wall Frnt Specials	S4 19° 575w	L248+R132	(303)
15	F/L Wm F	S4 19° 575w	L506+R119	(6)
16	F/L Cool F	S4 19° 575w	L503+R119	(26)
17	SR Aisle	S4 50° 575w	R02+R132	(296)
18	Wall Frnt Specials	S4 19° 575w	L248+R132	(304)

Mid Cat

U#	Purpose	Inst Type & Access & Load	Color	Chan
1	Reading Light Backup	S4 26° 575w	R132	(261)
2	F/L Wm G	S4 26° 575w	L506+R119	(7)
3	F/L Cool G	S4 26° 575w	L503+R119	(27)
4	SL Aisle	S4 50° 575w	R02+R132	(292)
5	F/L Wm H	S4 26° 575w	L506+R119	(8)
6	F/L Cool H	S4 26° 575w	L503+R119	(28)
7	ML	Martin Mac Aura 260w	NC	(251)
8	F/L Wm I	S4 26° 575w	L506+R119	(9)
9	F/L Cool I	S4 26° 575w	L503+R119	(29)
9	ML	Martin Mac Aura 260w	NC	(252)
10	F/L Wm J	S4 26° 575w	L506+R119	(10)
11	F/L Cool J	S4 26° 575w	L503+R119	(30)
12	SR Aisle	S4 50° 575w	R02+R132	(295)
13	Band F/L M	S4 19° 575w	L503+R119	(42)
14	F/L Wm K	S4 26° 575w	L506+R119	(11)
15	Band F/L L	S4 19° 575w	L503+R119	(41)
16	F/L Cool K	S4 26° 575w	L503+R119	(31)
17	Band F/L N	S4 19° 575w	L503+R119	(43)
18	Reading Light Backup	S4 26° 575w	R132	(262)
FS1	Follow Spot	S4 Lustr2 19° 171w	R132	(Fs)
FS2	Follow Spot	S4 Lustr2 19° 171w	R132	(Fs)

Near Cat

U#	Purpose	Inst Type & Access & Load	Color	Chan
1	SL Aisle	S4 50° 575w	R02+R132	(291)
2	I-Cue	S4 19° 575w	R132	(311)
2i	I-Cue	I-Cue		(311)
3	I-Cue	S4 19° 575w	R132	(312)
3i	I-Cue	I-Cue		(312)
4	SR Aisle	S4 50° 575w	R02+R132	(294)
5	Band F/L O	S4 26° 575w	L503+R119	(44)

Near Cat UUS

U#	Purpose	Inst Type & Access & Load	Color	Chan
1	S/L NR DS	S4 Lustr2 36° 171w	R132	(131)
2	S/L C DS	S4 Lustr2 26° 171w	R132	(132)
3	S/L C DS	S4 Lustr2 19° 171w	R132	(133)
4	T/L A	S4 Lustr2 50° 171w	R119	(51)
5	S/L C DS	S4 Lustr2 19° 171w	R132	(141)
6	S/L C DS	S4 Lustr2 26° 171w	R132	(142)
7	S/L NR DS	S4 Lustr2 36° 171w	R132	(143)

Near Box Boom L Lo

U#	Purpose	Inst Type & Access & Load	Color	Chan
1	High Head	S4 36° 575w	L048+R132	(201)
2	Head	S4 36° 575w	L733+R132	(191)
3	Par Mid	S4 PAR WFL 575w	R39	(181)
4	High Shin	S4 50° 575w	R53+R132	(171)

Near Box Boom R Lo

U#	Purpose	Inst Type & Access & Load	Color	Chan
1	High Head	S4 36° 575w	L704+R132	(205)
2	Head	S4 36° 575w	L224+R132	(195)
3	Par Mid	S4 PAR WFL 575w	R39	(185)
4	High Shin	S4 50° 575w	R54+R132	(175)

1st Electric - LS 3

U#	Purpose	Inst Type & Access & Load	Color	Chan
1	S/L NR MS	S4 Lustr2 36° 171w	R132	(134)
2	S/L C MS	S4 Lustr2 26° 171w	R132	(135)
3	S/L C MS	S4 Lustr2 19° 171w	R132	(136)
4	B/L M	ETC D60 Lustr SELO3070 161w	WO Lens	(72)
5	B/L L	ETC D60 Lustr SELO3070 161w	WO Lens	(71)
6	B/L N	ETC D60 Lustr SELO3070 161w	WO Lens	(73)
7	S/L C MS	S4 Lustr2 19° 171w	R132	(144)
8	S/L C MS	S4 Lustr2 26° 171w	R132	(145)
9	S/L NR MS	S4 Lustr2 36° 171w	R132	(146)

2nd Electric - LS 8

U#	Purpose	Inst Type & Access & Load	Color	Chan
1	T/L B	S4 Lustr2Fresnel 171w	NC	(52)
2	T/L C	S4 Lustr2Fresnel 171w	NC	(53)
3	T/L D	S4 Lustr2Fresnel 171w	NC	(54)
4	B/L Wm A	S4 PAR WFL 575w	L442	(81)
5	T/L E	S4 Lustr2Fresnel 171w	NC	(55)
6	B/L Cool A	S4 PAR WFL 575w	L501	(101)
7	T/L F	S4 Lustr2Fresnel 171w	NC	(56)
8	B/L Cool M	ETC D60 Lustr SELO3070 161w	WO Lens	(122)
9	B/L Cool L	ETC D60 Lustr SELO3070 161w	WO Lens	(121)
10	B/L O	ETC D60 Lustr SELO3070 161w	WO Lens	(74)
11	B/L Cool N	ETC D60 Lustr SELO3070 161w	WO Lens	(123)

3rd Electric - LS 14

U#	Purpose	Inst Type & Access & Load	Color	Chan
1	S/L NR US	S4 Lustr2 36° 171w	R132	(137)
2	S/L C US	S4 Lustr2 26° 171w	R132	(138)
3	S/L C US	S4 Lustr2 19° 171w	R132	(139)
4	B/L Wm B	S4 PAR WFL 575w	L442	(82)
5	B/L Cool B	S4 PAR WFL 575w	L501	(102)
6	B/L Wm C	S4 PAR WFL 575w	L442	(83)
7	B/L Cool C	S4 PAR WFL 575w	L501	(103)
8	US Wall Scrape	S4 50° 575w	L790+R119	(271)
9	Stain Glass Wall Scrape	S4 50° 575w	NC	(281)
10	B/L Wm D	S4 PAR WFL 575w	L442	(84)
11	B/L Cool D	S4 PAR WFL 575w	L501	(104)
12	US Wall Scrape	S4 50° 575w	L790+R119	(272)
13	Stain Glass Wall Scrape	S4 50° 575w	NC	(282)
14	B/L Wm E	S4 PAR WFL 575w	L442	(85)
15	B/L Cool E	S4 PAR WFL 575w	L501	(105)
16	US Wall Scrape	S4 50° 575w	L790+R119	(273)
17	Stain Glass Wall Scrape	S4 50° 575w	NC	(283)
18	B/L Wm F	S4 PAR WFL 575w	L442	(86)
19	B/L Cool F	S4 PAR WFL 575w	L501	(106)
20	US Wall Scrape	S4 50° 575w	L790+R119	(274)
21	Stain Glass Wall Scrape	S4 50° 575w	NC	(284)
22	B/L Cool O	ETC D60 Lustr SELO3070 161w	WO Lens	(124)
23	S/L C US	S4 Lustr2 19° 171w	R132	(147)
24	S/L C US	S4 Lustr2 26° 171w	R132	(148)
25	S/L NR US	S4 Lustr2 36° 171w	R132	(149)

4th Electric - LS 19

U#	Purpose	Inst Type & Access & Load	Color	Chan
1	T/L G	S4 Lustr2Fresnel 171w	NC	(57)
2	T/L H	S4 Lustr2Fresnel 171w	NC	(58)
3	T/L I	S4 Lustr2Fresnel 171w	NC	(59)
4	T/L J	S4 Lustr2Fresnel 171w	NC	(60)
5	T/L K	S4 Lustr2Fresnel 171w	NC	(61)

5th Electric - LS 26

U#	Purpose	Inst Type & Access & Load	Color	Chan
1	B/L Wm G	S4 PAR WFL 575w	L442	(87)
2	B/L Cool G	S4 PAR WFL 575w	L501	(107)
3	B/L Wm H	S4 PAR WFL 575w	L442	(88)
4	B/L Cool H	S4 PAR WFL 575w	L501	(108)
5	B/L Wm I	S4 PAR WFL 575w	L442	(89)
6	B/L Cool I	S4 PAR WFL 575w	L501	(109)
7	B/L Wm J	S4 PAR WFL 575w	L442	(90)
8	B/L Cool J	S4 PAR WFL 575w	L501	(110)
9	B/L Wm K	S4 PAR WFL 575w	L442	(91)
10	F/L Cool K	S4 PAR WFL 575w	L501	(111)

6th Electric - LS 36

U#	Purpose	Inst Type & Access & Load	Color	Chan
1	LED Ground Row	Chroma-Q Color Force 72 720w	NC	(221)
2	LED Ground Row	Chroma-Q Color Force 72 720w	NC	(222)
3	LED Ground Row	Chroma-Q Color Force 72 720w	NC	(223)
4	LED Ground Row	Chroma-Q Color Force 72 720w	NC	(224)
5	LED Ground Row	Chroma-Q Color Force 72 720w	NC	(225)
6	LED Ground Row	Chroma-Q Color Force 72 720w	NC	(226)
7	LED Ground Row	Chroma-Q Color Force 72 720w	NC	(227)

1 Boom L

U#	Purpose	Inst Type & Access & Load	Color	Chan
1	High Head	S4 36° 575w	L048+R132	(202)
2	Head	S4 36° 575w	L733+R132	(192)
3	Par Mid	S4 PAR WFL 575w	R39	(182)
4	High Shin	S4 50° 575w	R53+R132	(172)

2 Boom L

U#	Purpose	Inst Type & Access & Load	Color	Chan
1	High Head	S4 36° 575w	L048+R132	(203)
2	Head	S4 36° 575w	L733+R132	(193)
3	Par Mid	S4 PAR WFL 575w	R39	(183)
4	High Shin	S4 50° 575w	R53+R132	(173)

3 Boom L

U#	Purpose	Inst Type & Access & Load	Color	Chan
1	High Head	S4 36° 575w	L048+R132	(204)
2	Head	S4 36° 575w	L733+R132	(194)
3	Par Mid	S4 PAR WFL 575w	R39	(184)
4	High Shin	S4 50° 575w	R53+R132	(174)

1 Par Boom L

U#	Purpose	Inst Type & Access & Load	Color	Chan
1	Color 1	S4 MultiPAR MFL 3kW	L507	(211)
2	Color 2	S4 MultiPAR MFL 3kW	L139	(213)
3	Color 3	S4 MultiPAR MFL 3kW	R80	(215)

1 Boom R

U#	Purpose	Inst Type & Access & Load	Color	Chan
1	High Head	S4 36° 575w	L704+R132	(206)
2	Head	S4 36° 575w	L224+R132	(196)
3	Par Mid	S4 PAR WFL 575w	R39	(186)
4	High Shin	S4 50° 575w	R54+R132	(176)

2 Boom R

U#	Purpose	Inst Type & Access & Load	Color	Chan
1	High Head	S4 36° 575w	L704+R132	(207)
2	Head	S4 36° 575w	L224+R132	(197)
3	Par Mid	S4 PAR WFL 575w	R39	(187)
4	High Shin	S4 50° 575w	R54+R132	(177)

3 Boom R

U#	Purpose	Inst Type & Access & Load	Color	Chan
1	High Head	S4 36° 575w	L704+R132	(208)
2	Head	S4 36° 575w	L224+R132	(198)
3	Par Mid	S4 PAR WFL 575w	R39	(188)
4	High Shin	S4 50° 575w	R54+R132	(178)

1 Par Boom R

U#	Purpose	Inst Type & Access & Load	Color	Chan
1	Color 1	S4 MultiPAR MFL 3kW	L507	(212)
2	Color 2	S4 MultiPAR MFL 3kW	L139	(214)
3	Color 3	S4 MultiPAR MFL 3kW	R80	(216)

Deck Units SL

U#	Purpose	Inst Type & Access & Load	Color	Chan
1	Deck Specials	S4 36° 575w	L651+R132	(241)
2	Deck Specials	S4 36° 575w	L651+R132	(242)
3	Deck Specials	S4 36° 575w	L651+R132	(243)

Deck Units SR

U#	Purpose	Inst Type & Access & Load	Color	Chan
1	Deck Specials	S4 36° 575w	L354+R132	(244)
2	Deck Specials	S4 36° 575w	L354+R132	(245)
3	Deck Specials	S4 36° 575w	L354+R132	(246)

Ground Row

U#	Purpose	Inst Type & Access & Load	Color	Chan
1	LED Ground Row	Chroma-Q Color Force 72 720w	NC	(231)
2	LED Ground Row	Chroma-Q Color Force 72 720w	NC	(232)
3	LED Ground Row	Chroma-Q Color Force 72 720w	NC	(233)
4	LED Ground Row	Chroma-Q Color Force 72 720w	NC	(234)
5	LED Ground Row	Chroma-Q Color Force 72 720w	NC	(235)
6	LED Ground Row	Chroma-Q Color Force 72 720w	NC	(236)
7	LED Ground Row	Chroma-Q Color Force 72 720w	NC	(237)

Deck LED Tape

U#	Purpose	Inst Type & Access & Load	Color	Chan
1	Band Platform LED Tape	RGB LED Tape Band Platform 25w	NC	(322)
2	US Platform LED Tape	RGB LED Tape 15'-0" 25w	NC	(321)

Band Standlights

U#	Purpose	Inst Type & Access & Load	Color	Chan
1	Standlights	Standlights	NC	(350)

DS Under Deck

U#	Purpose	Inst Type & Access & Load	Color	Chan
1	DS Deck Wm	S4 PAR WFL 575w	L651+R132	(331)
2	DS Deck Cool	S4 PAR WFL 575w	L354+R132	(341)
3	DS Deck Wm	S4 PAR WFL 575w	L651+R132	(331)
4	DS Deck Cool	S4 PAR WFL 575w	L354+R132	(341)
5	DS Deck Wm	S4 PAR WFL 575w	L651+R132	(331)
6	DS Deck Cool	S4 PAR WFL 575w	L354+R132	(341)

US Under Platform

U#	Purpose	Inst Type & Access & Load	Color	Chan
1	US Deck Wm	S4 PAR WFL 575w	L651+R132	(332)
2	US Deck Cool	S4 PAR WFL 575w	L354+R132	(342)
3	US Deck Wm	S4 PAR WFL 575w	L651+R132	(332)
4	US Deck Cool	S4 PAR WFL 575w	L354+R132	(342)
5	US Deck Wm	S4 PAR WFL 575w	L651+R132	(332)
6	US Deck Cool	S4 PAR WFL 575w	L354+R132	(342)

Fairy Lights

U#	Purpose	Inst Type & Access & Load	Color	Chan
1	Fairy Lights	Twinkle Lights	NC	(351)
2	Fairy Lights	Twinkle Lights	NC	(352)
3	Fairy Lights	Twinkle Lights	NC	(353)

Hazer

U#	Purpose	Inst Type & Access & Load	Color	Chan
1	Hazer	MDG Hazer		(560)

Channel	U#	Position	Purpose	Inst Type & Load	Color
(1)	10	Far Cat	F/L Wm A	S4 19° 575w	L506+R119
(2)	1	Far Cat	F/L Wm B	S4 19° 575w	L506+R119
(3)	4	Far Cat	F/L Wm C	S4 19° 575w	L506+R119
(4)	7	Far Cat	F/L Wm D	S4 19° 575w	L506+R119
(5)	11	Far Cat	F/L Wm E	S4 19° 575w	L506+R119
(6)	15	Far Cat	F/L Wm F	S4 19° 575w	L506+R119
(7)	2	Mid Cat	F/L Wm G	S4 26° 575w	L506+R119
(8)	5	Mid Cat	F/L Wm H	S4 26° 575w	L506+R119
(9)	8	Mid Cat	F/L Wm I	S4 26° 575w	L506+R119
(10)	10	Mid Cat	F/L Wm J	S4 26° 575w	L506+R119
(11)	14	Mid Cat	F/L Wm K	S4 26° 575w	L506+R119
(21)	13	Far Cat	F/L Cool A	S4 19° 575w	L503+RR19
(22)	2	Far Cat	F/L Cool B	S4 19° 575w	L503+R119
(23)	5	Far Cat	F/L Cool C	S4 19° 575w	L503+R119
(24)	8	Far Cat	F/L Cool D	S4 19° 575w	L503+R119
(25)	12	Far Cat	F/L Cool E	S4 19° 575w	L503+R119
(26)	16	Far Cat	F/L Cool F	S4 19° 575w	L503+R119
(27)	3	Mid Cat	F/L Cool G	S4 26° 575w	L503+R119
(28)	6	Mid Cat	F/L Cool H	S4 26° 575w	L503+R119
(29)	9	Mid Cat	F/L Cool I	S4 26° 575w	L503+R119
(30)	11	Mid Cat	F/L Cool J	S4 26° 575w	L503+R119
(31)	16	Mid Cat	F/L Cool K	S4 26° 575w	L503+R119
(41)	15	Mid Cat	Band F/L L	S4 19° 575w	L503+R119
(42)	13	Mid Cat	Band F/L M	S4 19° 575w	L503+R119

Channel	U#	Position	Purpose	Inst Type & Load	Color
(43)	17	Mid Cat	Band F/L N	S4 19° 575w	L503+R119
(44)	5	Near Cat	Band F/L O	S4 26° 575w	L503+R119
(51)	4	Near Cat UUS	T/L A	S4 Lustr2 50° 171w	R119
(52)	1	2nd Electric - LS 8	T/L B	S4 Lustr2Fresnel 171w	NC
(53)	2	2nd Electric - LS 8	T/L C	S4 Lustr2Fresnel 171w	NC
(54)	3	2nd Electric - LS 8	T/L D	S4 Lustr2Fresnel 171w	NC
(55)	5	2nd Electric - LS 8	T/L E	S4 Lustr2Fresnel 171w	NC
(56)	7	2nd Electric - LS 8	T/L F	S4 Lustr2Fresnel 171w	NC
(57)	1	4th Electric - LS 19	T/L G	S4 Lustr2Fresnel 171w	NC
(58)	2	4th Electric - LS 19	T/L H	S4 Lustr2Fresnel 171w	NC
(59)	3	4th Electric - LS 19	T/L I	S4 Lustr2Fresnel 171w	NC
(60)	4	4th Electric - LS 19	T/L J	S4 Lustr2Fresnel 171w	NC
(61)	5	4th Electric - LS 19	T/L K	S4 Lustr2Fresnel 171w	NC
(71)	5	1st Electric - LS 3	B/L L	ETC D60 Lustr SELO3070 161w	WO Lens
(72)	4	1st Electric - LS 3	B/L M	ETC D60 Lustr SELO3070 161w	WO Lens
(73)	6	1st Electric - LS 3	B/L N	ETC D60 Lustr SELO3070 161w	WO Lens
(74)	10	2nd Electric - LS 8	B/L O	ETC D60 Lustr SELO3070 161w	WO Lens
(81)	4	2nd Electric - LS 8	B/L Wm A	S4 PAR WFL 575w	L442
(82)	4	3rd Electric - LS 14	B/L Wm B	S4 PAR WFL 575w	L442

Channel	U#	Position	Purpose	Inst Type & Load	Color
(83)	6	3rd Electric - LS 14	B/L Wm C	S4 PAR WFL 575w	L442
(84)	10	3rd Electric - LS 14	B/L Wm D	S4 PAR WFL 575w	L442
(85)	14	3rd Electric - LS 14	B/L Wm E	S4 PAR WFL 575w	L442
(86)	18	3rd Electric - LS 14	B/L Wm F	S4 PAR WFL 575w	L442
(87)	1	5th Electric - LS 26	B/L Wm G	S4 PAR WFL 575w	L442
(88)	3	5th Electric - LS 26	B/L Wm H	S4 PAR WFL 575w	L442
(89)	5	5th Electric - LS 26	B/L Wm I	S4 PAR WFL 575w	L442
(90)	7	5th Electric - LS 26	B/L Wm J	S4 PAR WFL 575w	L442
(91)	9	5th Electric - LS 26	B/L Wm K	S4 PAR WFL 575w	L442
(101)	6	2nd Electric - LS 8	B/L Cool A	S4 PAR WFL 575w	L501
(102)	5	3rd Electric - LS 14	B/L Cool B	S4 PAR WFL 575w	L501
(103)	7	3rd Electric - LS 14	B/L Cool C	S4 PAR WFL 575w	L501
(104)	11	3rd Electric - LS 14	B/L Cool D	S4 PAR WFL 575w	L501
(105)	15	3rd Electric - LS 14	B/L Cool E	S4 PAR WFL 575w	L501
(106)	19	3rd Electric - LS 14	B/L Cool F	S4 PAR WFL 575w	L501
(107)	2	5th Electric - LS 26	B/L Cool G	S4 PAR WFL 575w	L501
(108)	4	5th Electric - LS 26	B/L Cool H	S4 PAR WFL 575w	L501
(109)	6	5th Electric - LS 26	B/L Cool I	S4 PAR WFL 575w	L501
(110)	8	5th Electric - LS 26	B/L Cool J	S4 PAR WFL 575w	L501
(111)	10	5th Electric - LS 26	F/L Cool K	S4 PAR WFL 575w	L501
(121)	9	2nd Electric - LS 8	B/L Cool L	ETC D60 Lustr SELO3070 161w	WO Lens
(122)	8	2nd Electric - LS 8	B/L Cool M	ETC D60 Lustr SELO3070 161w	WO Lens
(123)	11	2nd Electric - LS 8	B/L Cool N	ETC D60 Lustr SELO3070 161w	WO Lens
(124)	22	3rd Electric - LS 14	B/L Cool O	ETC D60 Lustr SELO3070 161w	WO Lens

Channel	U#	Position	Purpose	Inst Type & Load	Color
(131)	1	Near Cat UUS	S/L NR DS	S4 Lustr2 36° 171w	R132
(132)	2	Near Cat UUS	S/L C DS	S4 Lustr2 26° 171w	R132
(133)	3	Near Cat UUS	S/L C DS	S4 Lustr2 19° 171w	R132
(134)	1	1st Electric - LS 3	S/L NR MS	S4 Lustr2 36° 171w	R132
(135)	2	1st Electric - LS 3	S/L C MS	S4 Lustr2 26° 171w	R132
(136)	3	1st Electric - LS 3	S/L C MS	S4 Lustr2 19° 171w	R132
(137)	1	3rd Electric - LS 14	S/L NR US	S4 Lustr2 36° 171w	R132
(138)	2	3rd Electric - LS 14	S/L C US	S4 Lustr2 26° 171w	R132
(139)	3	3rd Electric - LS 14	S/L C US	S4 Lustr2 19° 171w	R132
(141)	5	Near Cat UUS	S/L C DS	S4 Lustr2 19° 171w	R132
(142)	6	Near Cat UUS	S/L C DS	S4 Lustr2 26° 171w	R132
(143)	7	Near Cat UUS	S/L NR DS	S4 Lustr2 36° 171w	R132
(144)	7	1st Electric - LS 3	S/L C MS	S4 Lustr2 19° 171w	R132
(145)	8	1st Electric - LS 3	S/L C MS	S4 Lustr2 26° 171w	R132
(146)	9	1st Electric - LS 3	S/L NR MS	S4 Lustr2 36° 171w	R132
(147)	23	3rd Electric - LS 14	S/L C US	S4 Lustr2 19° 171w	R132
(148)	24	3rd Electric - LS 14	S/L C US	S4 Lustr2 26° 171w	R132
(149)	25	3rd Electric - LS 14	S/L NR US	S4 Lustr2 36° 171w	R132
(171)	4	Near Box Boom L Lo	High Shin	S4 50° 575w	R53+R132
(172)	4	1 Boom L	High Shin	S4 50° 575w	R53+R132
(173)	4	2 Boom L	High Shin	S4 50° 575w	R53+R132
(174)	4	3 Boom L	High Shin	S4 50° 575w	R53+R132
(175)	4	Near Box Boom R Lo	High Shin	S4 50° 575w	R54+R132
(176)	4	1 Boom R	High Shin	S4 50° 575w	R54+R132

Channel	U#	Position	Purpose	Inst Type & Load	Color
(177)	4	2 Boom R	High Shin	S4 50° 575w	R54+R132
(178)	4	3 Boom R	High Shin	S4 50° 575w	R54+R132
(181)	3	Near Box Boom L Lo	Par Mid	S4 PAR WFL 575w	R39
(182)	3	1 Boom L	Par Mid	S4 PAR WFL 575w	R39
(183)	3	2 Boom L	Par Mid	S4 PAR WFL 575w	R39
(184)	3	3 Boom L	Par Mid	S4 PAR WFL 575w	R39
(185)	3	Near Box Boom R Lo	Par Mid	S4 PAR WFL 575w	R39
(186)	3	1 Boom R	Par Mid	S4 PAR WFL 575w	R39
(187)	3	2 Boom R	Par Mid	S4 PAR WFL 575w	R39
(188)	3	3 Boom R	Par Mid	S4 PAR WFL 575w	R39
(191)	2	Near Box Boom L Lo	Head	S4 36° 575w	L733+R132
(192)	2	1 Boom L	Head	S4 36° 575w	L733+R132
(193)	2	2 Boom L	Head	S4 36° 575w	L733+R132
(194)	2	3 Boom L	Head	S4 36° 575w	L733+R132
(195)	2	Near Box Boom R Lo	Head	S4 36° 575w	L224+R132
(196)	2	1 Boom R	Head	S4 36° 575w	L224+R132
(197)	2	2 Boom R	Head	S4 36° 575w	L224+R132
(198)	2	3 Boom R	Head	S4 36° 575w	L224+R132
(201)	1	Near Box Boom L Lo	High Head	S4 36° 575w	L048+R132
(202)	1	1 Boom L	High Head	S4 36° 575w	L048+R132
(203)	1	2 Boom L	High Head	S4 36° 575w	L048+R132
(204)	1	3 Boom L	High Head	S4 36° 575w	L048+R132
(205)	1	Near Box Boom R Lo	High Head	S4 36° 575w	L704+R132

Channel	U#	Position	Purpose	Inst Type & Load	Color
(206)	1	1 Boom R	High Head	S4 36° 575w	L704+R132
(207)	1	2 Boom R	High Head	S4 36° 575w	L704+R132
(208)	1	3 Boom R	High Head	S4 36° 575w	L704+R132
(211)	1	1 Par Boom L	Color 1	S4 MultiPAR MFL 3kW	L507
(212)	1	1 Par Boom R	Color 1	S4 MultiPAR MFL 3kW	L507
(213)	2	1 Par Boom L	Color 2	S4 MultiPAR MFL 3kW	L139
(214)	2	1 Par Boom R	Color 2	S4 MultiPAR MFL 3kW	L139
(215)	3	1 Par Boom L	Color 3	S4 MultiPAR MFL 3kW	R80
(216)	3	1 Par Boom R	Color 3	S4 MultiPAR MFL 3kW	R80
(221)	1	6th Electric - LS 36	LED Ground Row	Chroma-Q Color Force 72 720w	NC
(222)	2	6th Electric - LS 36	LED Ground Row	Chroma-Q Color Force 72 720w	NC
(223)	3	6th Electric - LS 36	LED Ground Row	Chroma-Q Color Force 72 720w	NC
(224)	4	6th Electric - LS 36	LED Ground Row	Chroma-Q Color Force 72 720w	NC
(225)	5	6th Electric - LS 36	LED Ground Row	Chroma-Q Color Force 72 720w	NC
(226)	6	6th Electric - LS 36	LED Ground Row	Chroma-Q Color Force 72 720w	NC
(227)	7	6th Electric - LS 36	LED Ground Row	Chroma-Q Color Force 72 720w	NC
(231)	1	Ground Row	LED Ground Row	Chroma-Q Color Force 72 720w	NC
(232)	2	Ground Row	LED Ground Row	Chroma-Q Color Force 72 720w	NC
(233)	3	Ground Row	LED Ground Row	Chroma-Q Color Force 72 720w	NC

Channel	U#	Position	Purpose	Inst Type & Load	Color
(234)	4	Ground Row	LED Ground Row	Chroma-Q Color Force 72 720w	NC
(235)	5	Ground Row	LED Ground Row	Chroma-Q Color Force 72 720w	NC
(236)	6	Ground Row	LED Ground Row	Chroma-Q Color Force 72 720w	NC
(237)	7	Ground Row	LED Ground Row	Chroma-Q Color Force 72 720w	NC
(241)	1	Deck Units SL	Deck Specials	S4 36° 575w	L651+R132
(242)	2	Deck Units SL	Deck Specials	S4 36° 575w	L651+R132
(243)	3	Deck Units SL	Deck Specials	S4 36° 575w	L651+R132
(244)	1	Deck Units SR	Deck Specials	S4 36° 575w	L354+R132
(245)	2	Deck Units SR	Deck Specials	S4 36° 575w	L354+R132
(246)	3	Deck Units SR	Deck Specials	S4 36° 575w	L354+R132
(251)	7	Mid Cat	ML	Martin Mac Aura 260w	NC
(252)	9	Mid Cat	ML	Martin Mac Aura 260w	NC
(261)	1	Mid Cat	Reading Light Backup	S4 26° 575w	R132
(262)	18	Mid Cat	Reading Light Backup	S4 26° 575w	R132
(271)	8	3rd Electric - LS 14	US Wall Scrape	S4 50° 575w	L790+R119
(272)	12	3rd Electric - LS 14	US Wall Scrape	S4 50° 575w	L790+R119
(273)	16	3rd Electric - LS 14	US Wall Scrape	S4 50° 575w	L790+R119
(274)	20	3rd Electric - LS 14	US Wall Scrape	S4 50° 575w	L790+R119
(281)	9	3rd Electric - LS 14	Stain Glass Wall Scrape	S4 50° 575w	NC
(282)	13	3rd Electric - LS 14	Stain Glass Wall Scrape	S4 50° 575w	NC

Channel	U#	Position	Purpose	Inst Type & Load	Color
(283)	17	3rd Electric - LS 14	Stain Glass Wall Scrape	S4 50° 575w	NC
(284)	21	3rd Electric - LS 14	Stain Glass Wall Scrape	S4 50° 575w	NC
(291)	1	Near Cat	SL Aisle	S4 50° 575w	R02+R132
(292)	4	Mid Cat	SL Aisle	S4 50° 575w	R02+R132
(293)	6	Far Cat	SL Aisle	S4 50° 575w	R02+R132
(294)	4	Near Cat	SR Aisle	S4 50° 575w	R02+R132
(295)	12	Mid Cat	SR Aisle	S4 50° 575w	R02+R132
(296)	17	Far Cat	SR Aisle	S4 50° 575w	R02+R132
(301)	3	Far Cat	Wall Frnt Specials	S4 19° 575w	L248+R132
(302)	9	Far Cat	Wall Frnt Specials	S4 19° 575w	L248+R132
(303)	14	Far Cat	Wall Frnt Specials	S4 19° 575w	L248+R132
(304)	18	Far Cat	Wall Frnt Specials	S4 19° 575w	L248+R132
(311)	2	Near Cat	I-Cue	S4 19° 575w	R132
	2i	"	"	I-Cue	
(312)	3	Near Cat	I-Cue	S4 19° 575w	R132
	3i	"	"	I-Cue	
(321)	2	Deck LED Tape	US Platform LED Tape	RGB LED Tape 15'-0" 25w	NC
(322)	1	Deck LED Tape	Band Platform LED Tape	RGB LED Tape Band Platform 25w	NC
(331)	1	DS Under Deck	DS Deck Wm	S4 PAR WFL 575w	L651+R132
	3	"	"	"	"
	5	"	"	"	"

Channel	U#	Position	Purpose	Inst Type & Load	Color
(332)	1	US Under Platform	US Deck Wm	S4 PAR WFL 575w	L651+R132
	3	"	"	"	"
	5	"	"	"	"
(341)	2	DS Under Deck	DS Deck Cool	S4 PAR WFL 575w	L354+R132
	4	"	"	"	"
	6	"	"	"	"
(342)	2	US Under Platform	US Deck Cool	S4 PAR WFL 575w	L354+R132
	4	"	"	"	"
	6	"	"	"	"
(350)	1	Band Standlights	Standlights	Standlights	NC
(351)	1	Fairy Lights	Fairy Lights	Twikle Lights	NC
(352)	2	Fairy Lights	Fairy Lights	Twikle Lights	NC
(353)	3	Fairy Lights	Fairy Lights	Twikle Lights	NC
(560)	1	Hazer	Hazer	MDG Hazer	

LETTERED Channel

Channel	U#	Position	Purpose	Inst Type & Load	Color
(Fs)	FS 1	Mid Cat	Follow Spot	S4 Lustr2 19° 171w	R132
	FS 2	"	"	"	"